



ENTERO N°
669010634

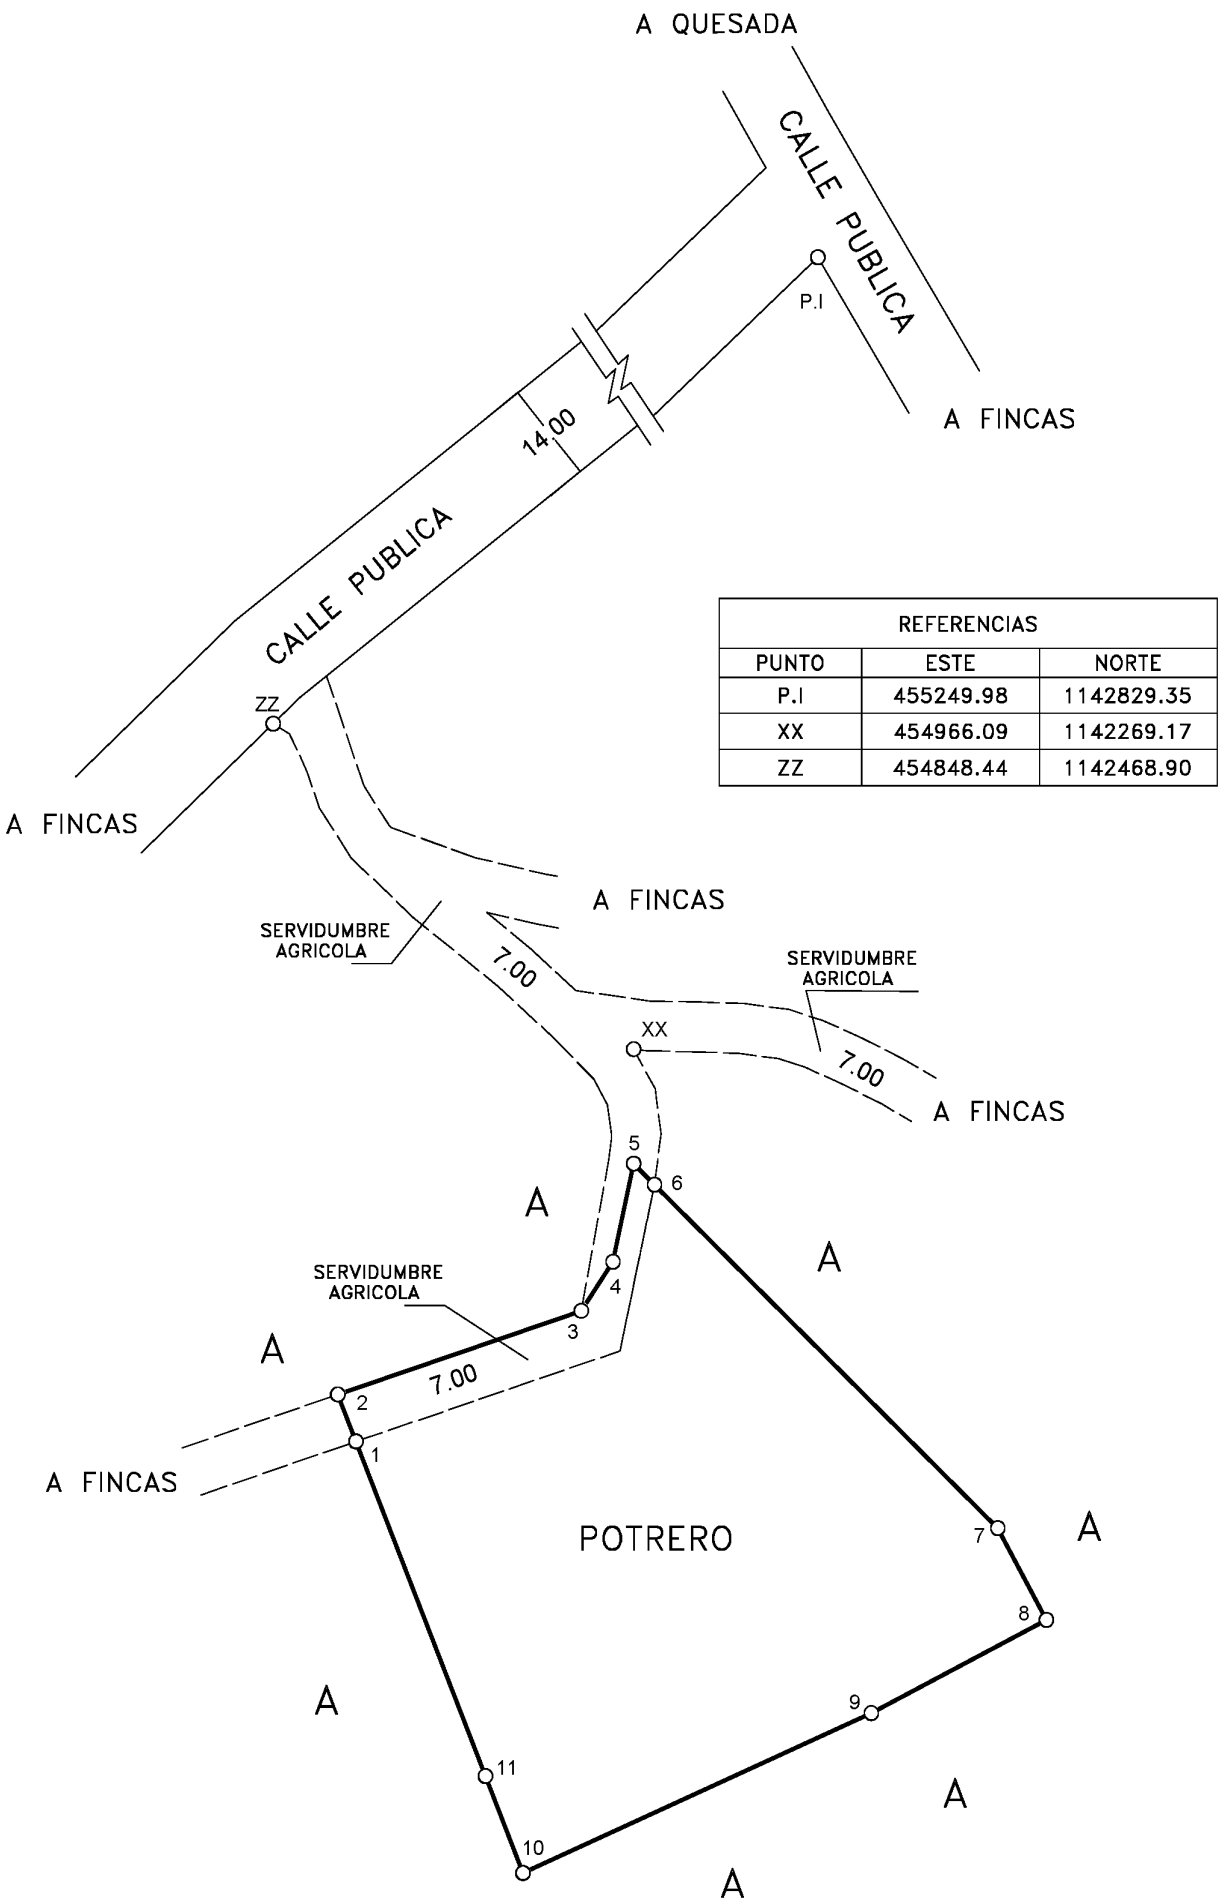

LISTADO DE COORDENADAS		
PUNTO	ESTE (m)	NORTE (m)
1	454929.54	1142193.81
2	454926.97	1142200.33
3	454961.21	1142211.90
4	454965.69	1142218.69
5	454968.55	1142232.24
6	454971.52	1142229.33
7	455019.78	1142181.82
8	455026.60	1142169.14
9	455002.00	1142156.25
10	454953.02	1142134.13
11	454947.74	1142147.54

NOTAS:
-ESCALA DEL MAPA CATASTRAL 1:5000
-EPOCA 2014.59,SISTEMA CR-SIRGAS, PROYECCION CRTM05,
-METODO DE ENLACE A LA RED DE COORDENADAS CRTM05,
MEDICION ENLACE A ESTACION CIQE
-EXACTITUD RELATIVA : +/-0.10m,
-EXACTITUD ABSOLUTA : +/-0.10m
-DOY FE QUE LOS LINDEROS SON EXISTENTES
-TODAS LAS MEDIDAS ESTAN DADAS EN METROS
-MODIFICA AL PLANO CATASTRADO N°A-1630235-2013
-FRETE A SERVIDUMBRE AGRICOLA DE VERTICE 1 AL 6: 69.28m
-PARCELA EXCLUSIVAMENTE PARA USO AGRICOLA
-LOS PUNTOS XX Y ZZ SON VERTICES DE LA SERVIDUMBRE
-COLINDANTE A: 21001050284700.

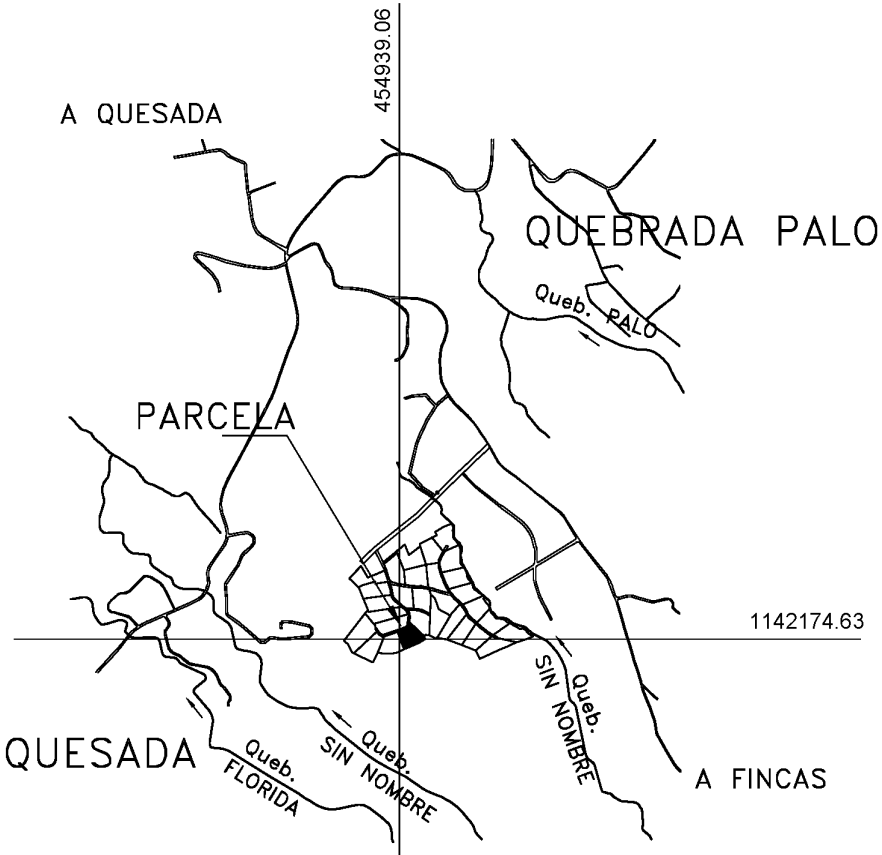

UBICACION GEOGRAFICA
HOJA QUESADA – AGUAS ZARCAS
ESCALA: 1:50,000
AMPLIADA: 1:25,000
EPOCA 2014.59, SISTEMA CR-SIRGAS,
PROYECCION CRTM05

JORGE MARIO GUERRERO VARGAS (FIRMA)

Firmado digitalmente por JORGE MARIO GUERRERO VARGAS (FIRMA)
Fecha: 2026.07.04 16:00:50 -06'00'

JORGE MARIO GUERRERO VARGAS
TOPOGRAFO ASOCIADO: T.A. 8914

PROTOCOLO: TOMO 24381
FOLIO 026

ESCALA 1:1000
FECHA JUNIO 2026

SITUADO EN: LA LLANADA

DISTRITO: 1° QUESADA

CANTON: 10° SAN CARLOS

PROVINCIA: 2° ALAJUELA

PARCELA 31A

AREA
5000.00m²

ES PARTE DE
FOLIO REAL
2 502847-000
IDENTIFICADOR PREDIAL
21001050284700
AREA SEGUN REGISTRO
34ha1697.65m²