



ENTERO N°
669010669

REFERENCIAS		
PUNTO	ESTE	NORTE
P.I	455249.98	1142829.35
XX	454966.09	1142269.17
ZZ	454848.44	1142468.90

LISTADO DE COORDENADAS		
PUNTO	ESTE (m)	NORTE (m)
1	454882.46	1142177.90
2	454873.75	1142182.35
3	454926.97	1142200.33
4	454929.54	1142193.81
5	454947.74	1142147.54
6	454953.02	1142134.13
7	454930.78	1142123.68
8	454909.06	1142118.34
9	454879.40	1142118.96
10	454859.40	1142123.83
11	454865.57	1142137.66

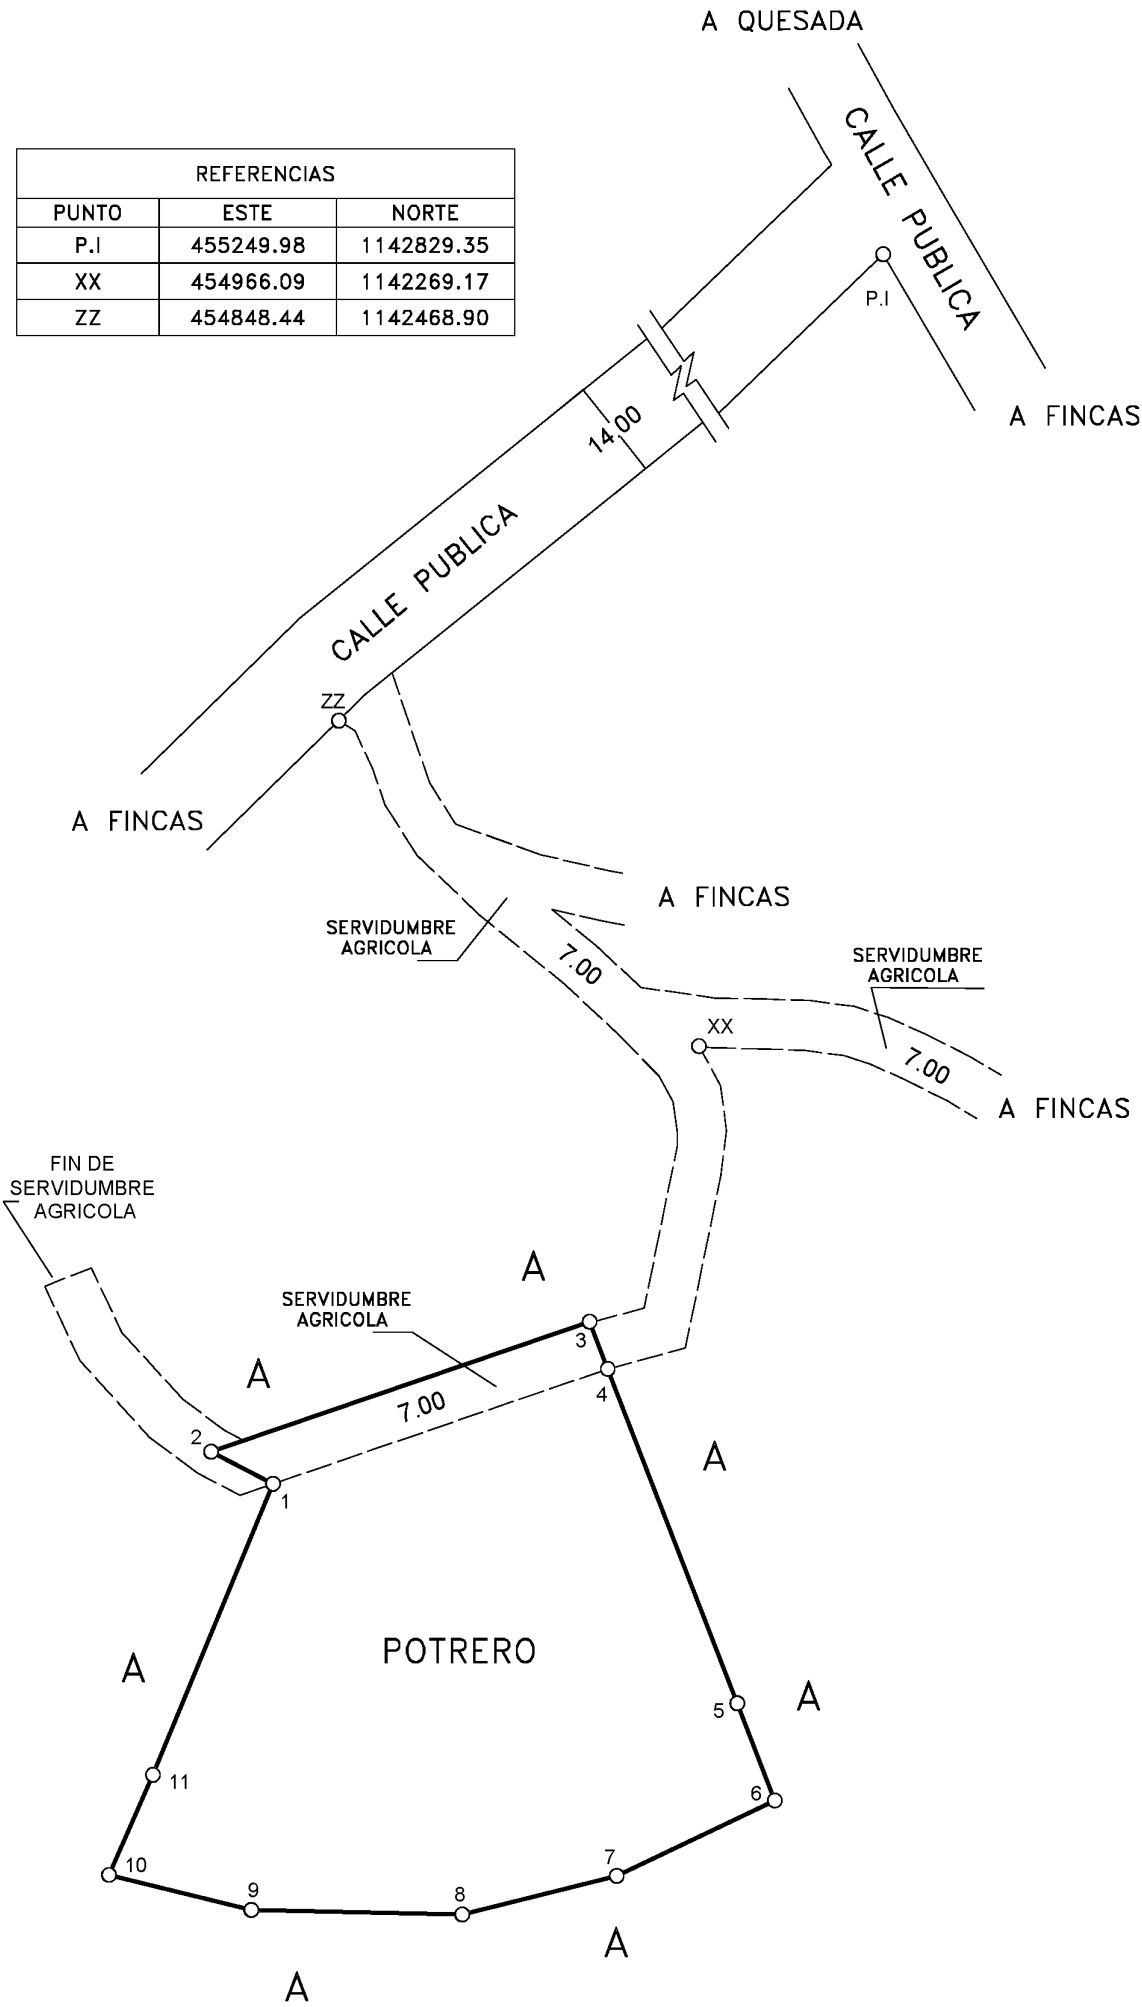

NOTAS:
-ESCALA DEL MAPA CATASTRAL 1:5000
-EPOCA 2014.59,SISTEMA CR-SIRGAS, PROYECCION CRTM05,
-METODO DE ENLACE A LA RED DE COORDENADAS CRTM05,
MEDICION ENLACE A ESTACION CIQE
-EXACTITUD RELATIVA : +/-0.10m,
-EXACTITUD ABSOLUTA : +/-0.10m
-DOY FE QUE LOS LINDEROS SON EXISTENTES
-TODAS LAS MEDIDAS ESTAN DADAS EN METROS
-MODIFICA AL PLANO CATASTRADO N°A-1630235-2013
-FRENTE A SERVIDUMBRE AGRICOLA DE VERTICE 1 AL 4: 72.97m
-PARCELA EXCLUSIVAMENTE PARA USO AGRICOLA
-LOS PUNTOS XX Y ZZ SON VERTICES DE LA SERVIDUMBRE
-COLINDANTE A: 21001050284700.

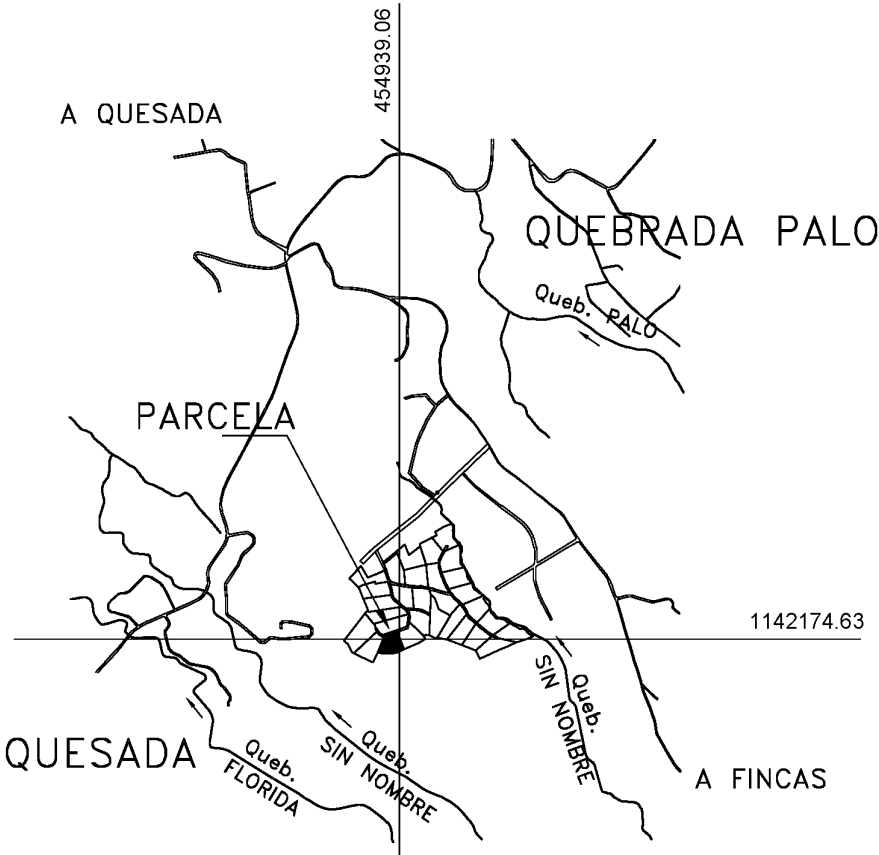

UBICACION GEOGRAFICA

HOJA QUESADA – AGUAS ZARCAS
ESCALA: 1:50,000
AMPLIADA: 1:25,000
EPOCA 2014.59, SISTEMA CR-SIRGAS,
PROYECCION CRTM05

JORGE MARIO GUERRERO VARGAS (FIRMA)
Firmado digitalmente por JORGE MARIO GUERRERO VARGAS (FIRMA)
Fecha: 2026.07.04 16:00:13 -06'00'

JORGE MARIO GUERRERO VARGAS
TOPOGRAFO ASOCIADO: T.A. 8914

PROTOCOLO: TOMO 24381
FOLIO 026

ESCALA 1:1000
FECHA JUNIO 2026

SITUADO EN: LA LLANADA

DISTRITO: 1° QUESADA

CANTON: 10° SAN CARLOS

PROVINCIA: 2° ALAJUELA

PARCELA 31A

AREA

5000.00m²

ES PARTE DE
FOLIO REAL

2 502847-000

IDENTIFICADOR PREDIAL
21001050284700

AREA SEGUN REGISTRO
34ha1697.65m²