


ENTERO N°  
XXXXXXXXXX

|           |                        |           |            |
|-----------|------------------------|-----------|------------|
| 455061.21 | LISTADO DE COORDENADAS |           |            |
|           | PUNTO                  | ESTE (m)  | NORTE (m)  |
|           | 1                      | 455030.71 | 1142618.86 |
|           | 2                      | 455040.59 | 1142628.72 |
|           | 3                      | 455080.26 | 1142575.11 |
|           | 4                      | 455090.42 | 1142557.04 |
|           | 5                      | 455060.96 | 1142540.43 |
|           | 6                      | 455052.00 | 1142556.31 |
|           | 7                      | 455045.53 | 1142565.07 |
|           | 8                      | 455060.53 | 1142578.42 |

|           |                        |
|-----------|------------------------|
| A QUESADA | 1810.36 m <sup>2</sup> |
|-----------|------------------------|

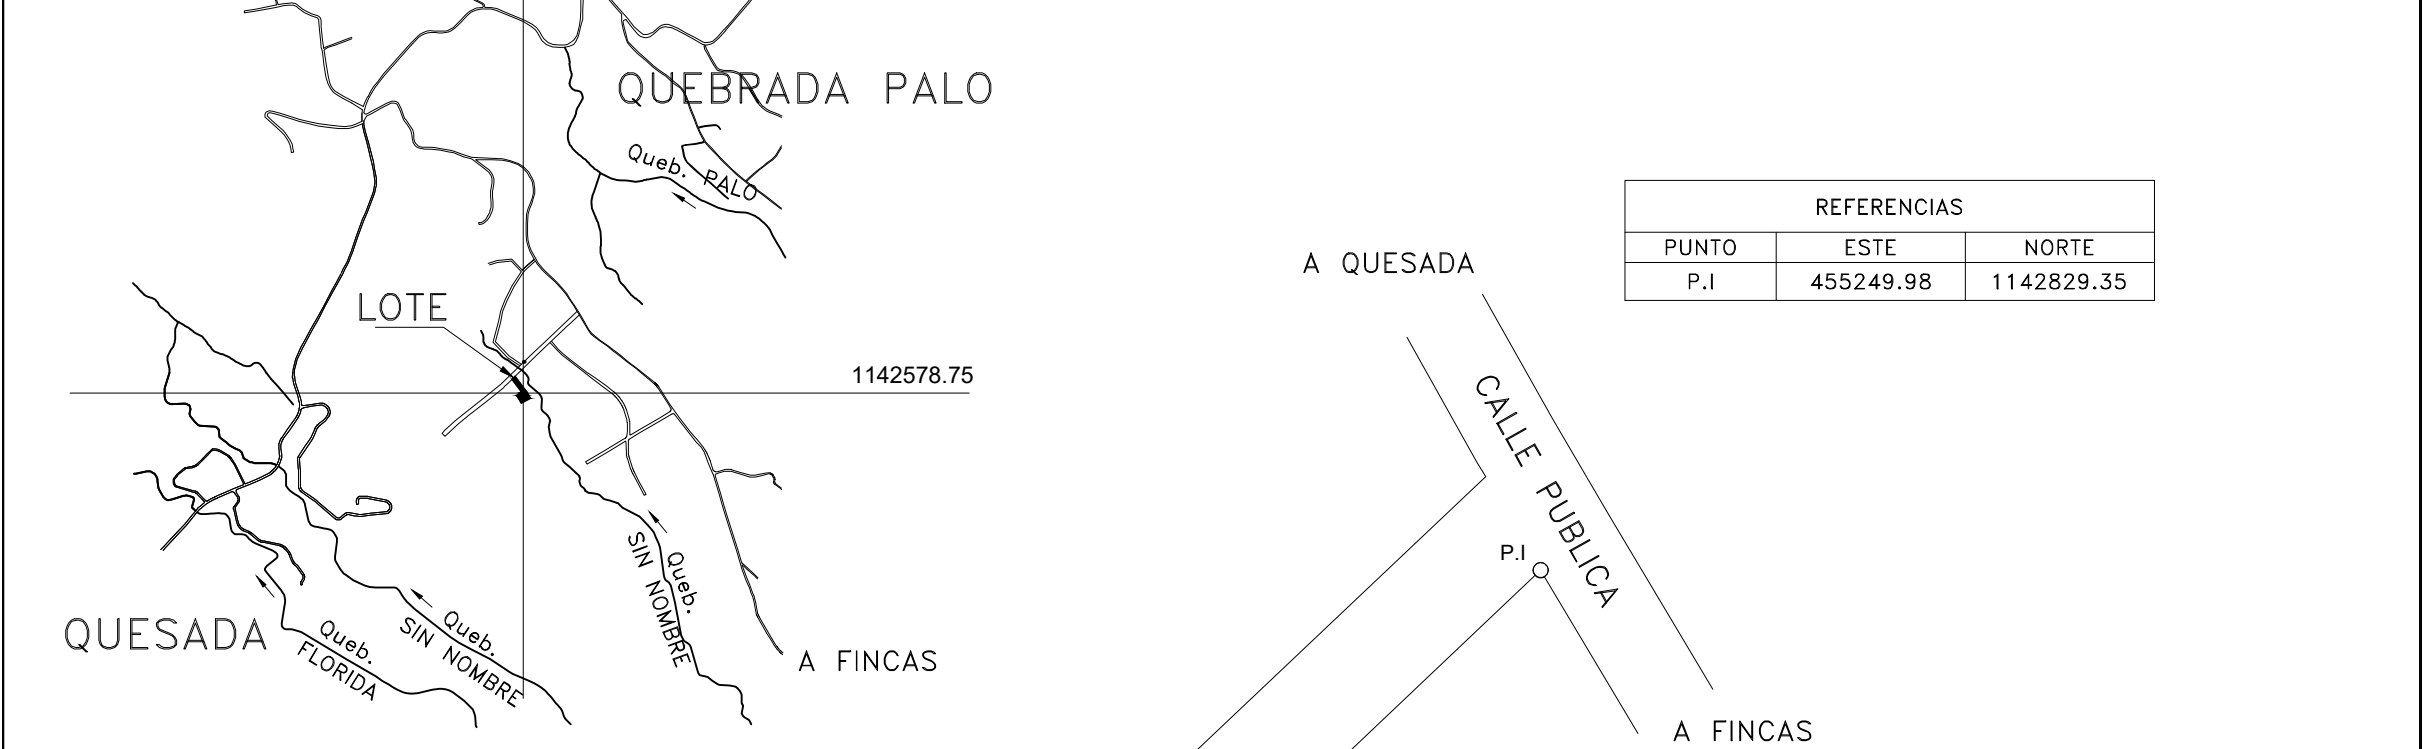

UBICACION GEOGRAFICA

HOJA QUESADA – AGUAS ZARCAS


ESCALA: 1:50,000

AMPLIADA: 1:25,000

EPOCA 2014.59, SISTEMA CR–SIRGAS,  
PROYECCION CRTM05

The map shows a section of a road network. A road labeled 'PUB. 13.96' is shown with a break symbol. Another road labeled 'PRIV. 13.9985' is shown branching off. The map is oriented with the roads running diagonally from the bottom-left towards the top-right.

21001061803500

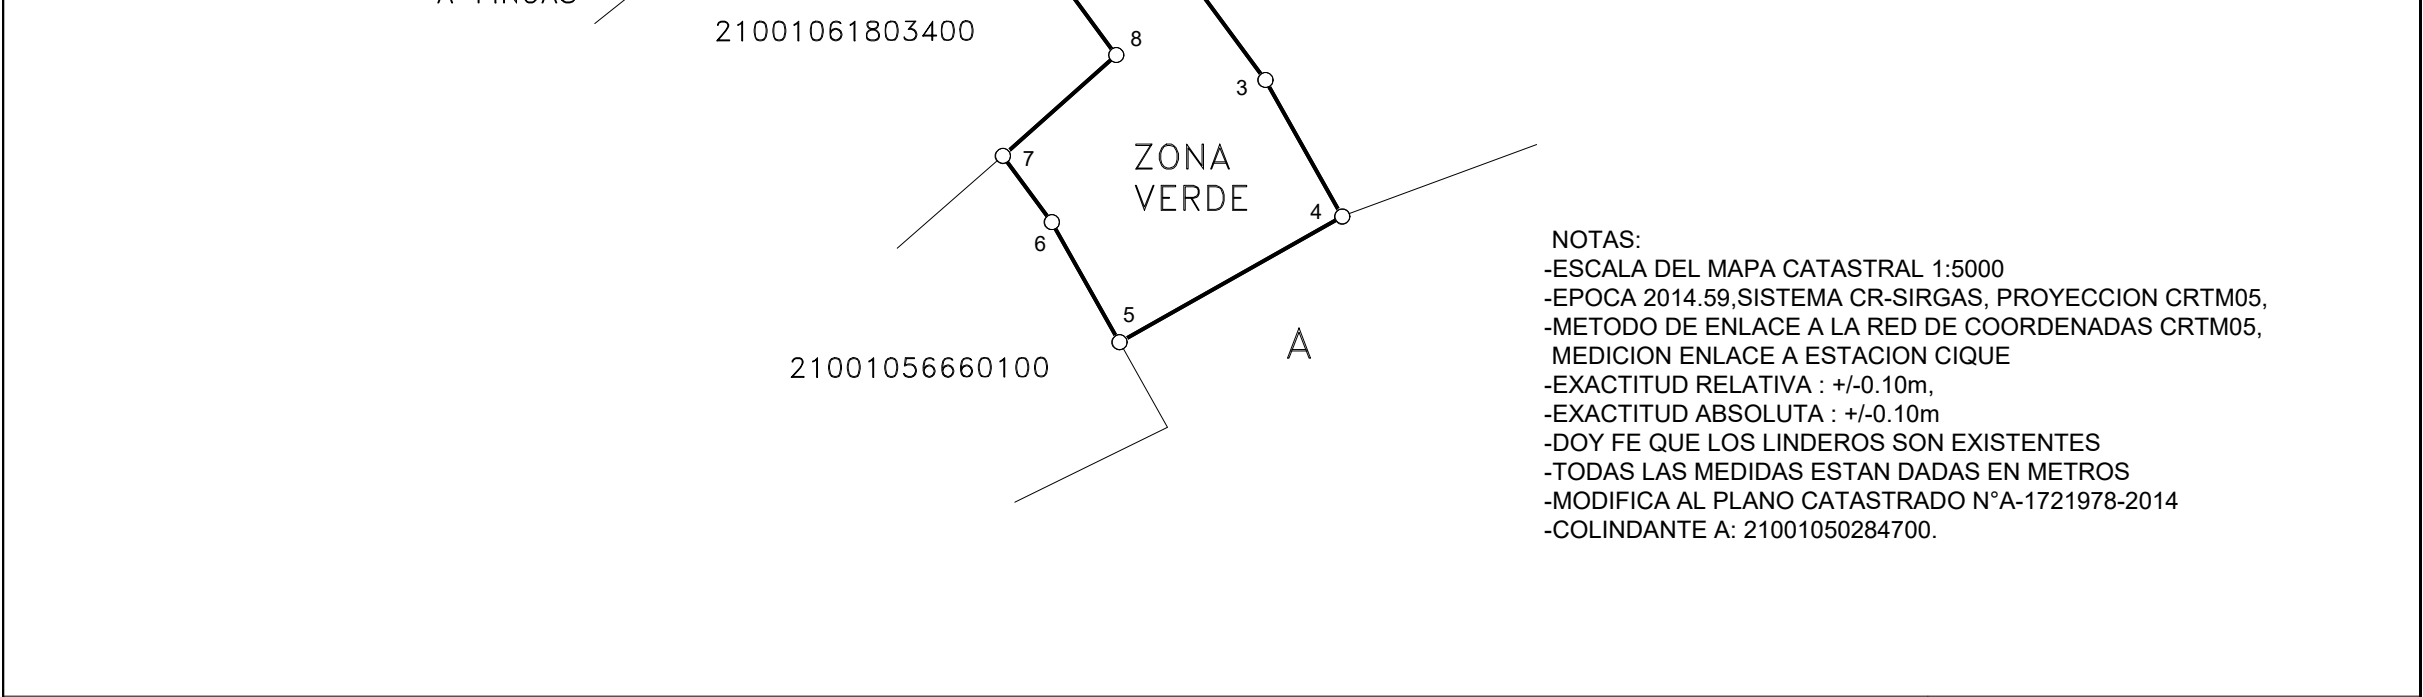

|                                                              |                                    |                        |                               |                                                  |
|--------------------------------------------------------------|------------------------------------|------------------------|-------------------------------|--------------------------------------------------|
| TOPOGRAFO ASOCIADO: T.A. 8914<br>JORGE MARIO GUERRERO VARGAS | PROTOCOLO: TOMO 24381<br>FOLIO 026 | SITUADO EN: LA LLANADA | AREA<br>1810.36m <sup>2</sup> | ES PARTE DE<br>FOLIO REAL<br>2 502847-000        |
|                                                              | ESCALA 1:1000<br>FECHA MAYO 2026   | DISTRITO: 1° QUESADA   |                               | IDENTIFICADOR PREDIAL<br>21001050284700          |
|                                                              | CANTON: 10° SAN CARLOS             | PROVINCIA: 2° ALAJUELA |                               | AREA SEGUN REGISTRO<br>34ha1697.65m <sup>2</sup> |

---