


ENTERO N°
XXXXXXXXXX

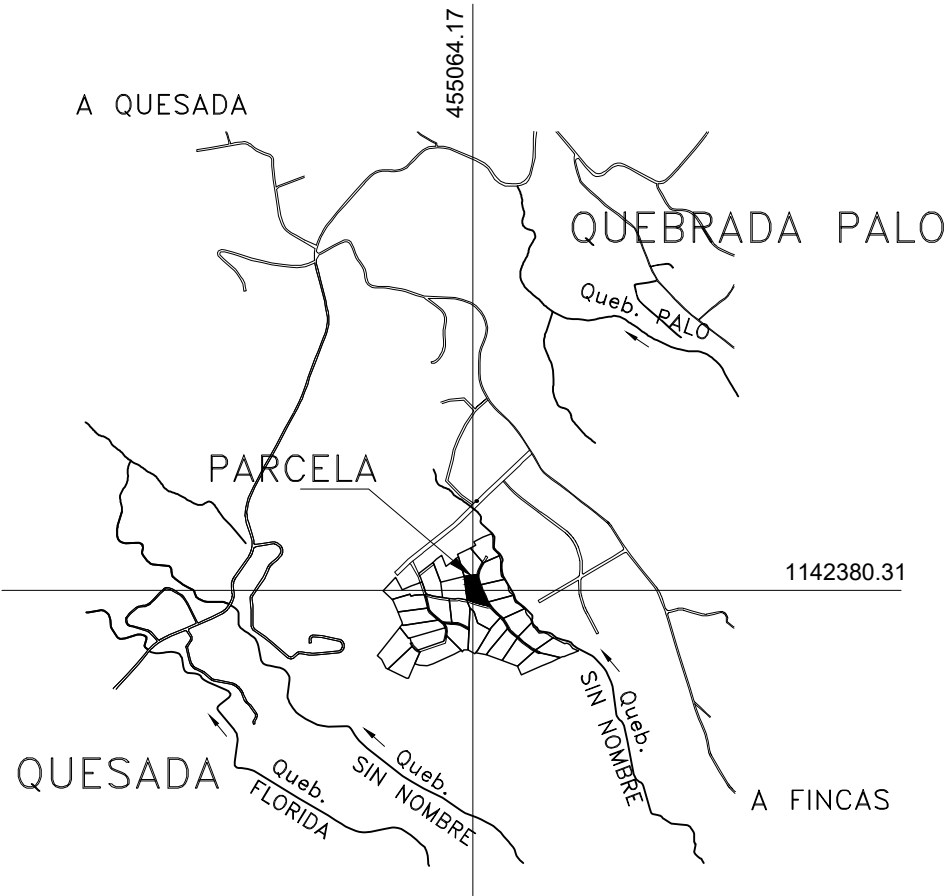


LISTADO DE COORDENADAS		
PUNTO	ESTE (m)	NORTE (m)
1	455071.89	1142432.59
2	455075.35	1142433.04
3	455075.35	1142423.12
4	455076.82	1142415.38
5	455082.03	1142398.94
6	455089.72	1142378.39
7	455093.35	1142369.63
8	455098.21	1142359.48
9	455104.31	1142347.04
10	455106.89	1142342.18
11	455109.81	1142336.71
12	455113.98	1142330.15
13	455110.09	1142329.75
14	455107.07	1142329.44
15	455090.31	1142333.53
16	455063.05	1142341.02
17	455049.96	1142345.47
18	455037.78	1142348.34
19	455028.96	1142427.00

UBICACION GEOGRAFICA

HOJA QUESADA – AGUAS ZARCAS
ESCALA: 1:50,000
AMPLIADA: 1:25,000
EPOCA 2014.59, SISTEMA CR–SIRGAS,
PROYECCION CRTM05

REFERENCIAS		
PUNTO	ESTE	NORTE
P.I	455249.98	1142829.35
XX	454903.46	1142362.01
ZZ	454848.44	1142468.90

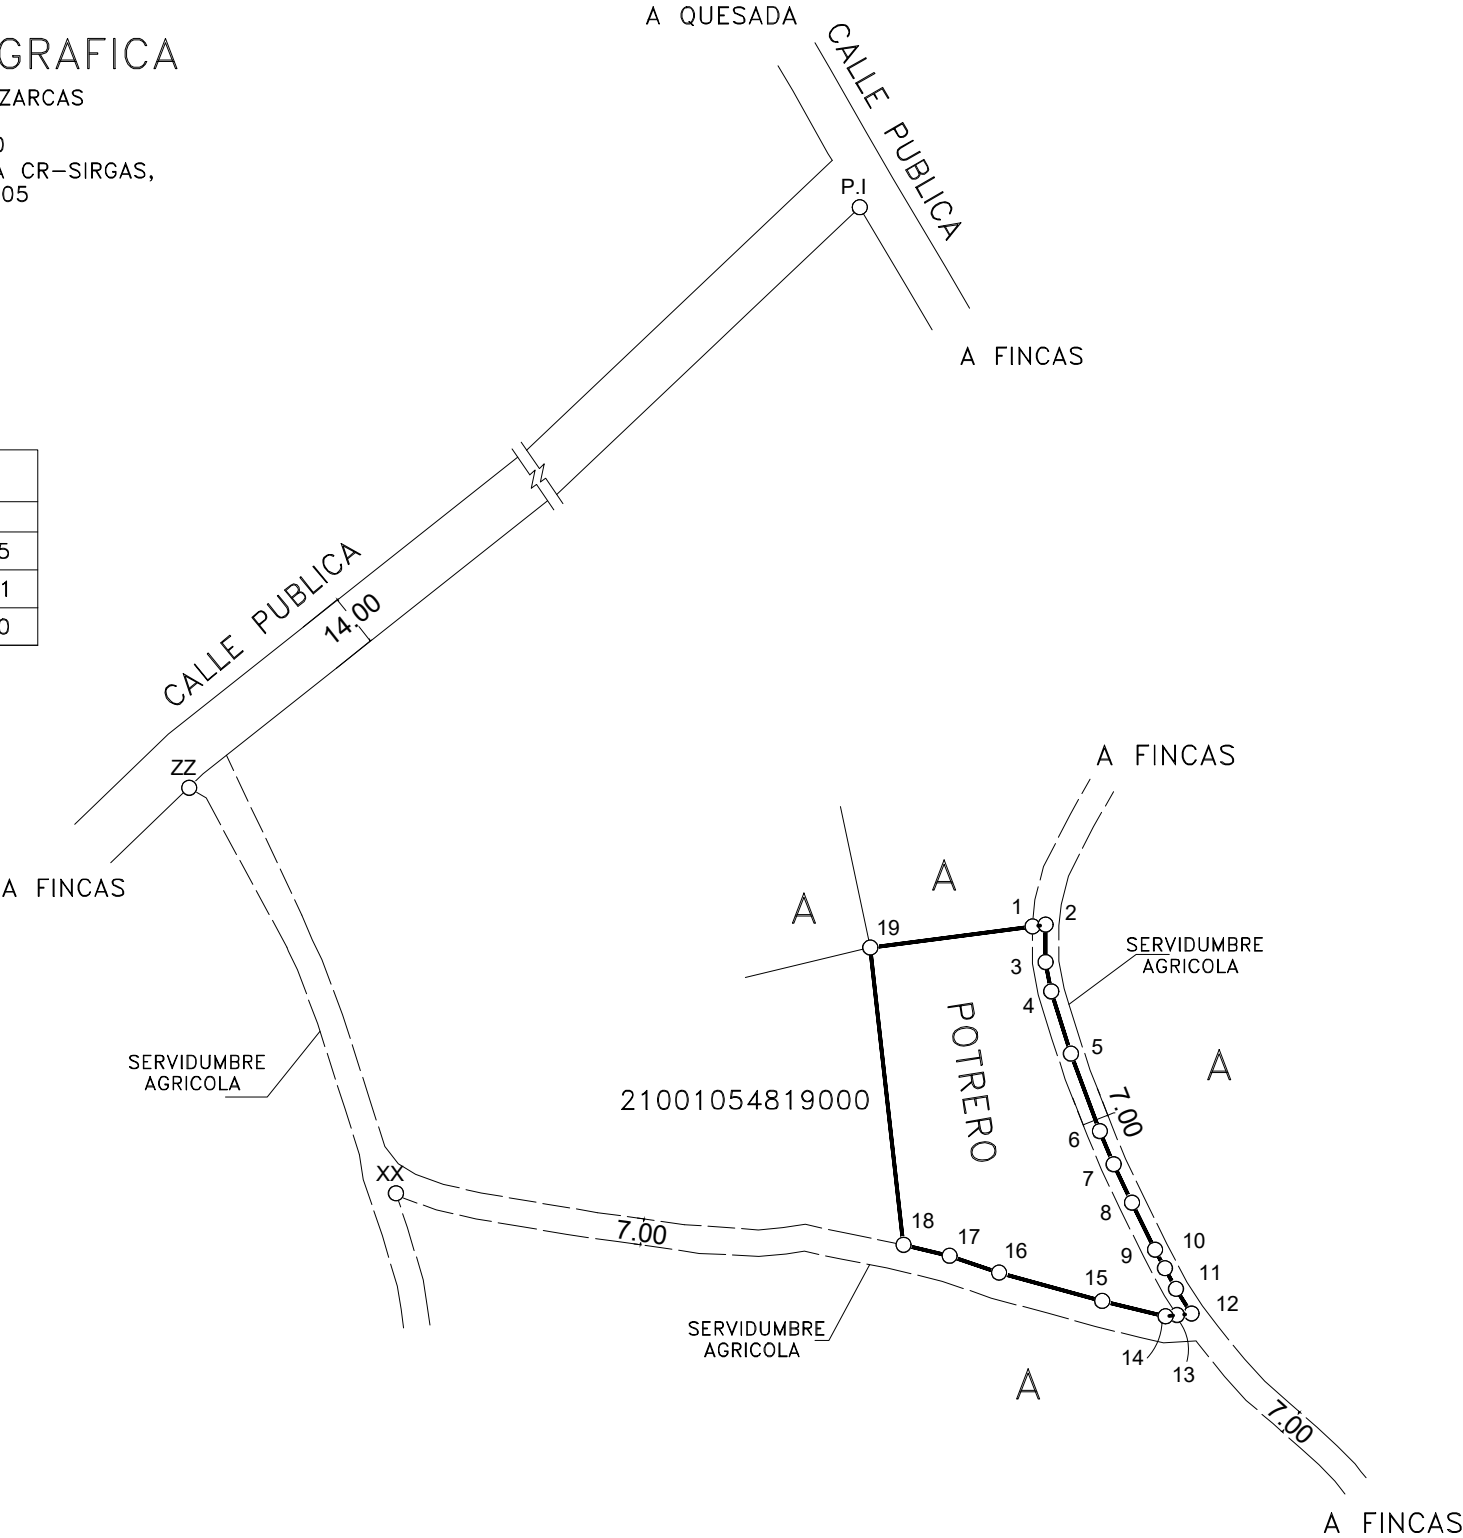

NOTAS:
-ESCALA DEL MAPA CATASTRAL 1:5000
-EPOCA 2014.59,SISTEMA CR-SIRGAS, PROYECCION CRTM05,
-METODO DE ENLACE A LA RED DE COORDENADAS CRTM05,
MEDICION ENLACE A ESTACION CIQUE
-EXACTITUD RELATIVA : +/-0.10m,
-EXACTITUD ABSOLUTA : +/-0.10m
-DOY FE QUE LOS LINDEROS SON EXISTENTES
-TODAS LAS MEDIDAS ESTAN DADAS EN METROS
-MODIFICA AL PLANO CATASTRADO N°A-1630235-2013
-FRENTE A SERVIDUMBRE AGRICOLA DE VERTICE 1 AL 18: 193.31m
-PARCELA EXCLUSIVAMENTE PARA USO AGRICOLA
-LOS PUNTOS XX Y ZZ SON VERTICES DE LA SERVIDUMBRE
-COLINDANTE A: 21001050284700.

PROTOCOLO: TOMO 24381
FOLIO 026

ESCALA 1:2000
FECHA MAYO 2026

SITUADO EN: LA LLANADA

DISTRITO: 1° QUESADA

CANTON: 10° SAN CARLOS

PROVINCIA: 2° ALAJUELA

PARCELA 15

AREA

5063.72m²

ES PARTE DE
FOLIO REAL

2 502847–000

IDENTIFICADOR PREDIAL
21001050284700

AREA SEGUN REGISTRO
34ha1697.65m²

TOPOGRAFO ASOCIADO: T.A. 8914
JORGE MARIO GUERRERO VARGAS