


ENTERO N°
XXXXXXXXXX



LISTADO DE COORDENADAS		
PUNTO	ESTE (m)	NORTE (m)
1	455085.46	1142399.71
2	455082.03	1142398.94
3	455076.82	1142415.38
4	455075.35	1142423.12
5	455075.35	1142433.04
6	455076.01	1142439.02
7	455078.10	1142447.19
8	455084.96	1142460.66
9	455091.32	1142471.76
10	455097.02	1142474.24
11	455145.44	1142495.35
12	455149.59	1142481.18
13	455149.57	1142463.72
14	455149.59	1142447.15
15	455150.57	1142432.86
16	455153.46	1142426.30
17	455162.33	1142417.01

UBICACION GEOGRAFICA
HOJA QUESADA – AGUAS ZARCAS
ESCALA: 1:50,000
AMPLIADA: 1:25,000
EPOCA 2014.59, SISTEMA CR–SIRGAS,
PROYECCION CRTM05

REFERENCIAS		
PUNTO	ESTE	NORTE
P.I	455249.98	1142829.35
XX	454903.46	1142362.01
ZZ	454848.44	1142468.90

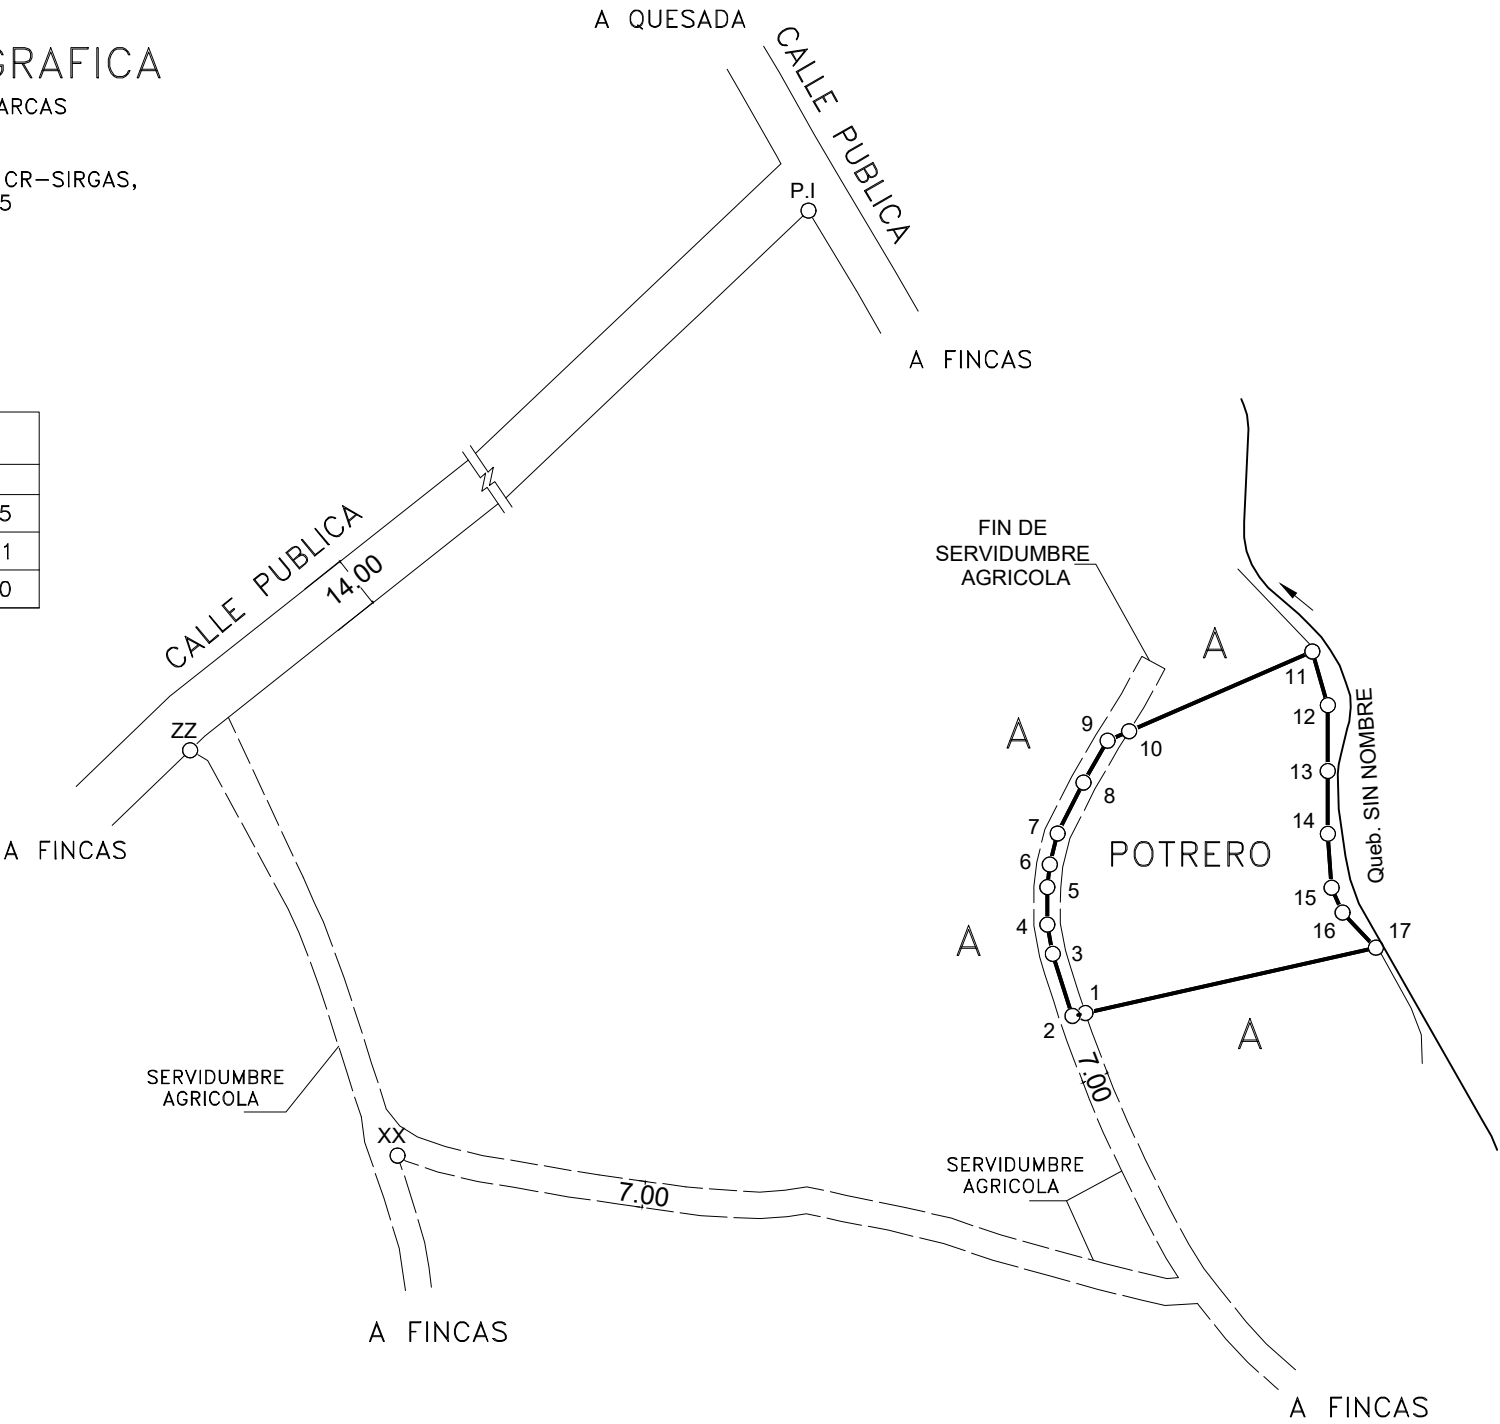

NOTAS:
-ESCALA DEL MAPA CATASTRAL 1:5000
-EPOCA 2014.59,SISTEMA CR-SIRGAS, PROYECCION CRTM05,
-METODO DE ENLACE A LA RED DE COORDENADAS CRTM05,
MEDICION ENLACE A ESTACION CIQUE
-EXACTITUD RELATIVA : +/-0.10m,
-EXACTITUD ABSOLUTA : +/-0.10m
-DOY FE QUE LOS LINDEROS SON EXISTENTES
-TODAS LAS MEDIDAS ESTAN DADAS EN METROS
-MODIFICA AL PLANO CATASTRADO N°A-1630235-2013
-AFECTADO POR LEY FORESTAL 7575, ARTICULO 33
-FRENTE A SERVIDUMBRE AGRICOLA DE VERTICE 1 AL 10: 87.12m
-PARCELA EXCLUSIVAMENTE PARA USO AGRICOLA
-LOS PUNTOS XX Y ZZ SON VERTICES DE LA SERVIDUMBRE
-COLINDANTE A: 21001050284700.

PROTOCOLO: TOMO 24381
FOLIO 026

ESCALA 1:2000
FECHA MAYO 2026

SITUADO EN: LA LLANADA
DISTRITO: 1° QUESADA
CANTON: 10° SAN CARLOS
PROVINCIA: 2° ALAJUELA

PARCELA 16

AREA
5403.38m²

ES PARTE DE
FOLIO REAL
2 502847–000
IDENTIFICADOR PREDIAL
21001050284700
AREA SEGUN REGISTRO
34ha1697.65m²

TOPOGRAFO ASOCIADO: T.A. 8914
JORGE MARIO GUERRERO VARGAS