


ENTERO N°
XXXXXXXXXX

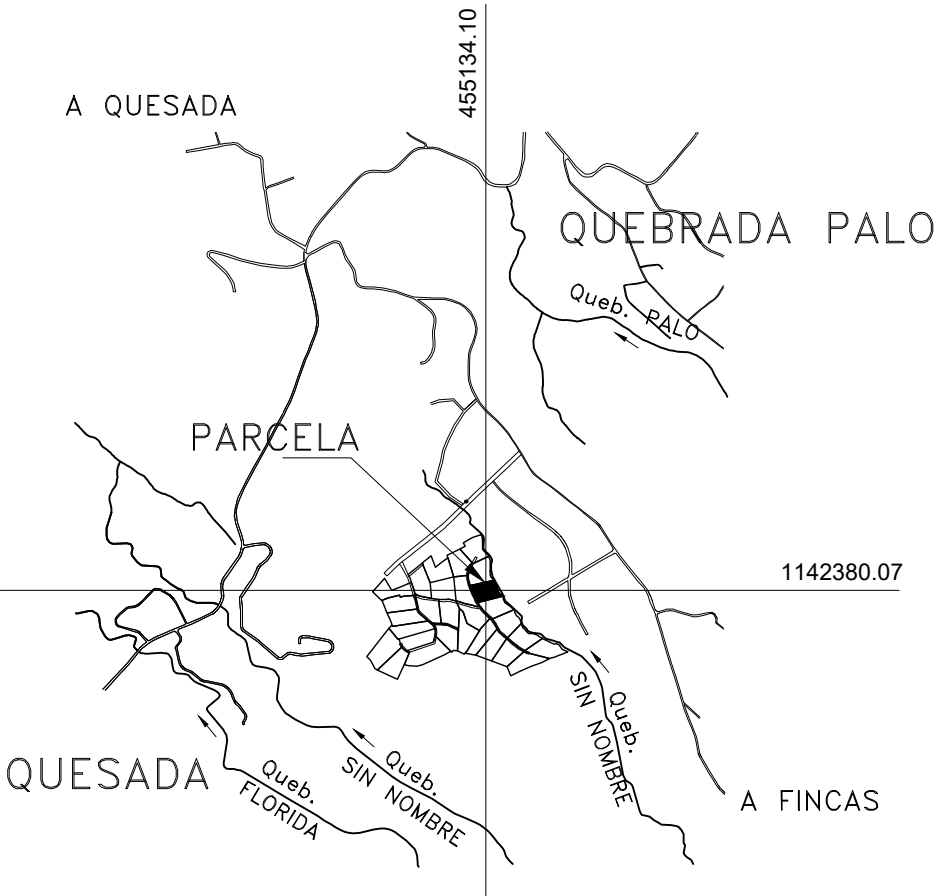


LISTADO DE COORDENADAS		
PUNTO	ESTE (m)	NORTE (m)
1	455110.38	1142343.09
2	455106.89	1142342.18
3	455104.31	1142347.04
4	455093.35	1142369.63
5	455089.72	1142378.39
6	455082.03	1142398.94
7	455085.46	1142399.71
8	455162.33	1142417.01
9	455171.61	1142400.99
10	455174.35	1142394.02
11	455174.63	1142386.43
12	455176.82	1142379.72
13	455179.81	1142374.41
14	455187.41	1142367.91
15	455192.95	1142364.47

UBICACION GEOGRAFICA

HOJA QUESADA – AGUAS ZARCAS
ESCALA: 1:50,000
AMPLIADA: 1:25,000
EPOCA 2014.59, SISTEMA CR–SIRGAS,
PROYECCION CRTM05

REFERENCIAS		
PUNTO	ESTE	NORTE
P.I	455249.98	1142829.35
XX	454903.46	1142362.01
ZZ	454848.44	1142468.90

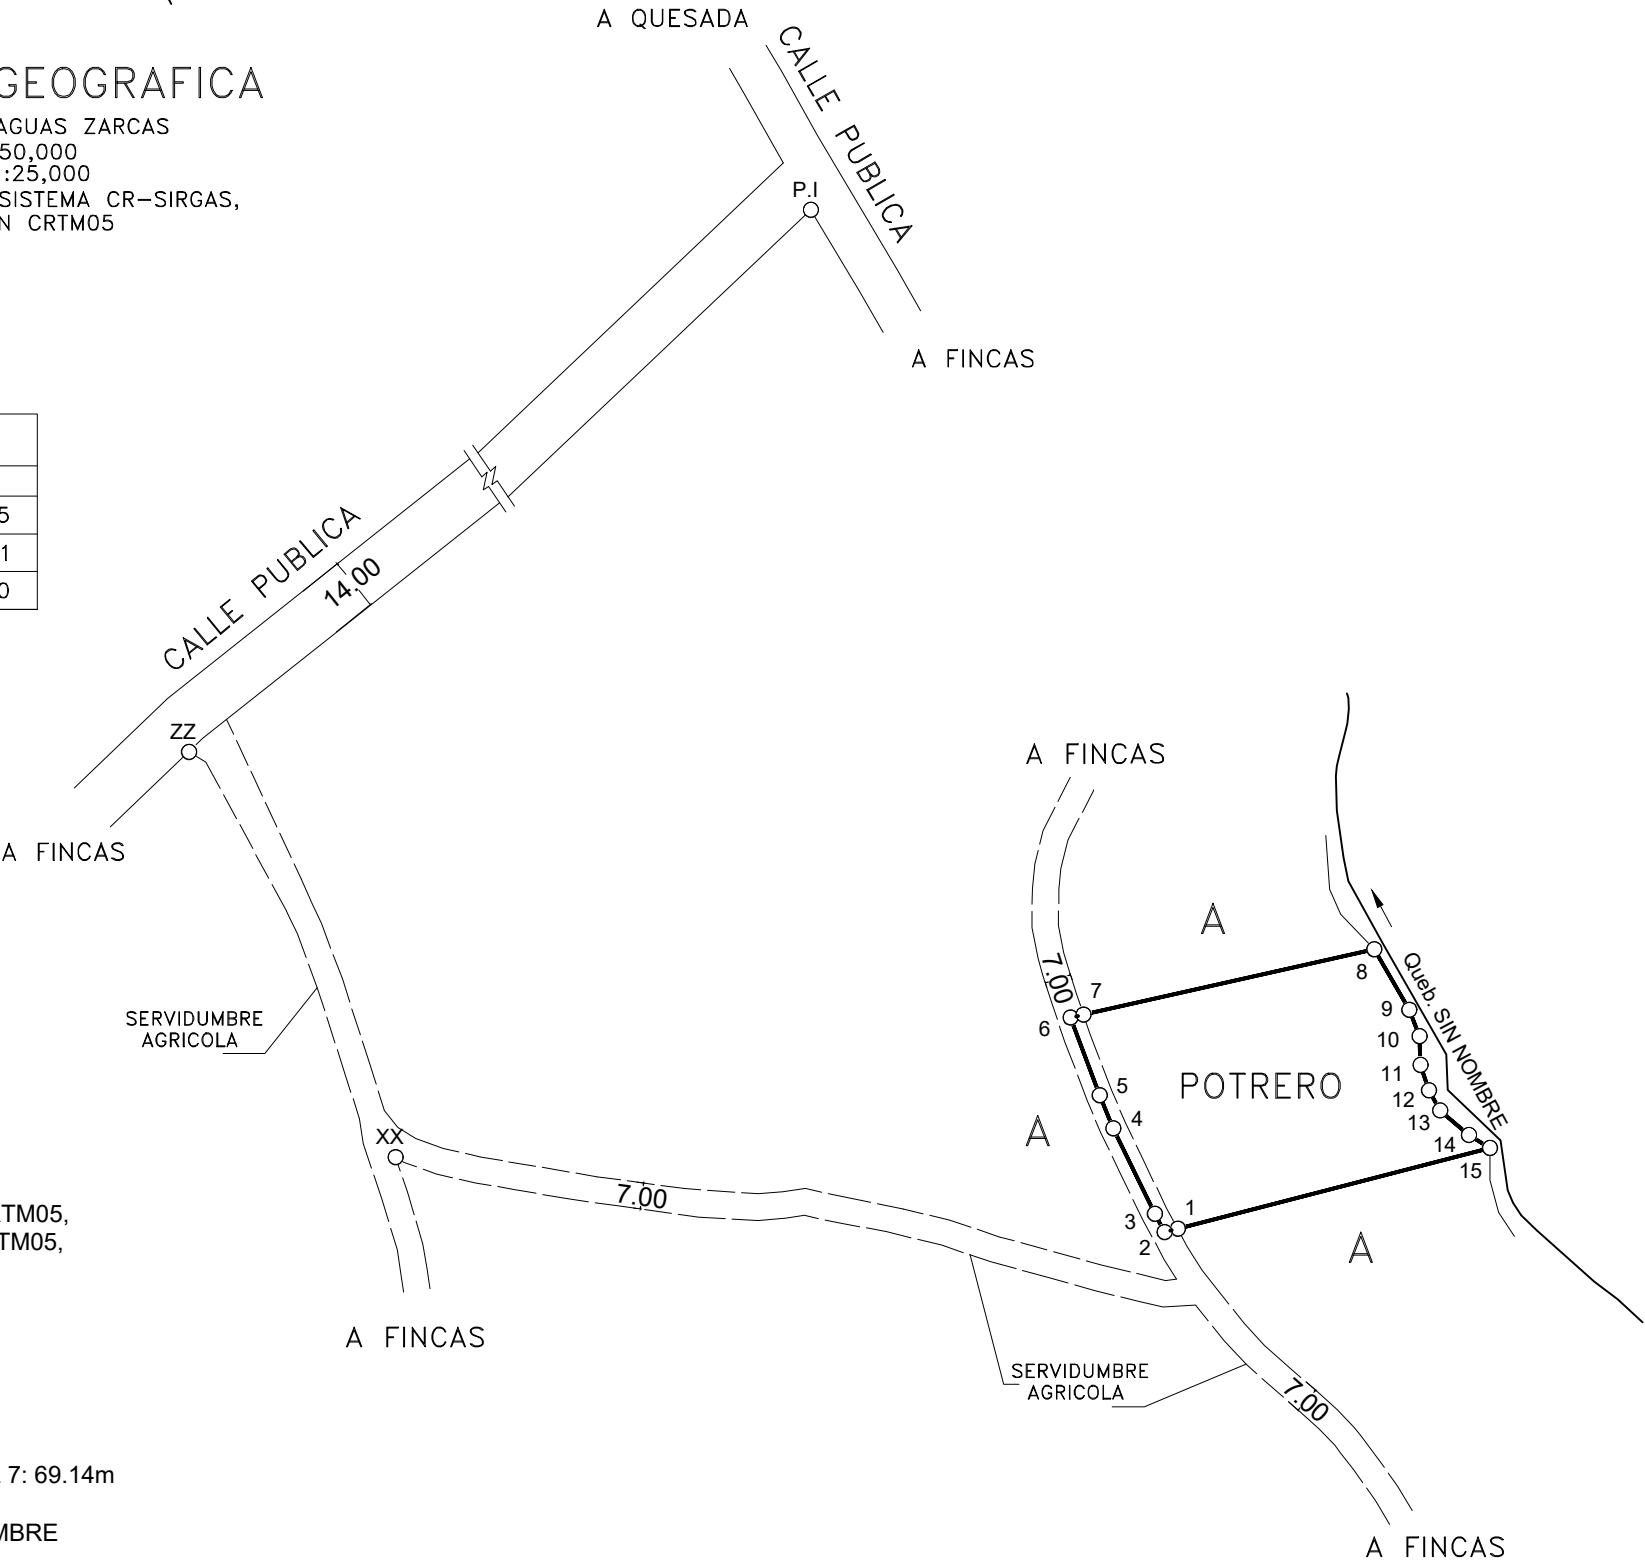

NOTAS:
-ESCALA DEL MAPA CATASTRAL 1:5000
-EPOCA 2014.59,SISTEMA CR-SIRGAS, PROYECCION CRTM05,
-METODO DE ENLACE A LA RED DE COORDENADAS CRTM05,
MEDICION ENLACE A ESTACION CIQUE
-EXACTITUD RELATIVA : +/-0.10m,
-EXACTITUD ABSOLUTA : +/-0.10m
-DOY FE QUE LOS LINDEROS SON EXISTENTES
-TODAS LAS MEDIDAS ESTAN DADAS EN METROS
-MODIFICA AL PLANO CATASTRADO N°A-1630235-2013
-AFECTADO POR LEY FORESTAL 7575, ARTICULO 33
- FRENTE A SERVIDUMBRE AGRICOLA DE VERTICE 1 AL 7: 69.14m
-PARCELA EXCLUSIVAMENTE PARA USO AGRICOLA
- LOS PUNTOS XX Y ZZ SON VERTICES DE LA SERVIDUMBRE
-COLINDANTE A: 21001050284700.

PROTOCOLO: TOMO 24381
FOLIO 026

ESCALA 1:2000
FECHA MAYO 2026

SITUADO EN: LA LLANADA
DISTRITO: 1° QUESADA
CANTON: 10° SAN CARLOS
PROVINCIA: 2° ALAJUELA

PARCELA 17

AREA
5000.00m²

ES PARTE DE
FOLIO REAL
2 502847–000
IDENTIFICADOR PREDIAL
21001050284700
AREA SEGUN REGISTRO
34ha1697.65m²

TOPOGRAFO ASOCIADO: T.A. 8914
JORGE MARIO GUERRERO VARGAS