



ENTERO N°
XXXXXXXXXX

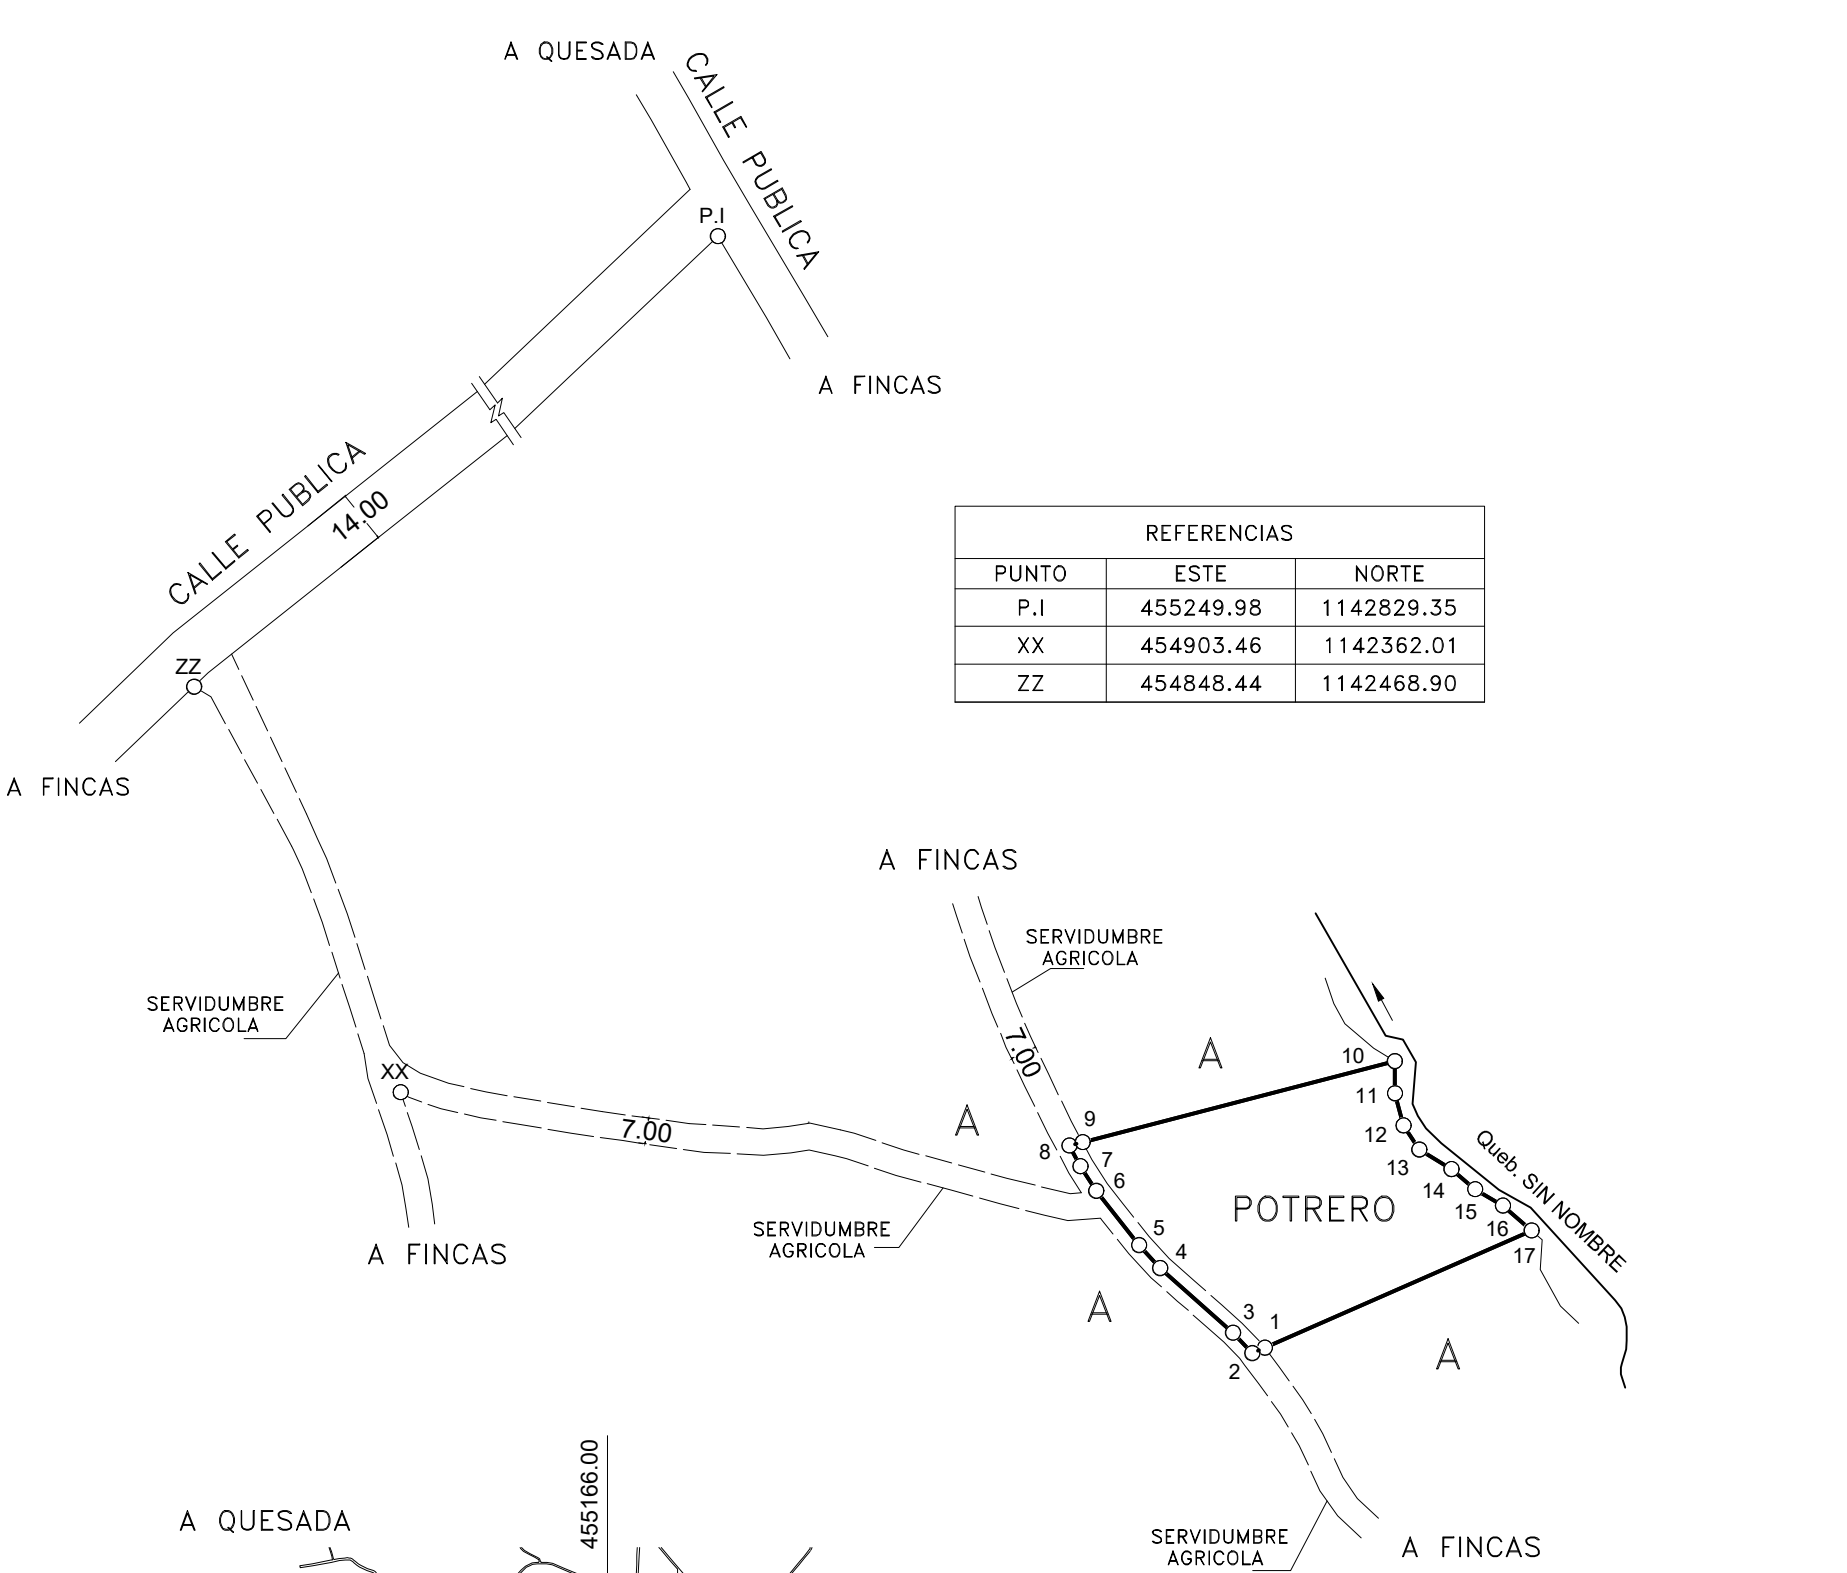

REFERENCIAS		
PUNTO	ESTE	NORTE
P.I	455249.98	1142829.35
XX	454903.46	1142362.01
ZZ	454848.44	1142468.90

LISTADO DE COORDENADAS		
PUNTO	ESTE (m)	NORTE (m)
1	455158.62	1142288.69
2	455155.27	1142287.22
3	455150.16	1142292.68
4	455130.89	1142309.75
5	455125.33	1142315.80
6	455113.98	1142330.15
7	455109.81	1142336.71
8	455106.89	1142342.18
9	455110.38	1142343.09
10	455192.95	1142364.47
11	455193.04	1142355.98
12	455195.28	1142347.49
13	455199.45	1142341.07
14	455207.96	1142335.92
15	455214.24	1142330.64
16	455221.59	1142326.29
17	455229.15	1142319.72

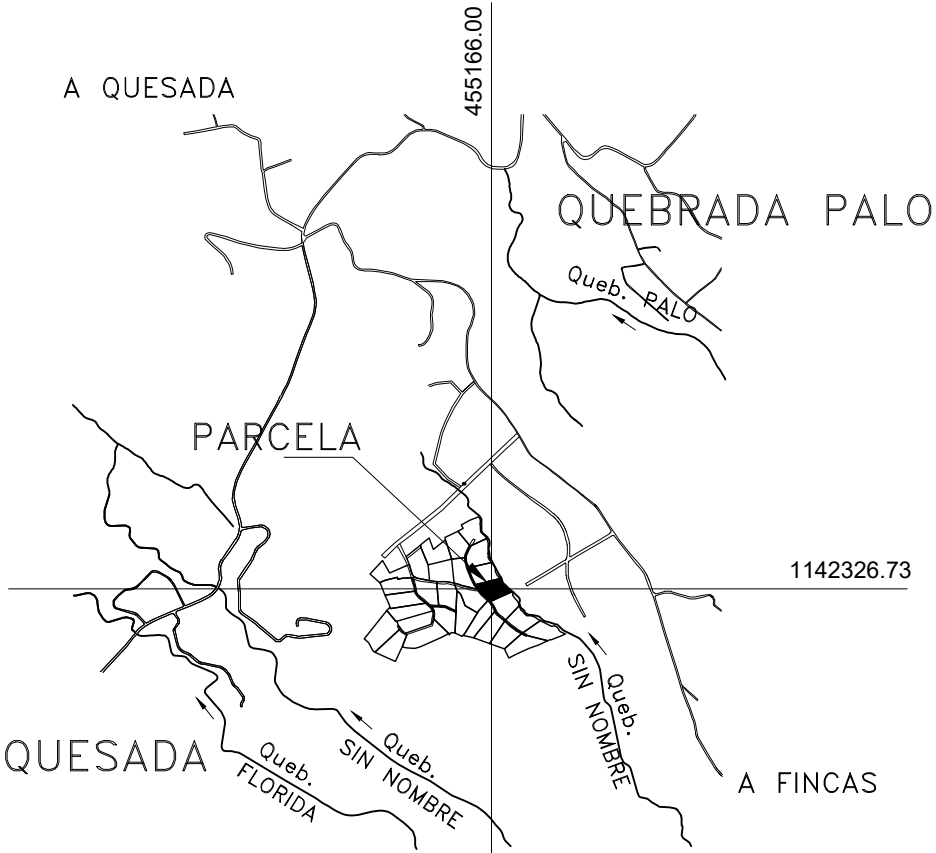

UBICACION GEOGRAFICA
HOJA QUESADA – AGUAS ZARCAS
ESCALA: 1:50,000
AMPLIADA: 1:25,000
EPOCA 2014.59, SISTEMA CR–SIRGAS,
PROYECCION CRTM05

NOTAS:
-ESCALA DEL MAPA CATASTRAL 1:5000
-EPOCA 2014.59, SISTEMA CR-SIRGAS, PROYECCION CRTM05,
-METODO DE ENLACE A LA RED DE COORDENADAS CRTM05,
MEDICION ENLACE A ESTACION CIQUE
-EXACTITUD RELATIVA : +/-0.10m,
-EXACTITUD ABSOLUTA : +/-0.10m
-DOY FE QUE LOS LINDEROS SON EXISTENTES
-TODAS LAS MEDIDAS ESTAN DADAS EN METROS
-MODIFICA AL PLANO CATASTRADO N°A-1630235-2013
-AFECTADO POR LEY FORESTAL 7575, ARTICULO 33
- FRENTE A SERVIDUMBRE AGRICOLA DE VERTICE 1 AL 9: 80.97m
-PARCELA EXCLUSIVAMENTE PARA USO AGRICOLA
- LOS PUNTOS XX Y ZZ SON VERTICES DE LA SERVIDUMBRE
-COLINDANTE A: 21001050284700.

PROTOCOLO: TOMO 24381
FOLIO 026

ESCALA 1:2000
FECHA MAYO 2026

SITUADO EN: LA LLANADA
DISTRITO: 1° QUESADA
CANTON: 10° SAN CARLOS
PROVINCIA: 2° ALAJUELA

PARCELA 18

AREA
5000.00m²

ES PARTE DE
FOLIO REAL
2 502847–000
IDENTIFICADOR PREDIAL
21001050284700
AREA SEGUN REGISTRO
34ha1697.65m²

TOPOGRAFO ASOCIADO: T.A. 8914
JORGE MARIO GUERRERO VARGAS