


ENTERO N°  
XXXXXXXXXX

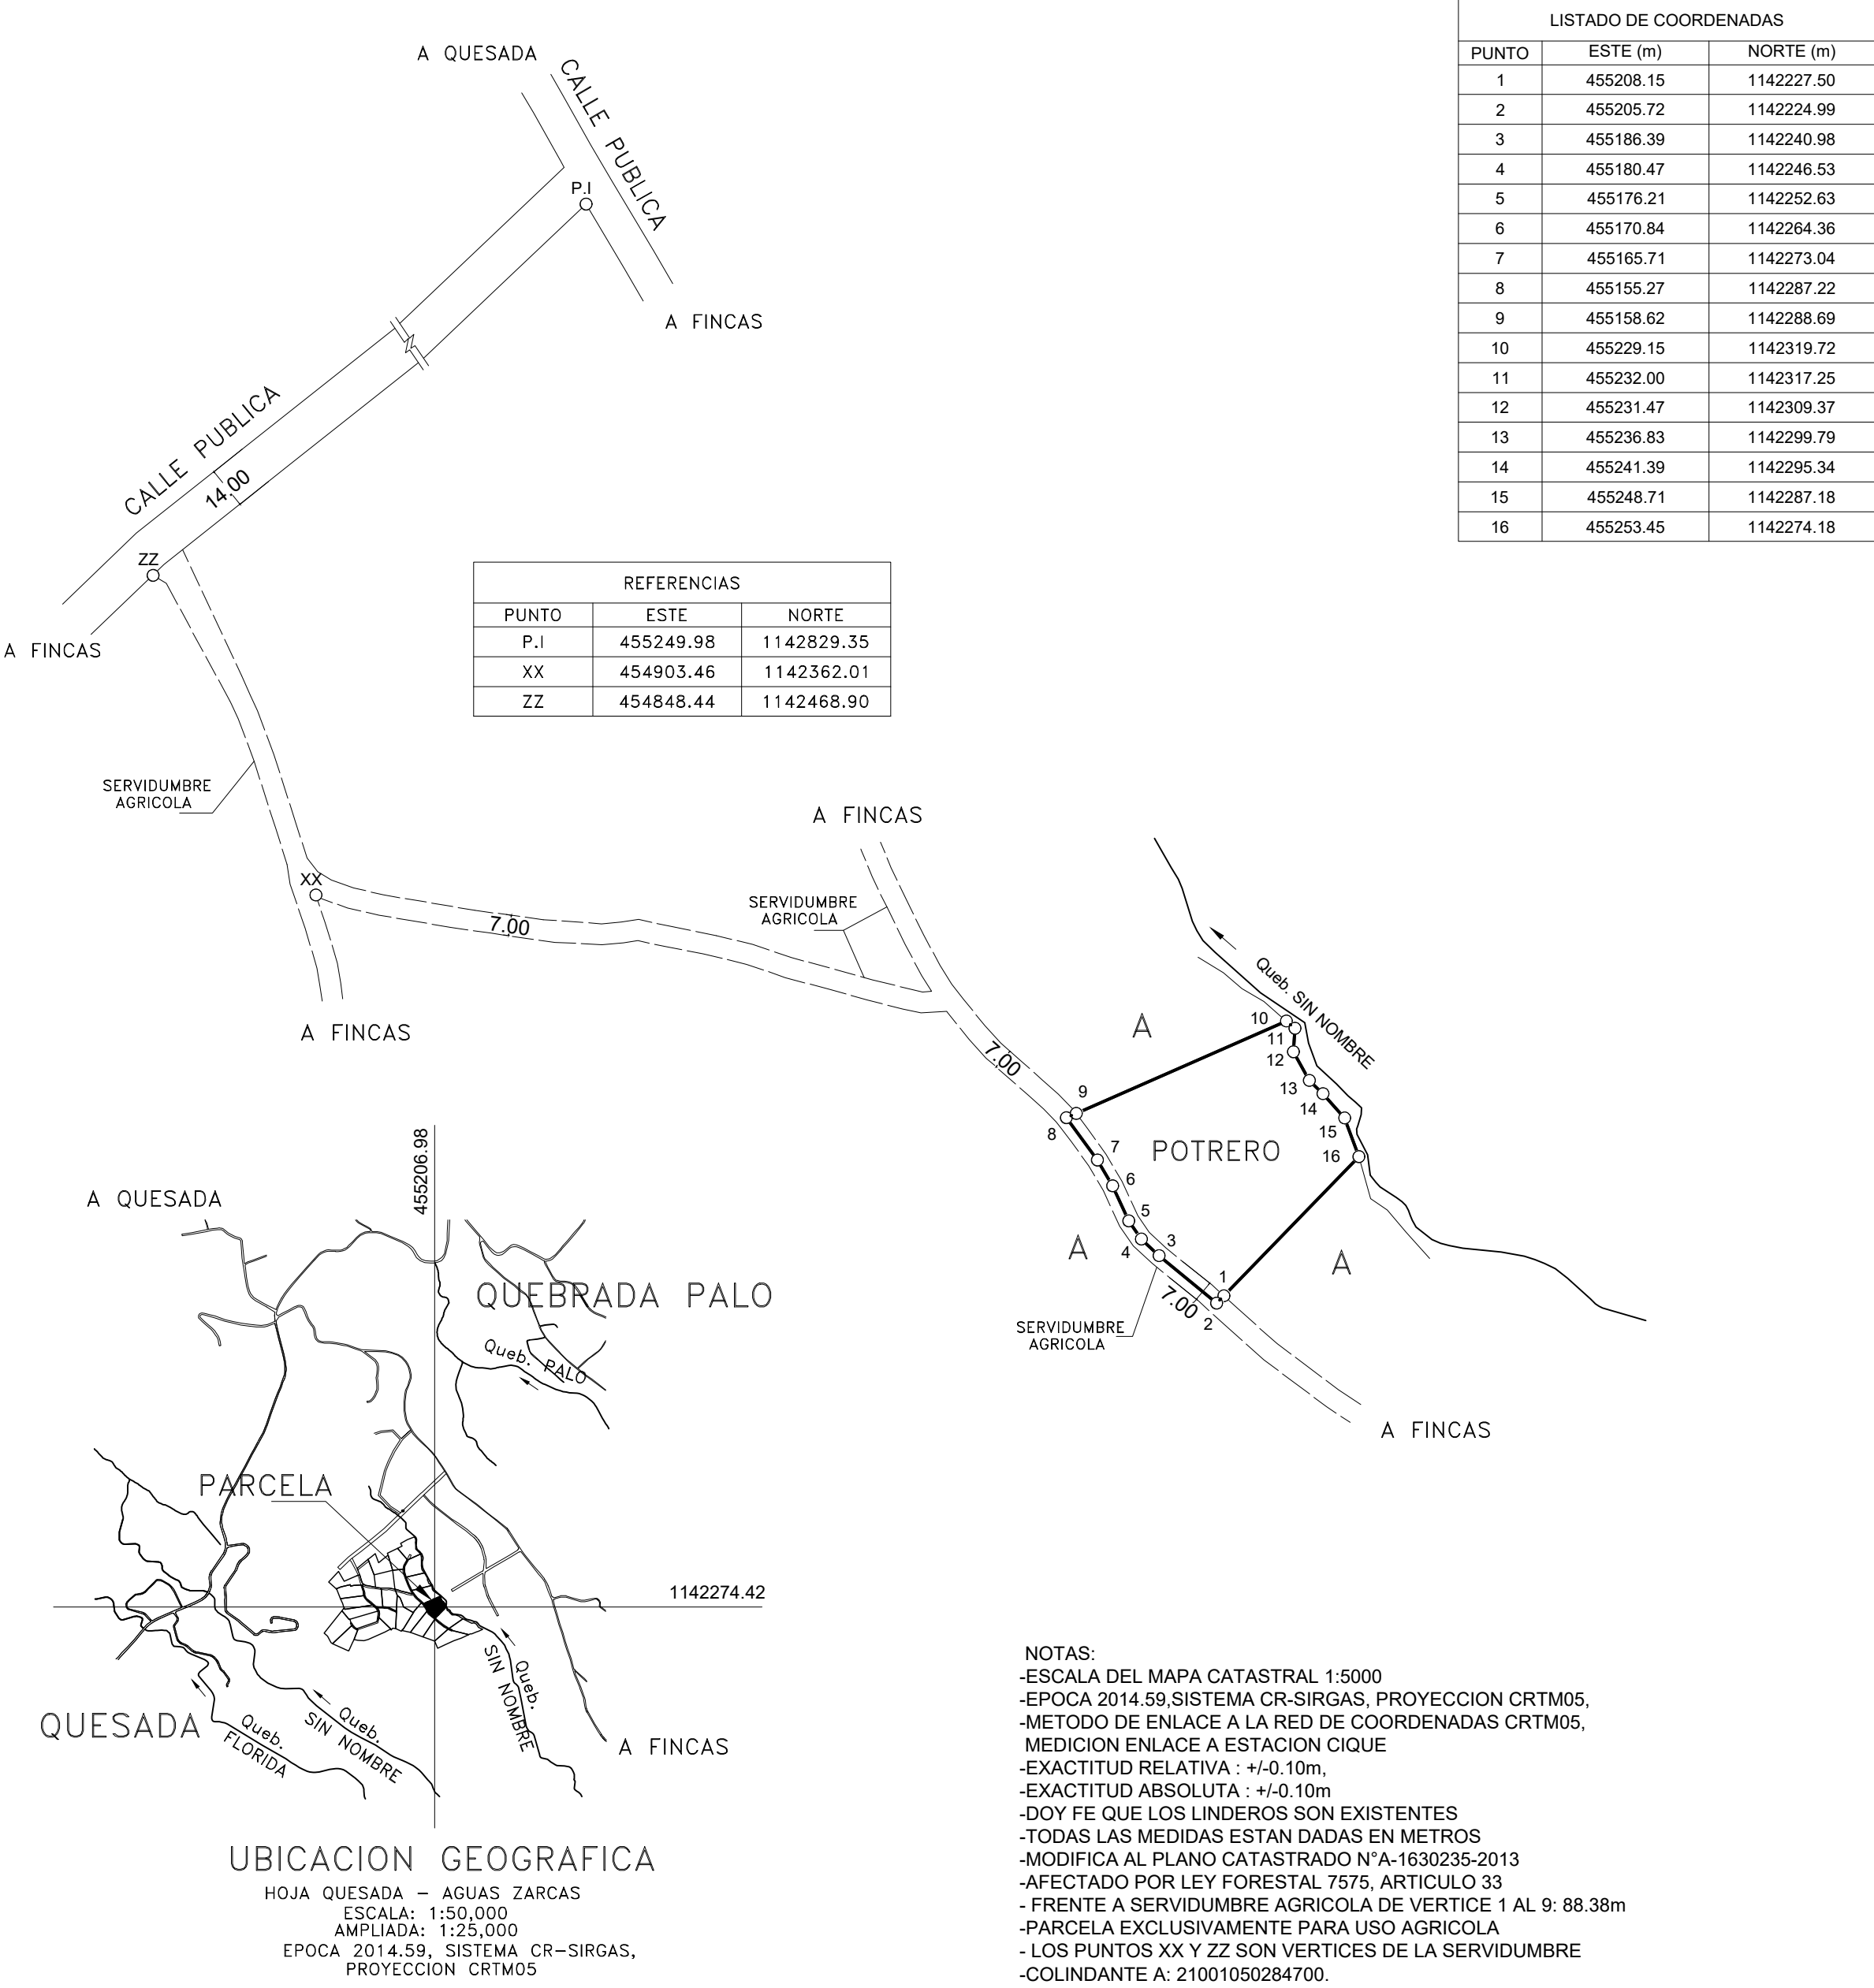

PROTOCOLO: TOMO 24381  
FOLIO 026

ESCALA 1:2000  
FECHA MAYO 2026

SITUADO EN: LA LLANADA

DISTRITO: 1° QUESADA

CANTON: 10° SAN CARLOS

PROVINCIA: 2° ALAJUELA

PARCELA 19

AREA

5000.00m<sup>2</sup>

ES PARTE DE  
FOLIO REAL

2 502847–000

IDENTIFICADOR PREDIAL  
21001050284700

AREA SEGUN REGISTRO  
34ha1697.65m<sup>2</sup>

TOPOGRAFO ASOCIADO: T.A. 8914  
JORGE MARIO GUERRERO VARGAS