
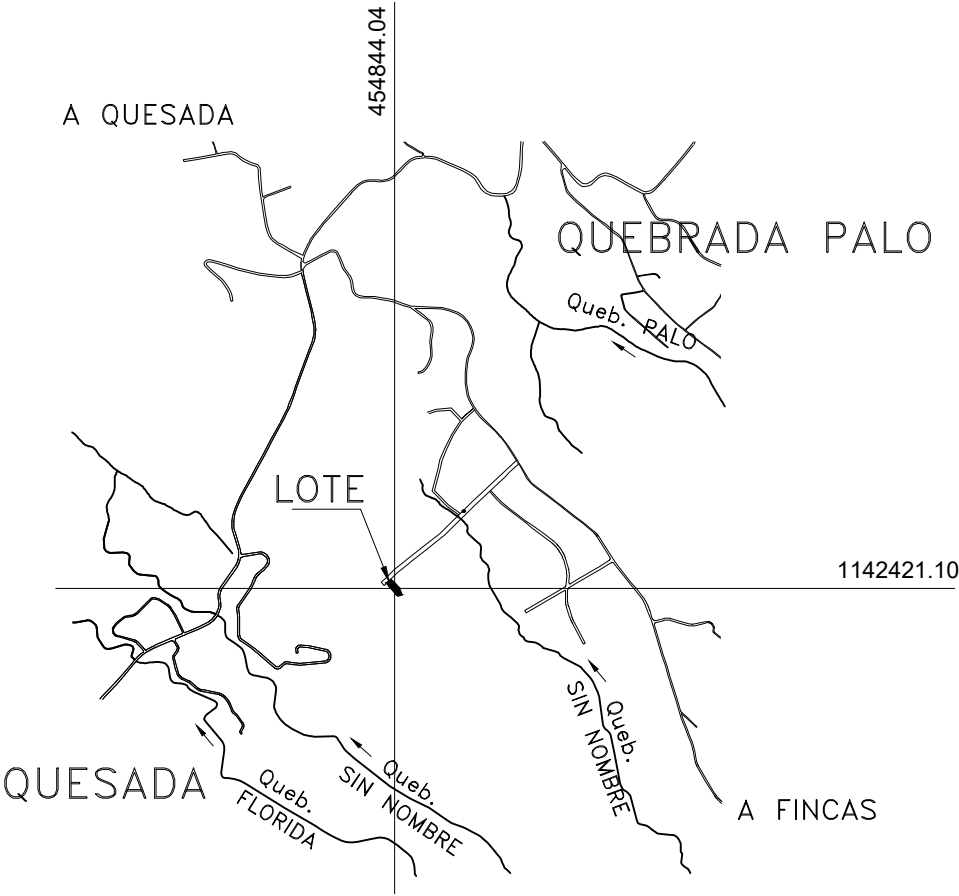


ENTERO N°
XXXXXXXXXX

NOTAS:
-ESCALA DEL MAPA CATASTRAL 1:5000
-EPOCA 2014.59,SISTEMA CR-SIRGAS, PROYECCION CRTM05,
-METODO DE ENLACE A LA RED CR-SIRGAS, MEDICION NTRIP CON EQUIPO GNSS.
ENLACE A ESTACION CIQE
-EXACTITUD RELATIVA : +/-0.10m,
-EXACTITUD ABSOLUTA : +/-0.10m
-DOY FE QUE LOS LINDEROS SON EXISTENTES
-TODAS LAS MEDIDAS ESTAN DADAS EN METROS
-MODIFICA AL PLANO CATASTRADO N°A-1630235-2013
-COLINDANTE A: 21001050284700

LISTADO DE COORDENADAS		
PUNTO	ESTE (m)	NORTE (m)
1	454815.32	1142436.93
2	454829.91	1142451.01
3	454858.80	1142421.45
4	454867.36	1142400.10
5	454853.42	1142394.36

REFERENCIAS		
PUNTO	ESTE	NORTE
P.I	455249.98	1142829.35

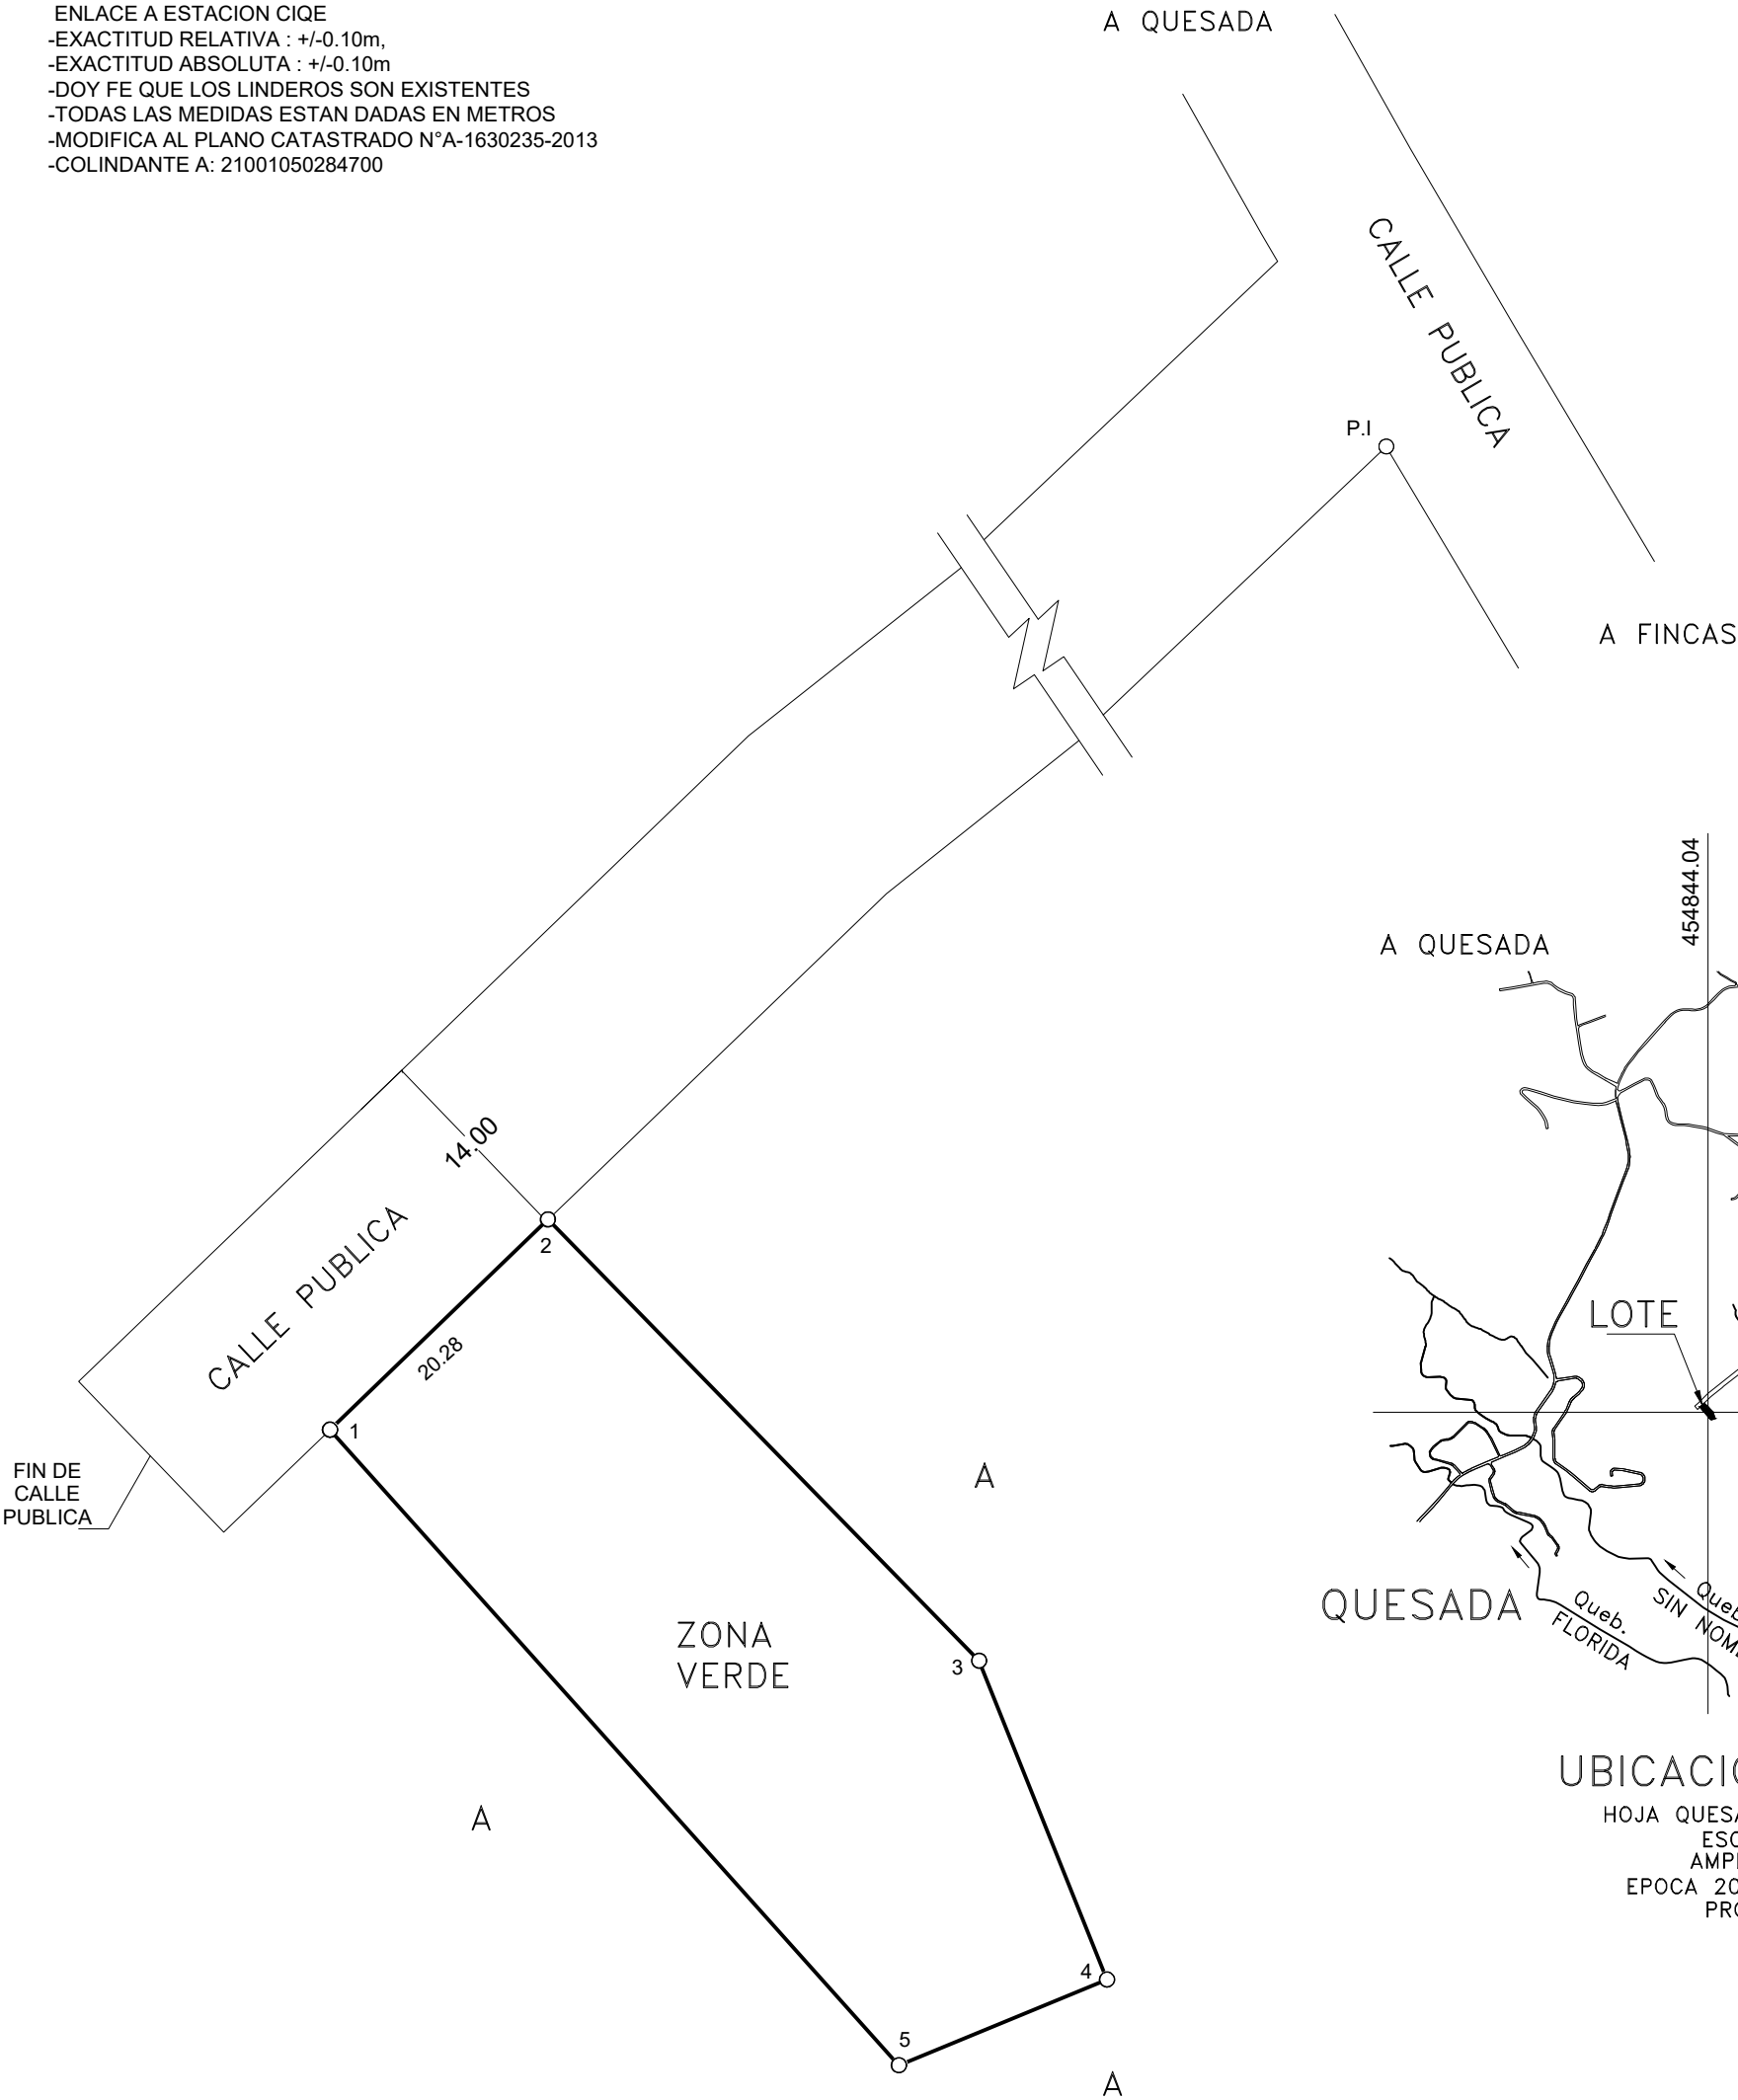

UBICACION GEOGRAFICA
HOJA QUESADA – AGUAS ZARCAS
ESCALA: 1:50,000
AMPLIADA: 1:25,000
EPOCA 2014.59, SISTEMA CR-SIRGAS,
PROYECCION CRTM05

PROTOCOLO: TOMO 24381
FOLIO 026

ESCALA 1:500
FECHA MAYO 2026

SITUADO EN: LA LLANADA
DISTRITO: 1° QUESADA
CANTON: 10° SAN CARLOS
PROVINCIA: 2° ALAJUELA

AREA
1222.94m²

ES PARTE DE
FOLIO REAL
2 502847-000
IDENTIFICADOR PREDIAL
21001050284700
AREA SEGUN REGISTRO
34ha1697.65m²

TOPOGRAFO ASOCIADO: T.A. 8914
JORGE MARIO GUERRERO VARGAS