



ENTERO N°
XXXXXXXXXX

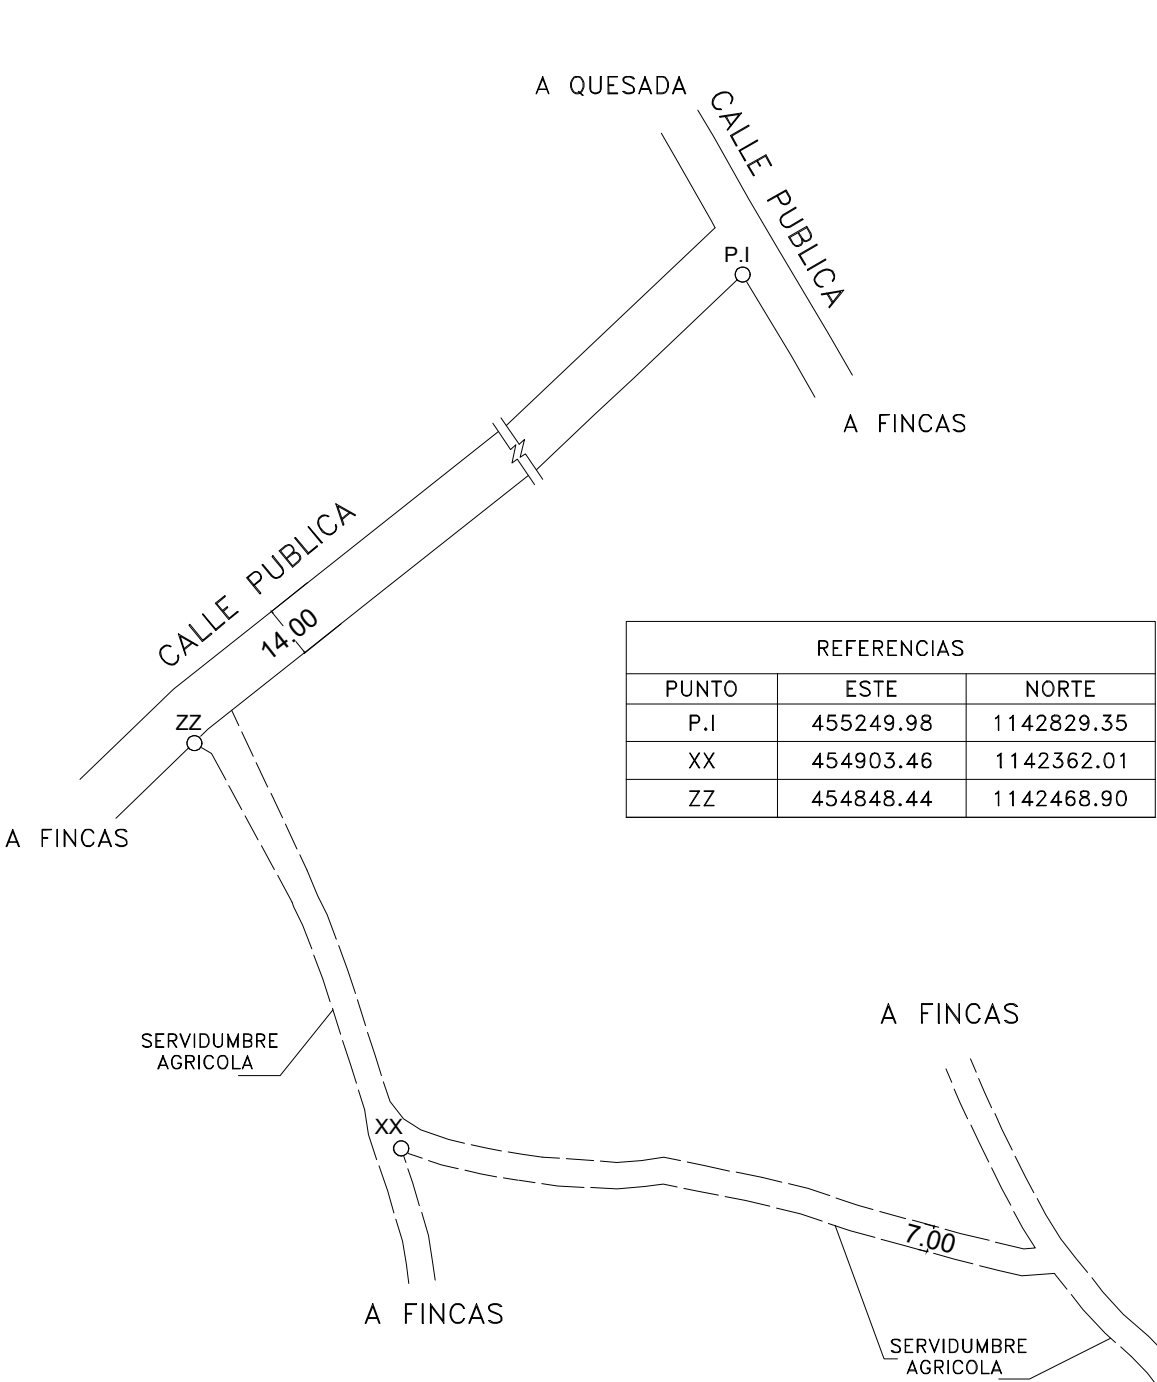

LISTADO DE COORDENADAS		
PUNTO	ESTE (m)	NORTE (m)
1	455277.81	1142174.82
2	455270.64	1142178.02
3	455263.05	1142181.95
4	455266.25	1142184.19
5	455323.30	1142224.17
6	455328.13	1142221.49
7	455360.45	1142204.92
8	455369.26	1142206.40
9	455378.41	1142201.76
10	455388.57	1142188.63
11	455406.28	1142179.81
12	455388.11	1142172.15
13	455378.70	1142168.74
14	455359.43	1142161.28
15	455354.34	1142160.75
16	455347.17	1142158.25
17	455302.14	1142169.01

NOTAS:
-ESCALA DEL MAPA CATASTRAL 1:5000
-EPOCA 2014.59,SISTEMA CR-SIRGAS, PROYECCION CRTM05,
-METODO DE ENLACE A LA RED DE COORDENADAS CRTM05,
MEDICION ENLACE A ESTACION CIQUE
-EXACTITUD RELATIVA : +/-0.10m,
-EXACTITUD ABSOLUTA : +/-0.10m
-DOY FE QUE LOS LINDEROS SON EXISTENTES
-TODAS LAS MEDIDAS ESTAN DADAS EN METROS
-MODIFICA AL PLANO CATASTRADO N°A-1630235-2013
-AFECTADO POR LEY FORESTAL 7575, ARTICULO 33
- FRENTE A SERVIDUMBRE AGRICOLA DE VERTICE 1 AL 4: 20.30m
-PARCELA EXCLUSIVAMENTE PARA USO AGRICOLA
- LOS PUNTOS XX Y ZZ SON VERTICES DE LA SERVIDUMBRE
-COLINDANTE A: 21001050284700.

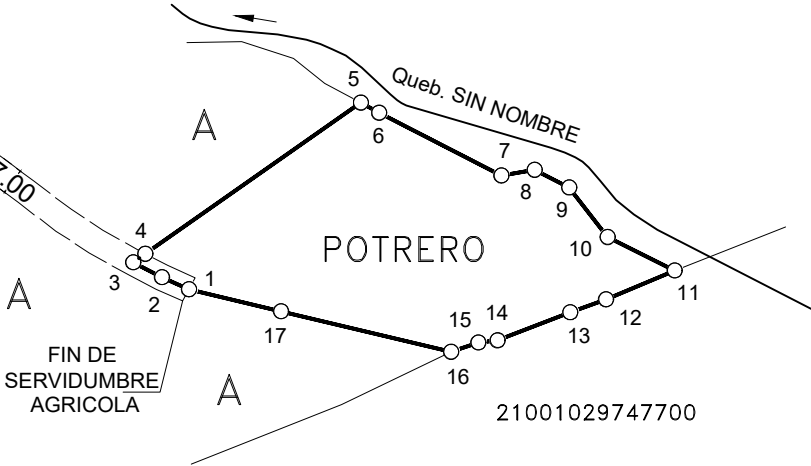

UBICACION GEOGRAFICA

HOJA QUESADA – AGUAS ZARCAS
ESCALA: 1:50,000
AMPLIADA: 1:25,000
EPOCA 2014.59, SISTEMA CR–SIRGAS,
PROYECCION CRTM05

PROTOCOLO: TOMO 24381
FOLIO 026

ESCALA 1:2000
FECHA MAYO 2026

SITUADO EN: LA LLANADA
DISTRITO: 1° QUESADA
CANTON: 10° SAN CARLOS
PROVINCIA: 2° ALAJUELA

PARCELA 21

AREA
5000.00m²

ES PARTE DE
FOLIO REAL
2 502847–000
IDENTIFICADOR PREDIAL
21001050284700
AREA SEGUN REGISTRO
34ha1697.65m²

TOPOGRAFO ASOCIADO: T.A. 8914
JORGE MARIO GUERRERO VARGAS