
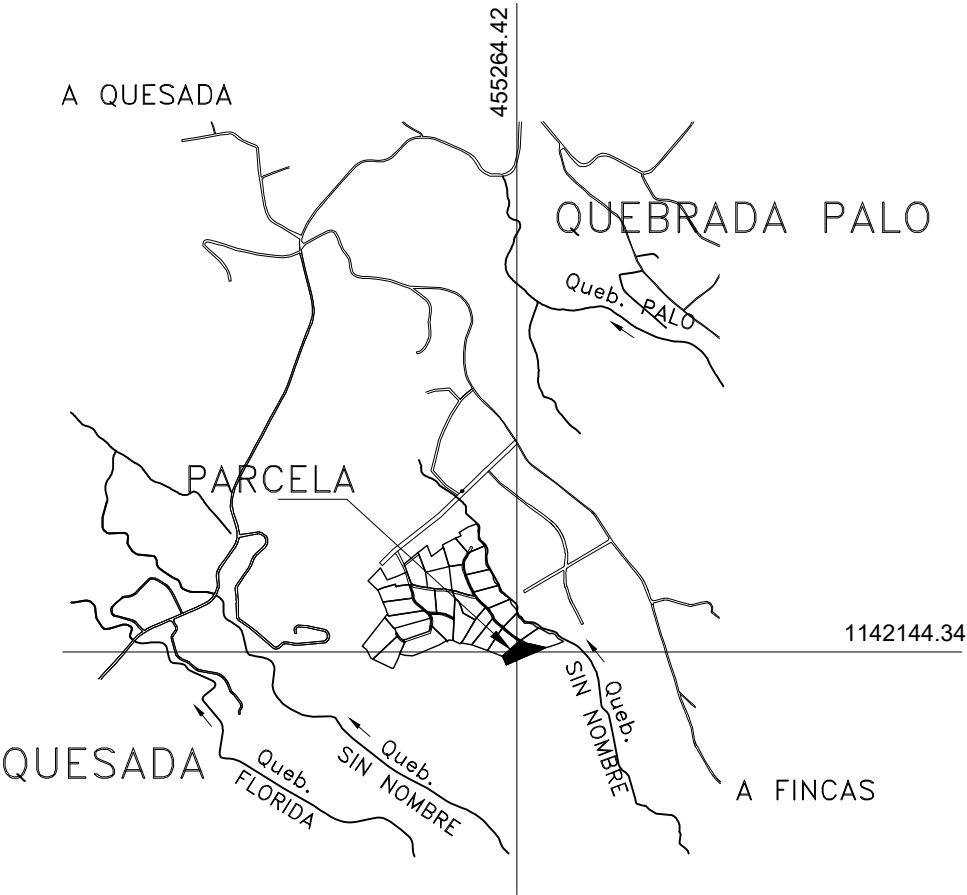


ENTERO N°
XXXXXXXXXX


LISTADO DE COORDENADAS		
PUNTO	ESTE (m)	NORTE (m)
1	455260.26	1142179.48
2	455263.05	1142181.95
3	455270.64	1142178.02
4	455277.81	1142174.82
5	455347.17	1142158.25
6	455317.52	1142143.97
7	455285.82	1142131.99
8	455246.56	1142114.23
9	455217.74	1142100.80
10	455204.61	1142130.19

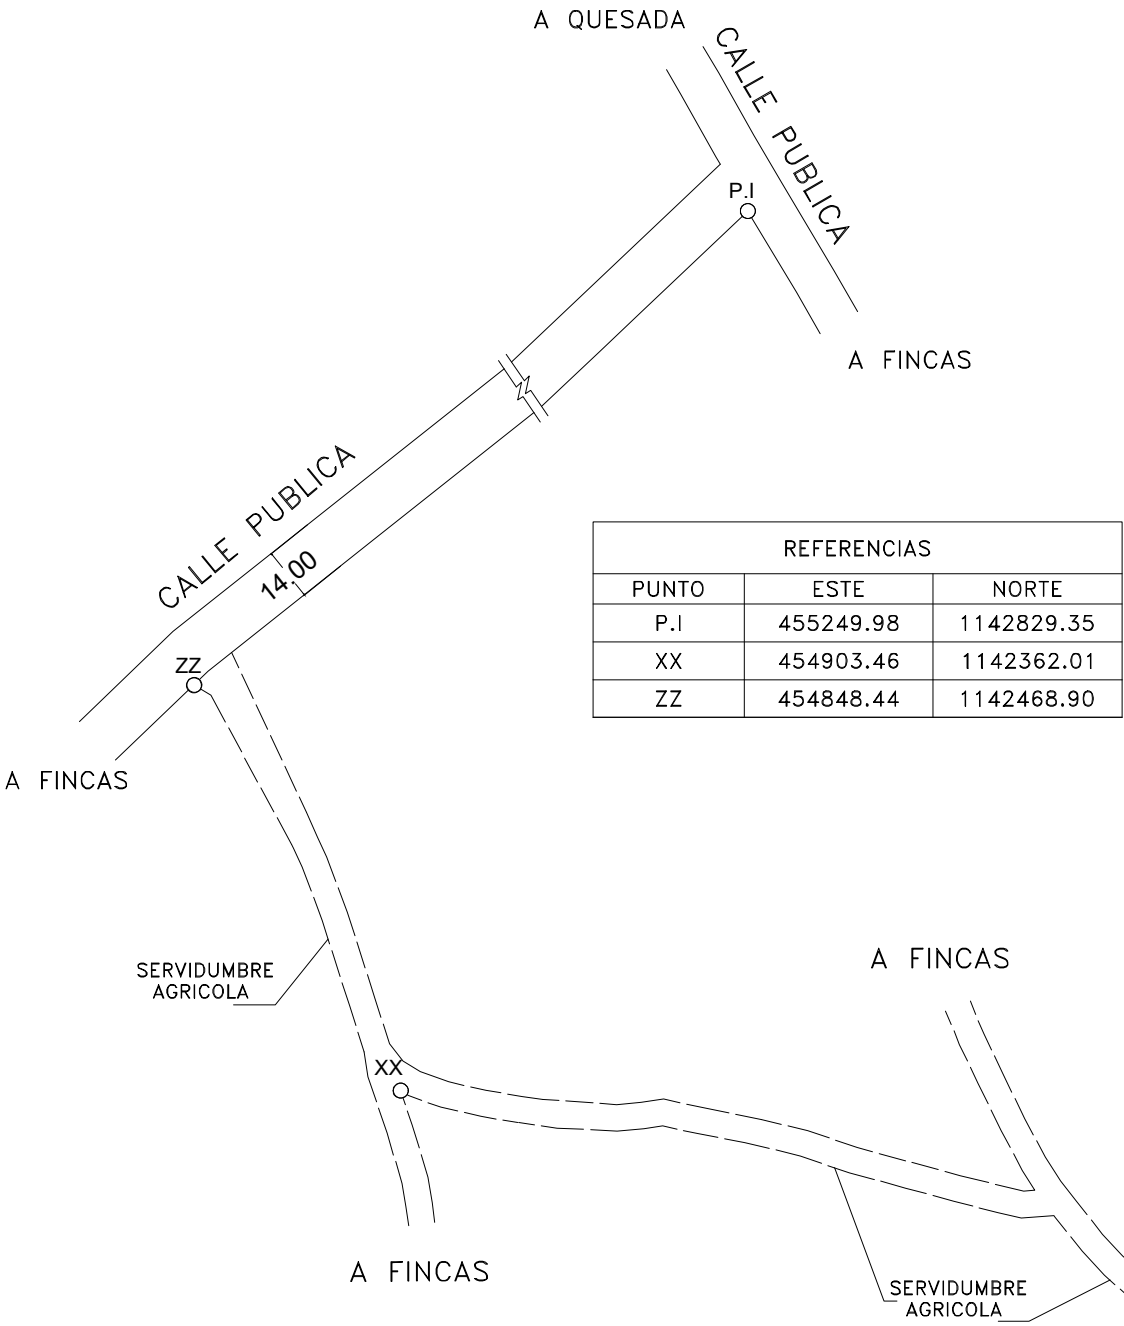

UBICACION GEOGRAFICA

HOJA QUESADA – AGUAS ZARCAS
ESCALA: 1:50,000
AMPLIADA: 1:25,000
EPOCA 2014.59, SISTEMA CR–SIRGAS,
PROYECCION CRTM05

- NOTAS:
- ESCALA DEL MAPA CATASTRAL 1:5000
 - EPOCA 2014.59,SISTEMA CR-SIRGAS, PROYECCION CRTM05,
 - METODO DE ENLACE A LA RED DE COORDENADAS CRTM05, MEDICION ENLACE A ESTACION CIQUE
 - EXACTITUD RELATIVA : +/-0.10m,
 - EXACTITUD ABSOLUTA : +/-0.10m
 - DOY FE QUE LOS LINDEROS SON EXISTENTES
 - TODAS LAS MEDIDAS ESTAN DADAS EN METROS
 - MODIFICA AL PLANO CATASTRADO N°A-1630235-2013
 - FRENTE A SERVIDUMBRE AGRICOLA DE VERTICE 1 AL 4: 20.13m
 - PARCELA EXCLUSIVAMENTE PARA USO AGRICOLA
 - LOS PUNTOS XX Y ZZ SON VERTICES DE LA SERVIDUMBRE
 - COLINDANTE A: 21001050284700.

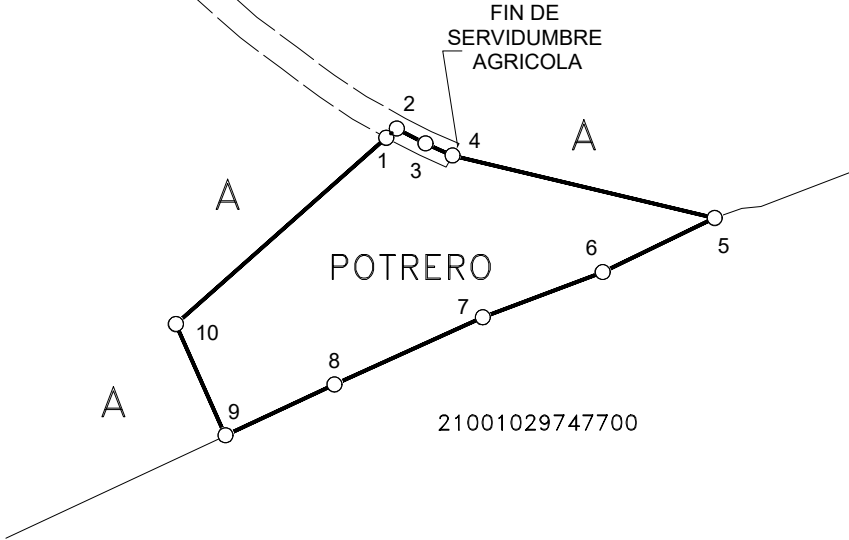

PROTOCOLO: TOMO 24381
FOLIO 026

ESCALA 1:2000
FECHA MAYO 2026

SITUADO EN: LA LLANADA
DISTRITO: 1° QUESADA
CANTON: 10° SAN CARLOS
PROVINCIA: 2° ALAJUELA

PARCELA 22

AREA
5000.00m²

ES PARTE DE
FOLIO REAL
2 502847–000
IDENTIFICADOR PREDIAL
21001050284700
AREA SEGUN REGISTRO
34ha1697.65m²

TOPOGRAFO ASOCIADO: T.A. 8914
JORGE MARIO GUERRERO VARGAS