
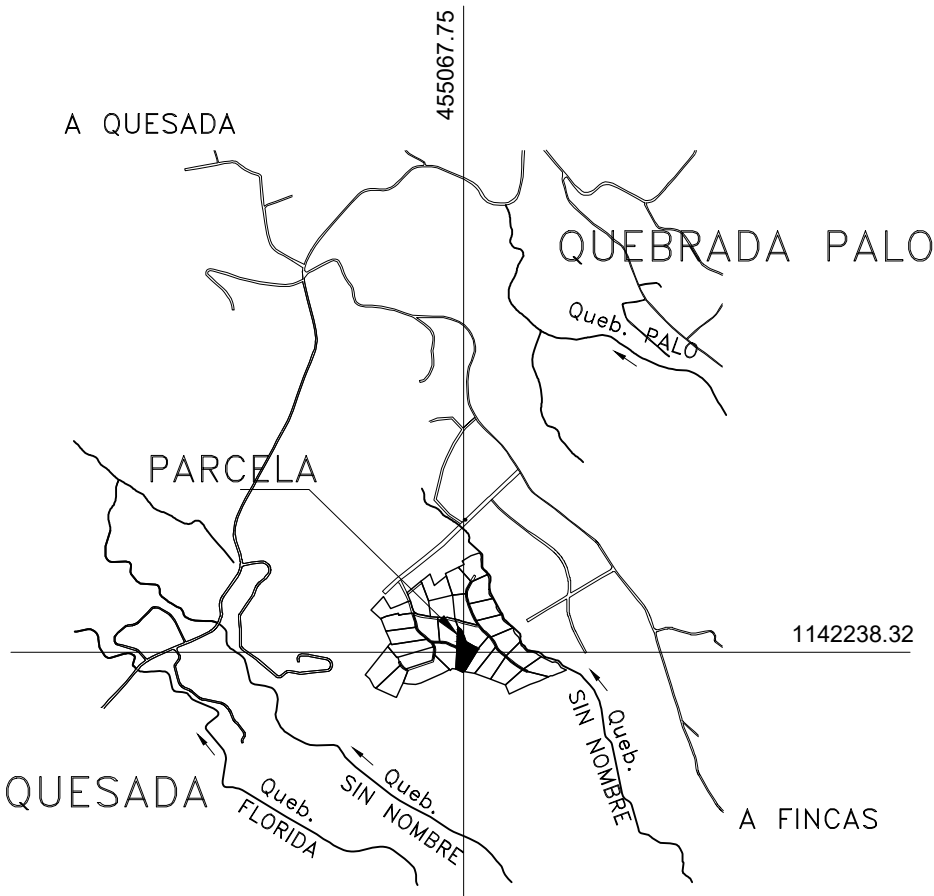


ENTERO N°
XXXXXXXXXX

LISTADO DE COORDENADAS		
PUNTO	ESTE (m)	NORTE (m)
1	455044.21	1142249.18
2	455044.56	1142257.08
3	455047.41	1142322.54
4	455058.62	1142313.06
5	455061.75	1142307.38
6	455067.68	1142291.65
7	455073.99	1142273.29
8	455114.81	1142250.23
9	455074.03	1142182.83
10	455064.13	1142171.43
11	455041.35	1142183.21

REFERENCIAS		
PUNTO	ESTE	NORTE
P.I	455249.98	1142829.35
XX	454903.46	1142362.01
ZZ	454848.44	1142468.90

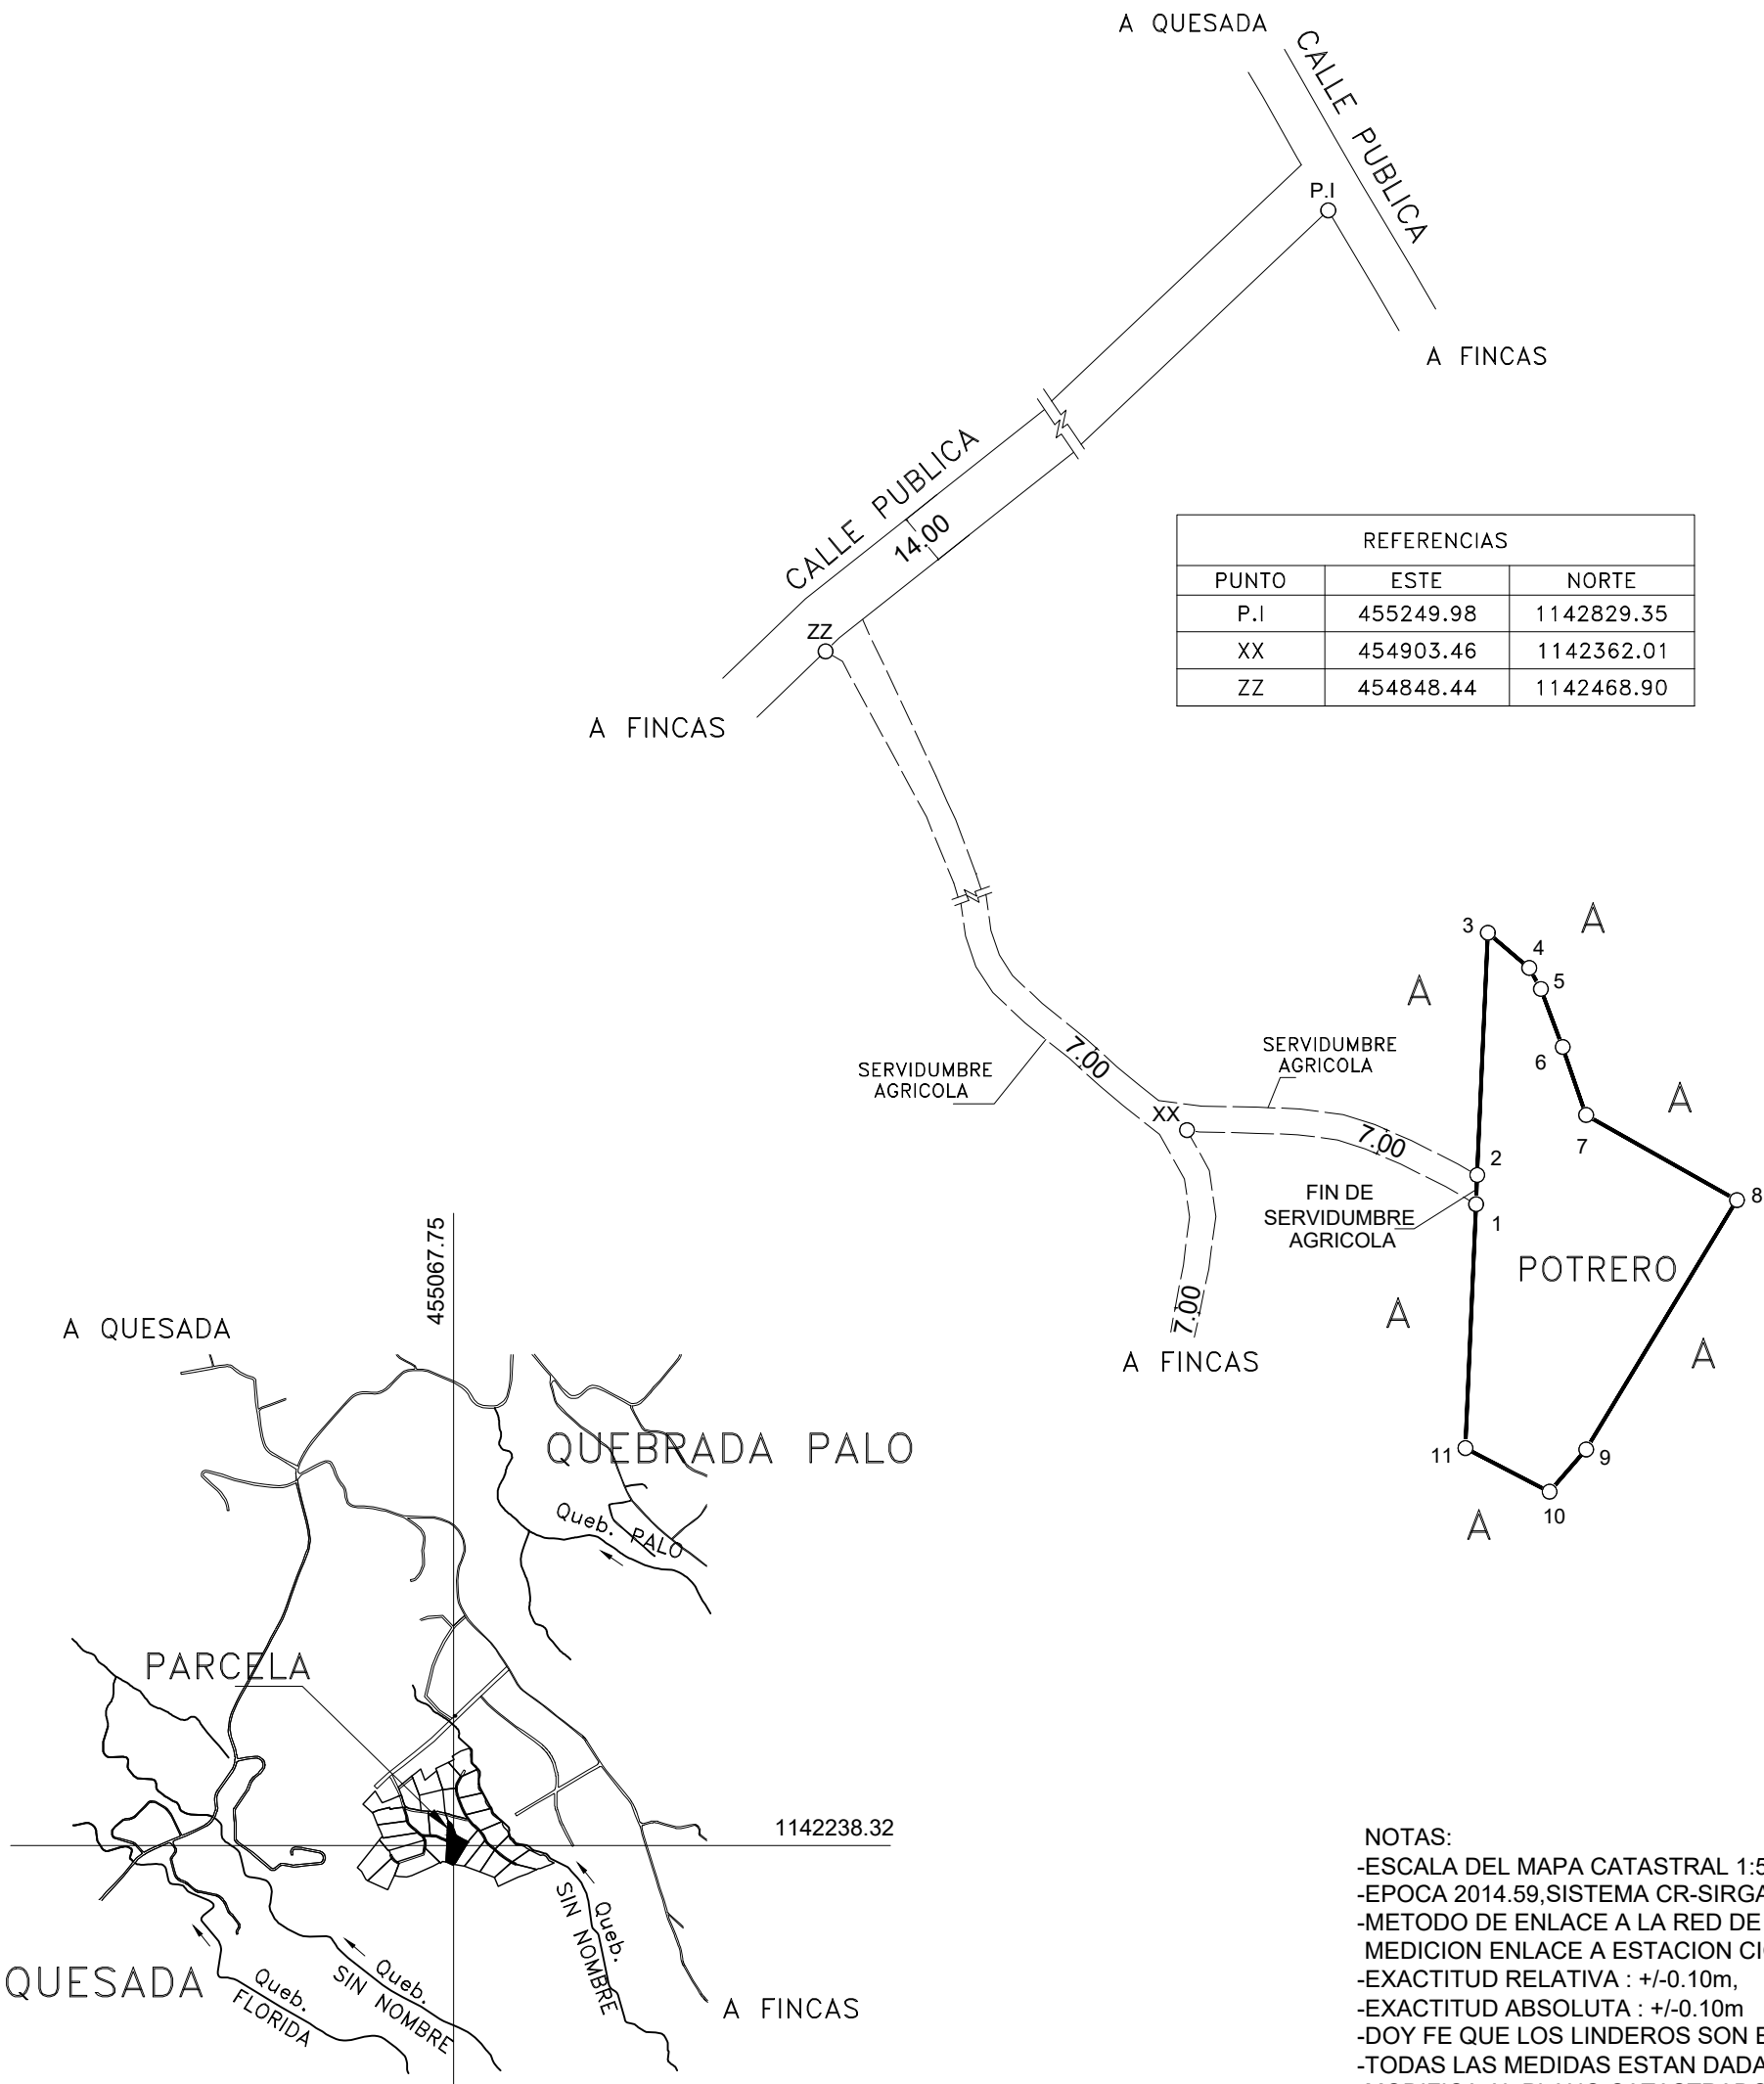

UBICACION GEOGRAFICA

HOJA QUESADA – AGUAS ZARCAS
ESCALA: 1:50,000
AMPLIADA: 1:25,000
EPOCA 2014.59, SISTEMA CR–SIRGAS,
PROYECCION CRTM05

- NOTAS:
- ESCALA DEL MAPA CATASTRAL 1:5000
 - EPOCA 2014.59,SISTEMA CR-SIRGAS, PROYECCION CRTM05,
 - METODO DE ENLACE A LA RED DE COORDENADAS CRTM05, MEDICION ENLACE A ESTACION CIQUE
 - EXACTITUD RELATIVA : +/-0.10m,
 - EXACTITUD ABSOLUTA : +/-0.10m
 - DOY FE QUE LOS LINDEROS SON EXISTENTES
 - TODAS LAS MEDIDAS ESTAN DADAS EN METROS
 - MODIFICA AL PLANO CATASTRADO N°A-1630235-2013
 - FRENTE A SERVIDUMBRE AGRICOLA DE VERTICE 1 AL 2: 7.91m
 - PARCELA EXCLUSIVAMENTE PARA USO AGRICOLA
 - LOS PUNTOS XX Y ZZ SON VERTICES DE LA SERVIDUMBRE
 - COLINDANTE A: 21001050284700.

PROTOCOLO: TOMO 24381
FOLIO 026

ESCALA 1:2000
FECHA MAYO 2026

SITUADO EN: LA LLANADA
DISTRITO: 1° QUESADA
CANTON: 10° SAN CARLOS
PROVINCIA: 2° ALAJUELA

PARCELA 27

AREA
5686.71m²

ES PARTE DE
FOLIO REAL
2 502847–000
IDENTIFICADOR PREDIAL
21001050284700
AREA SEGUN REGISTRO
34ha1697.65m²

TOPOGRAFO ASOCIADO: T.A. 8914
JORGE MARIO GUERRERO VARGAS