
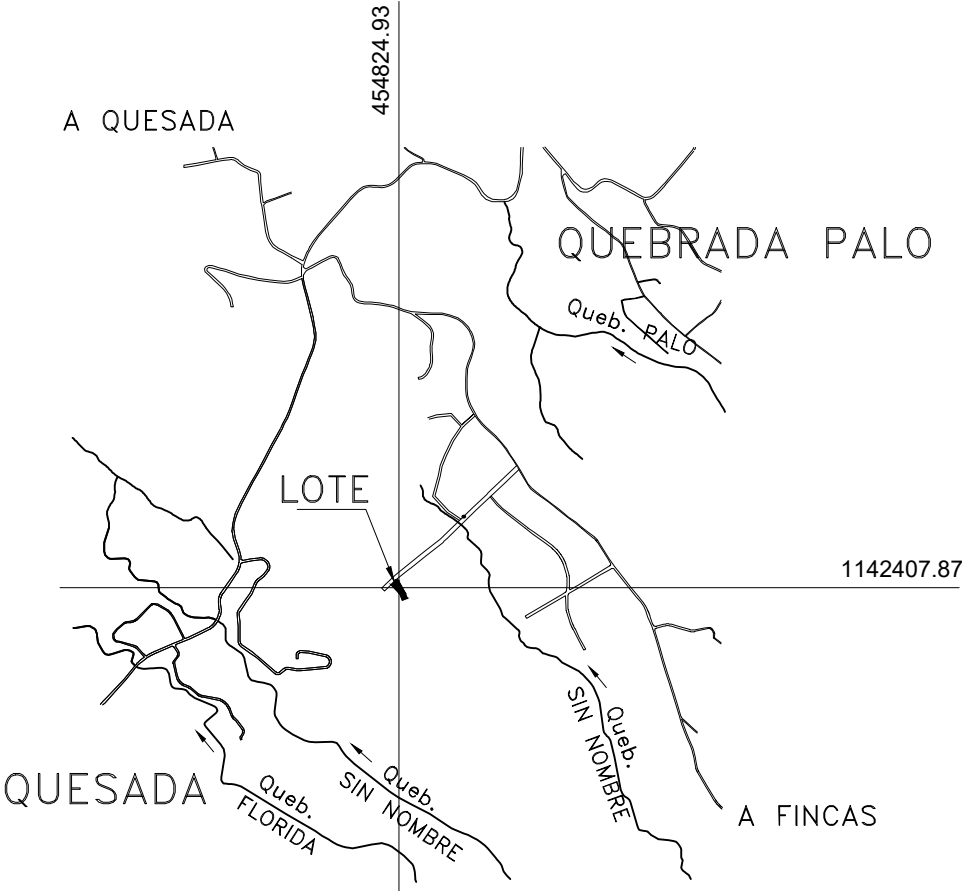


ENTERO N°
XXXXXXXXXX

NOTAS:
-ESCALA DEL MAPA CATASTRAL 1:5000
-EPOCA 2014.59,SISTEMA CR-SIRGAS, PROYECCION CRTM05,
-METODO DE ENLACE A LA RED CR-SIRGAS, MEDICION NTRIP CON EQUIPO GNSS.
ENLACE A ESTACION CIQE
-EXACTITUD RELATIVA : +/-0.10m,
-EXACTITUD ABSOLUTA : +/-0.10m
-DOY FE QUE LOS LINDEROS SON EXISTENTES
-TODAS LAS MEDIDAS ESTAN DADAS EN METROS
-MODIFICA AL PLANO CATASTRADO N°A-1630235-2013
-COLINDANTE A: 21001050284700

LISTADO DE COORDENADAS		
PUNTO	ESTE (m)	NORTE (m)
1	454829.91	1142451.01
2	454848.44	1142468.90
3	454851.06	1142465.30
4	454852.96	1142466.75
5	454875.97	1142424.58
6	454882.78	1142406.43
7	454867.36	1142400.10
8	454858.80	1142421.45

REFERENCIAS		
PUNTO	ESTE	NORTE
P.I	455249.98	1142829.35

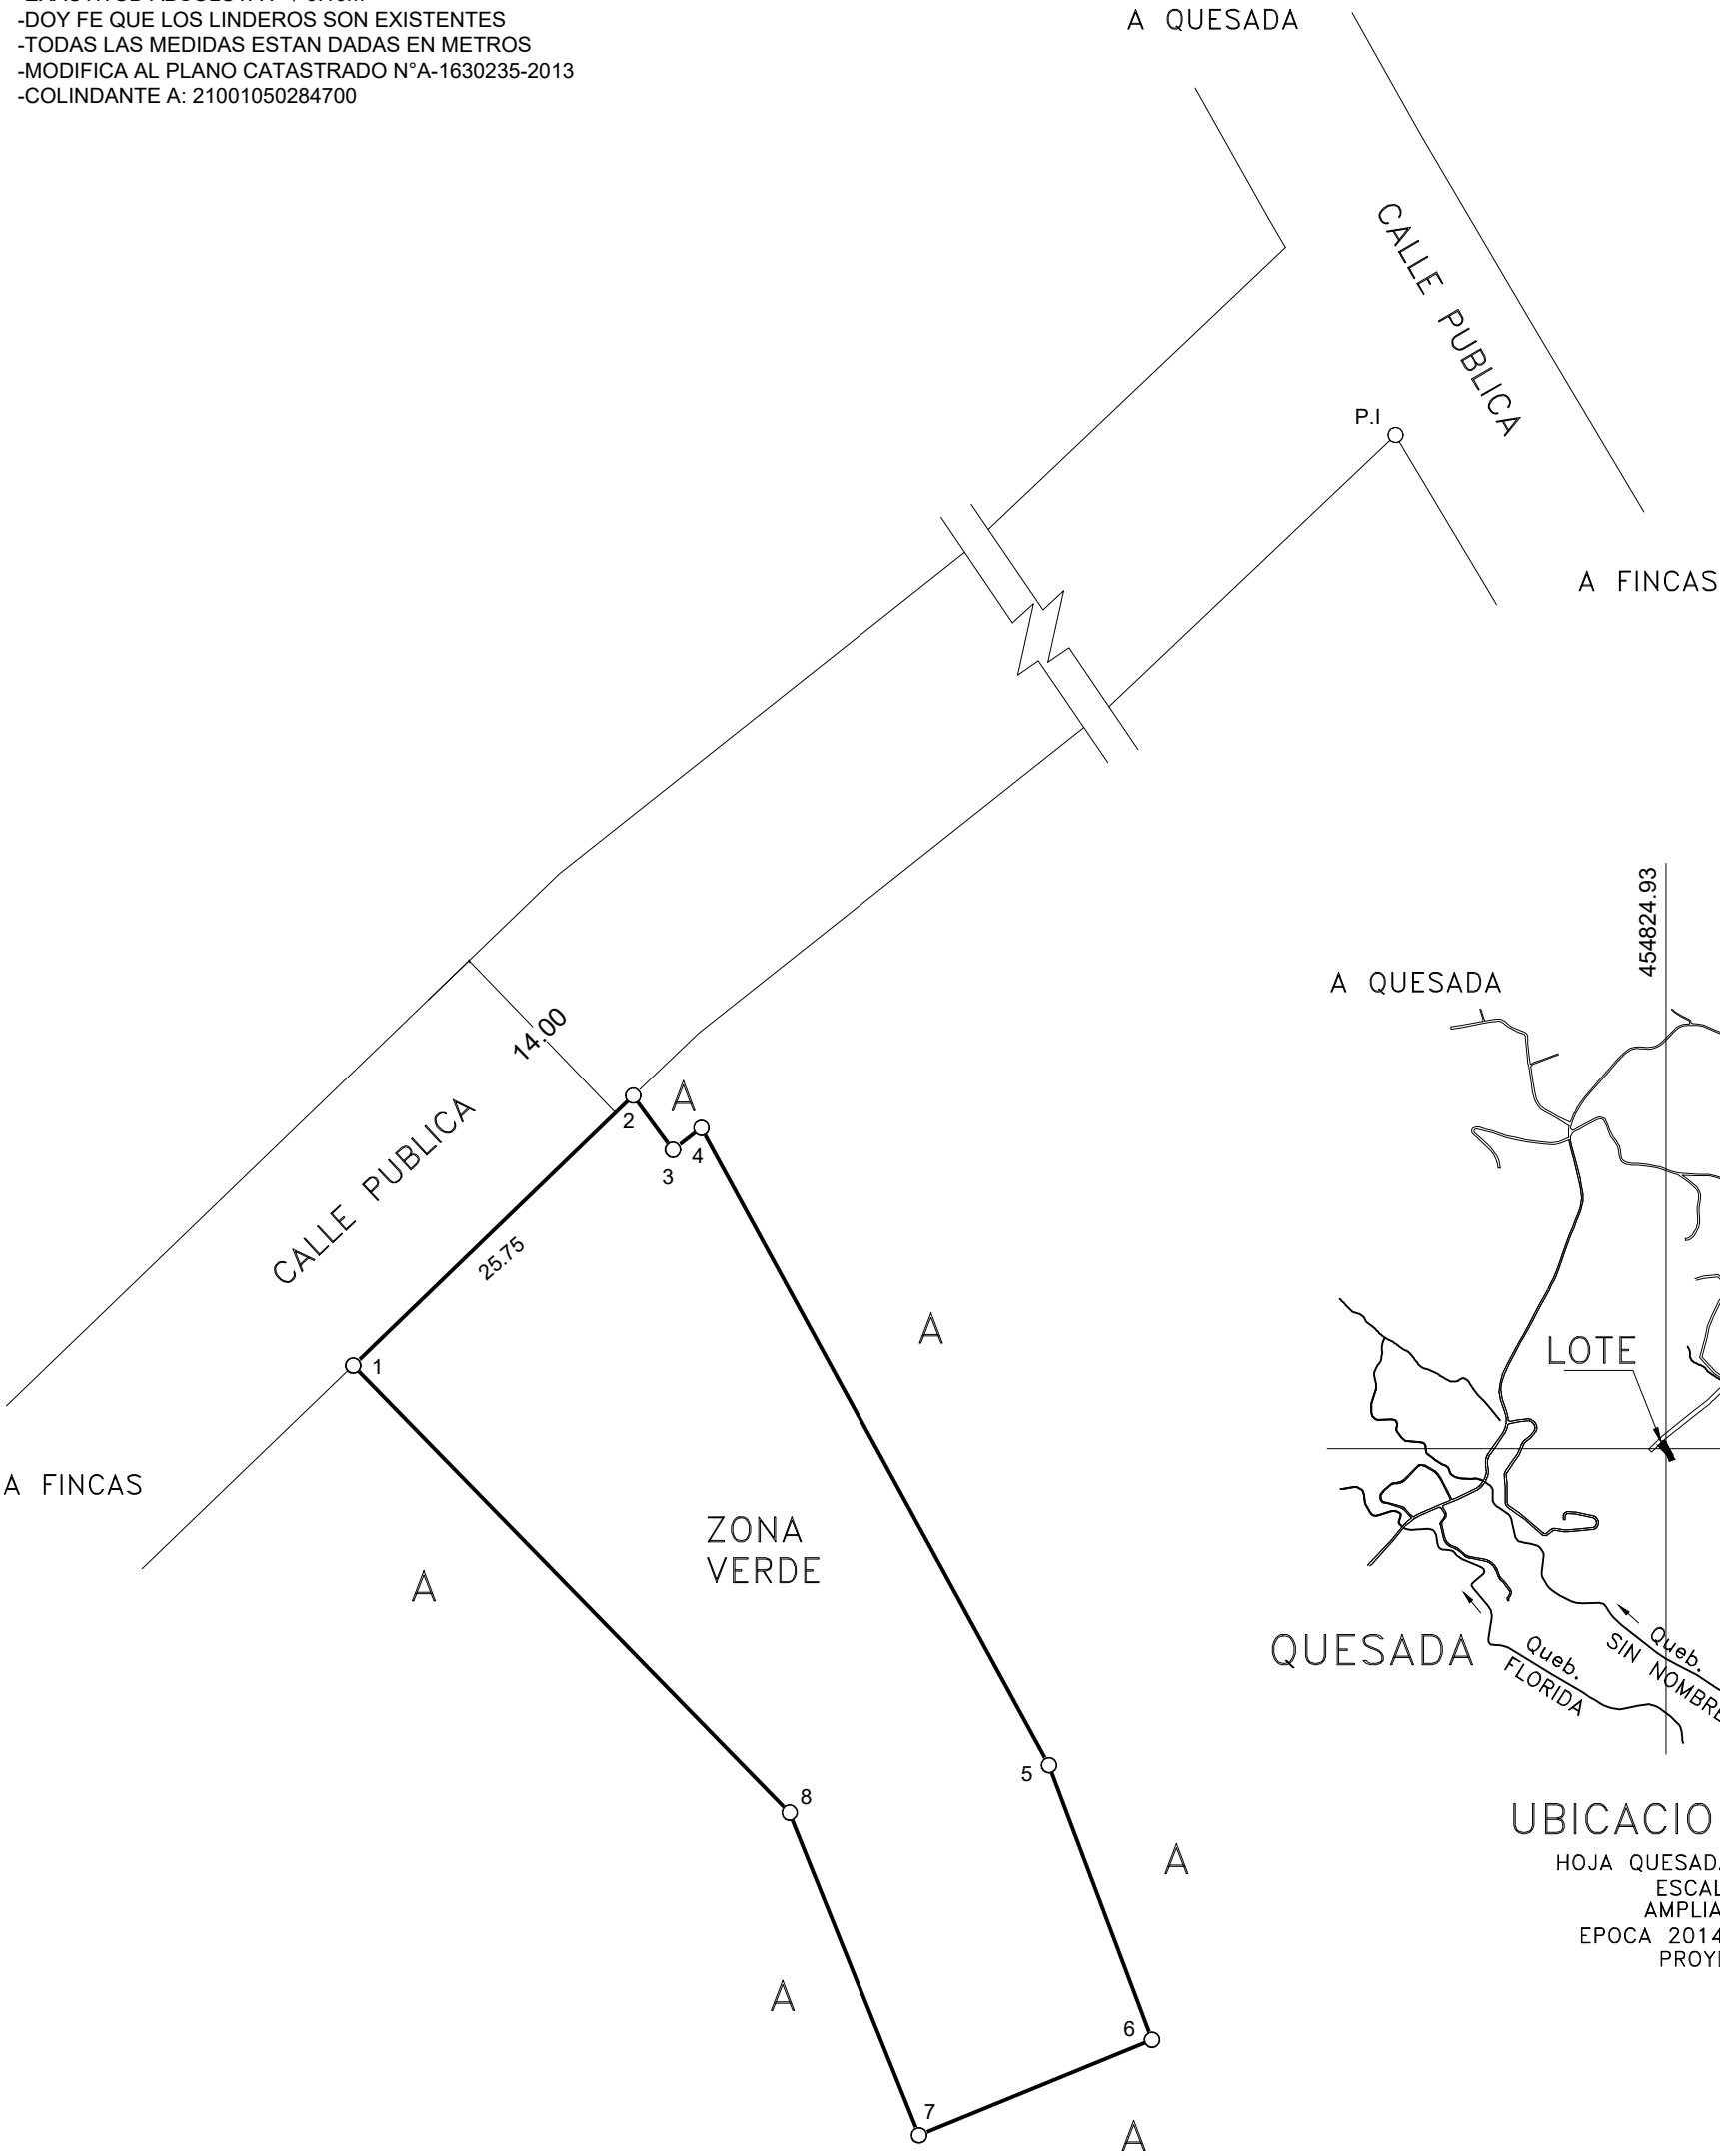

UBICACION GEOGRAFICA

HOJA QUESADA – AGUAS ZARCAS
ESCALA: 1:50,000
AMPLIADA: 1:25,000
EPOCA 2014.59, SISTEMA CR–SIRGAS,
PROYECCION CRTM05

PROTOCOLO: TOMO 24381
FOLIO 026

ESCALA 1:500
FECHA MAYO 2026

SITUADO EN: LA LLANADA

DISTRITO: 1° QUESADA

CANTON: 10° SAN CARLOS

PROVINCIA: 2° ALAJUELA

AREA

1379.41m²

ES PARTE DE
FOLIO REAL

2 502847–000

IDENTIFICADOR PREDIAL
21001050284700

AREA SEGUN REGISTRO
34ha1697.65m²

TOPOGRAFO ASOCIADO: T.A. 8914
JORGE MARIO GUERRERO VARGAS