

ENTERO N°  
XXXXXXXXXX


NOTAS:

- ESCALA DEL MAPA CATASTRAL 1:5000
- EPOCA 2014.59,SISTEMA CR-SIRGAS, PROYECCION CRTM05,
- METODO DE ENLACE A LA RED DE COORDENADAS CRTM05, MEDICION ENLACE A ESTACION CIQUE
- EXACTITUD RELATIVA : +/-0.10m,
- EXACTITUD ABSOLUTA : +/-0.10m
- DOY FE QUE LOS LINDEROS SON EXISTENTES
- TODAS LAS MEDIDAS ESTAN DADAS EN METROS
- MODIFICA AL PLANO CATASTRADO N°A-1630235-2013
- FRENTE A SERVIDUMBRE AGRICOLA DE VERTICE 1 AL 19: 227.77m
- PARCELA EXCLUSIVAMENTE PARA USO AGRICOLA
- LOS PUNTOS XX Y ZZ SON VERTICES DE LA SERVIDUMBRE
- COLINDANTE A: 21001050284700.

LISTADO DE COORDENADAS

| PUNTO | ESTE (m)  | NORTE (m)  |
|-------|-----------|------------|
| 1     | 454987.38 | 1142275.30 |
| 2     | 454987.73 | 1142271.79 |
| 3     | 454969.78 | 1142272.23 |
| 4     | 454956.42 | 1142274.13 |
| 5     | 454951.06 | 1142278.53 |
| 6     | 454947.08 | 1142282.11 |
| 7     | 454924.59 | 1142300.86 |
| 8     | 454916.25 | 1142308.71 |
| 9     | 454912.20 | 1142314.99 |
| 10    | 454909.62 | 1142322.43 |
| 11    | 454907.29 | 1142338.26 |
| 12    | 454903.07 | 1142352.27 |
| 13    | 454899.34 | 1142366.58 |
| 14    | 454908.70 | 1142366.99 |
| 15    | 454916.11 | 1142364.38 |
| 16    | 454926.08 | 1142362.06 |
| 17    | 454956.78 | 1142356.88 |
| 18    | 454979.80 | 1142353.75 |
| 19    | 454980.49 | 1142346.58 |

| REFERENCIAS |           |            |
|-------------|-----------|------------|
| PUNTO       | ESTE      | NORTE      |
| P.I         | 455249.98 | 1142829.35 |
| XX          | 454958.71 | 1142268.02 |
| ZZ          | 454848.44 | 1142468.90 |

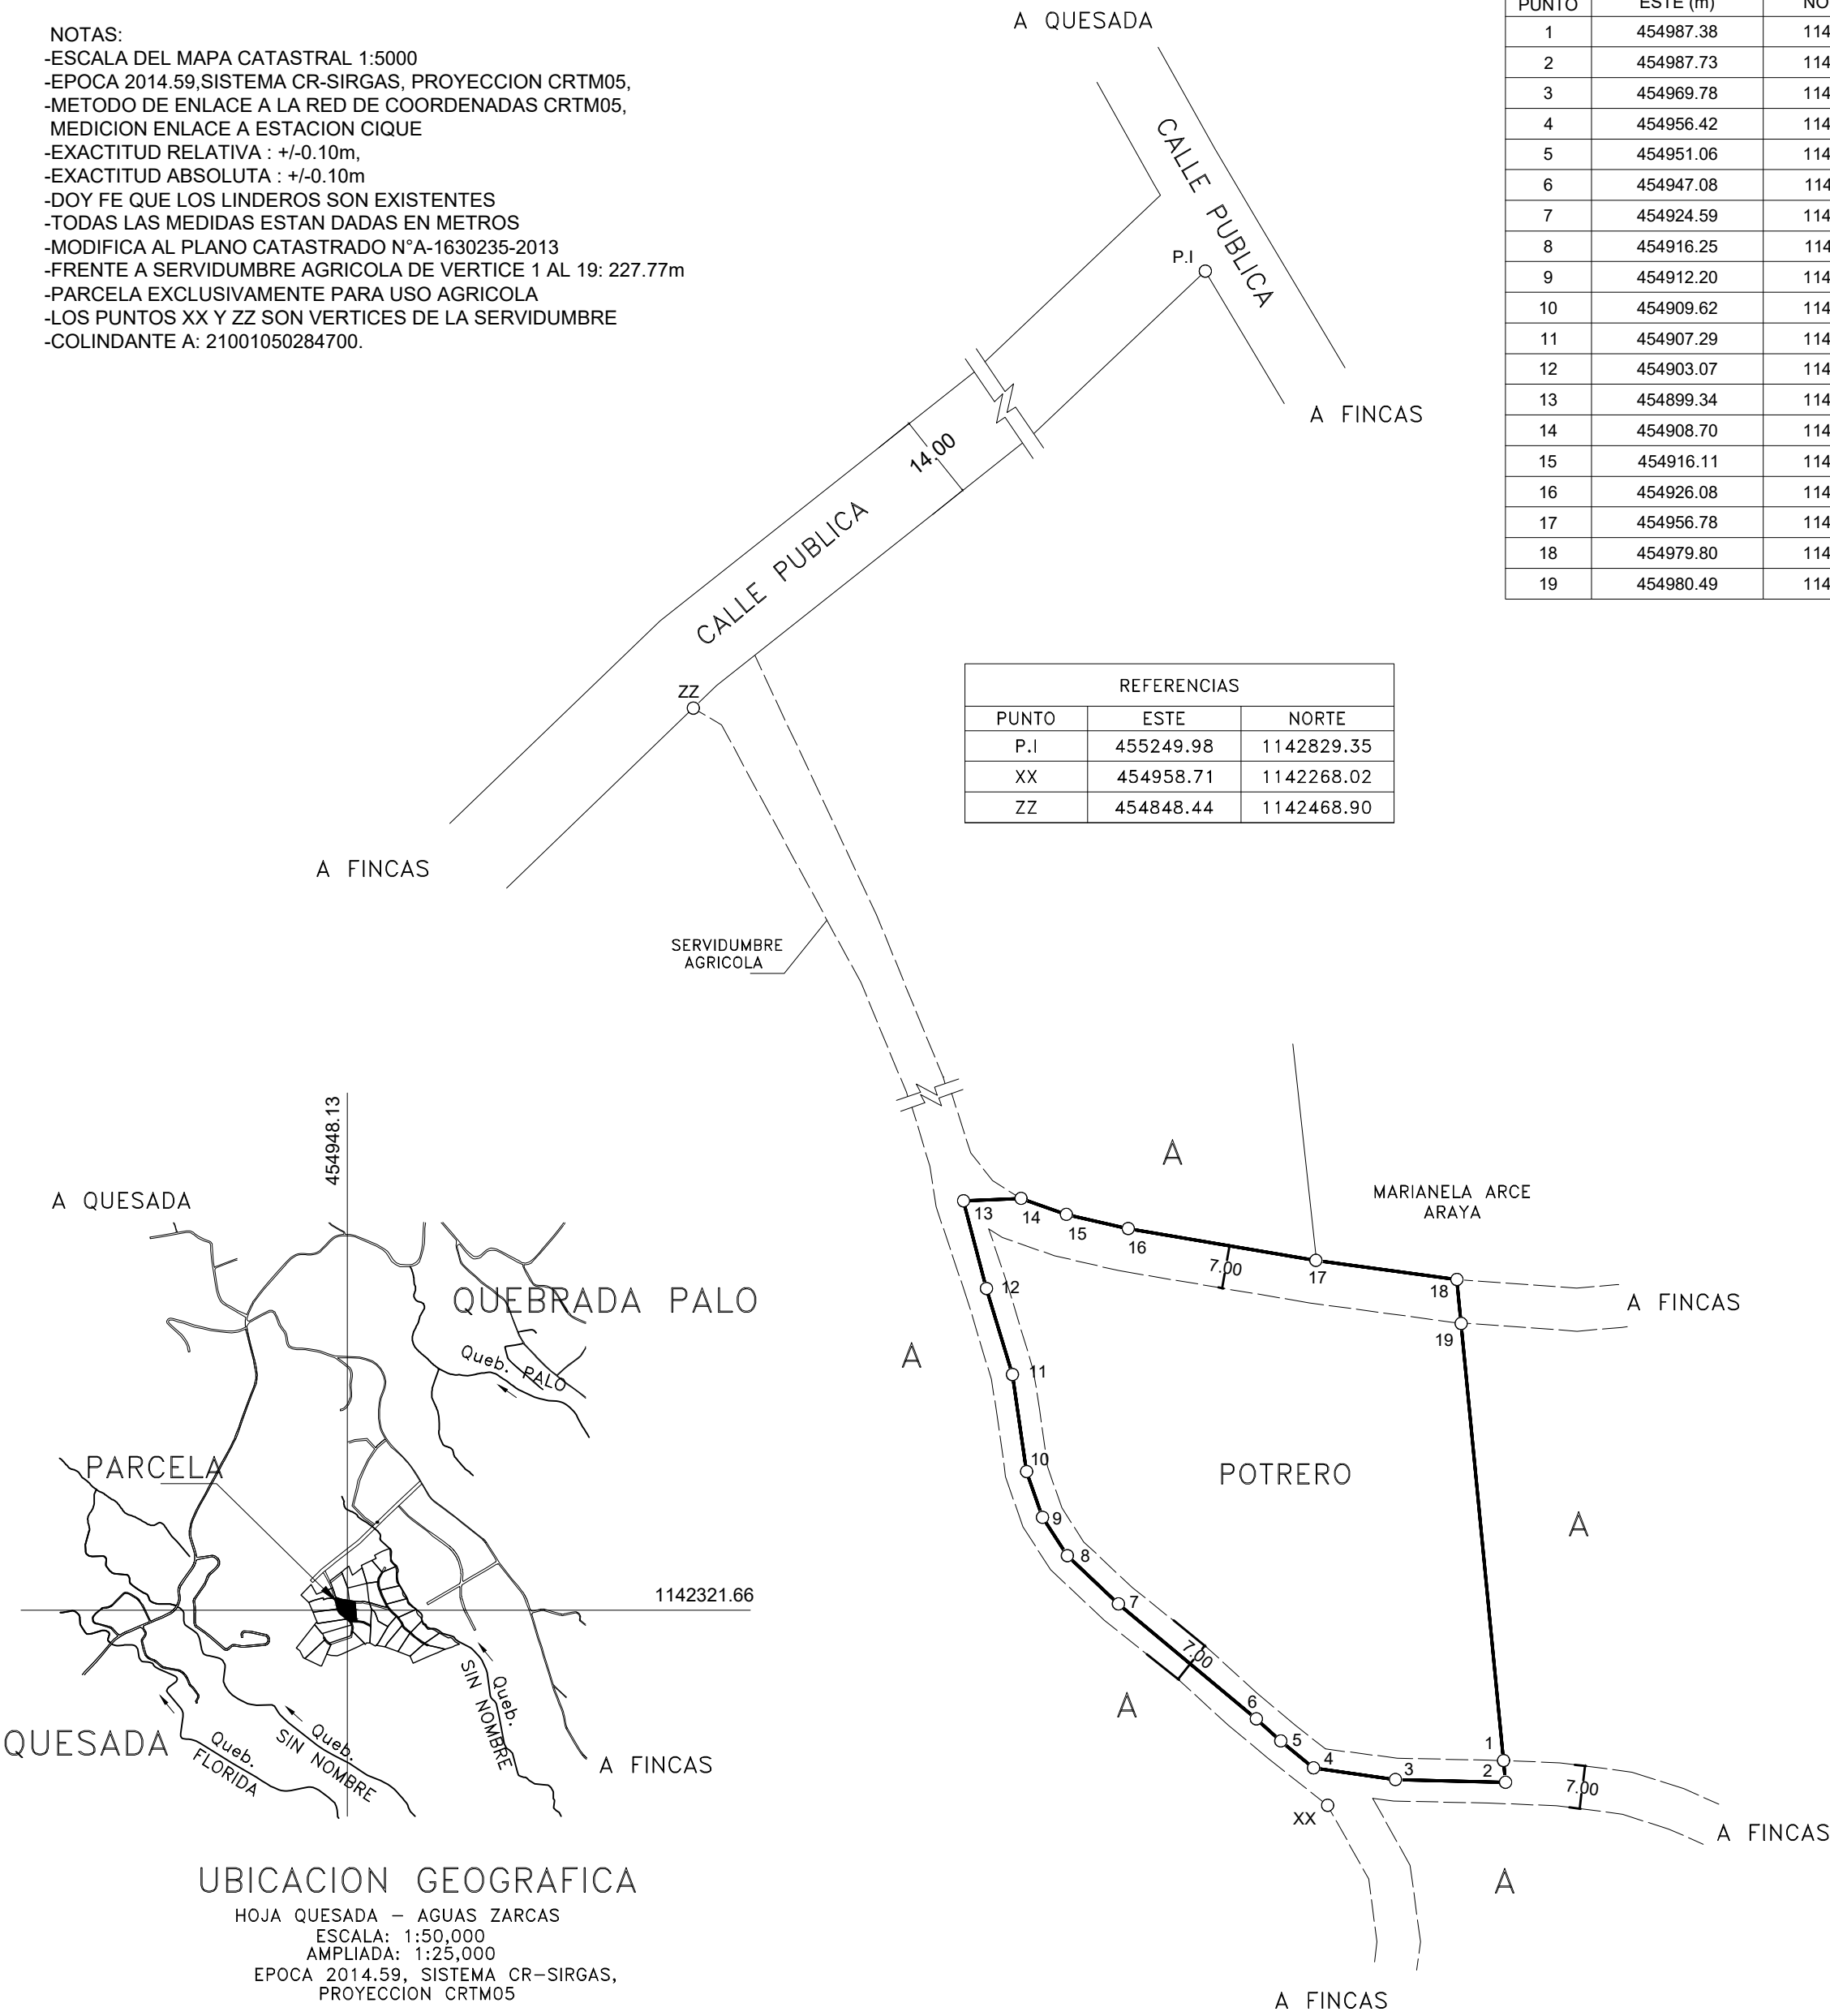

UBICACION GEOGRAFICA

HOJA QUESADA – AGUAS ZARCAS  
ESCALA: 1:50,000  
AMPLIADA: 1:25,000  
EPOCA 2014.59, SISTEMA CR–SIRGAS,  
PROYECCION CRTM05

PROTOCOLO: TOMO 24381  
FOLIO 026

ESCALA 1:1000  
FECHA MAYO 2026

SITUADO EN: LA LLANADA  
DISTRITO: 1° QUESADA  
CANTON: 10° SAN CARLOS  
PROVINCIA: 2° ALAJUELA

PARCELA 30

AREA  
5579.93m<sup>2</sup>

ES PARTE DE  
FOLIO REAL  
2 502847–000  
IDENTIFICADOR PREDIAL  
21001050284700  
AREA SEGUN REGISTRO  
34ha1697.65m<sup>2</sup>

TOPOGRAFO ASOCIADO: T.A. 8914  
JORGE MARIO GUERRERO VARGAS