


ENTERO N°
XXXXXXXXXX

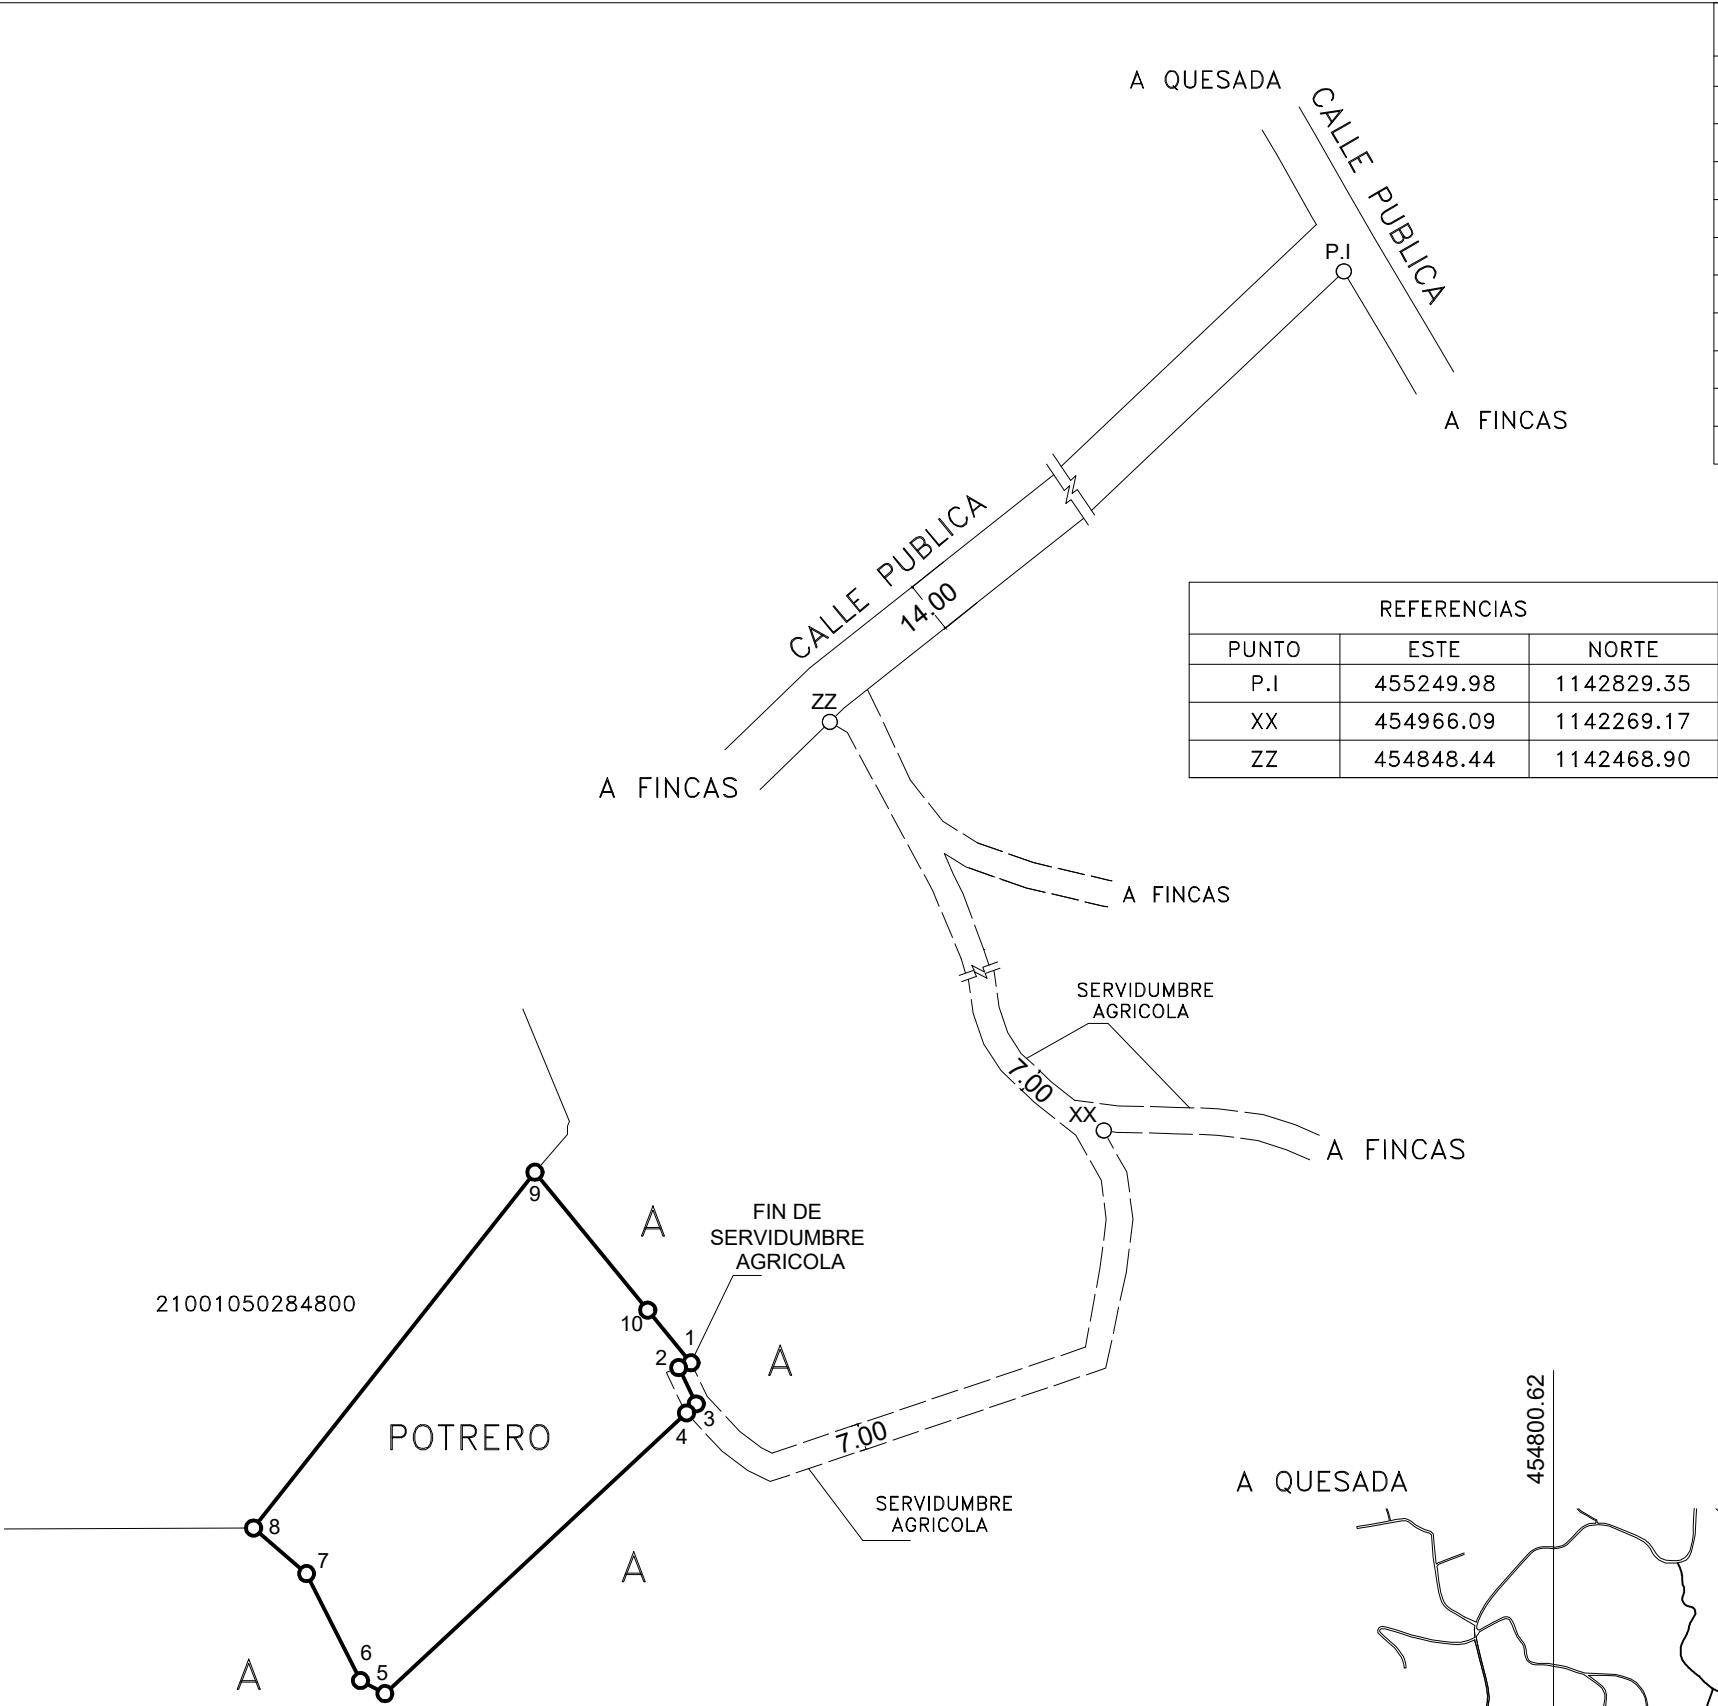


LISTADO DE COORDENADAS		
PUNTO	ESTE (m)	NORTE (m)
1	454856.90	1142207.77
2	454853.63	1142206.51
3	454858.27	1142196.91
4	454855.71	1142194.52
5	454775.91	1142120.26
6	454769.46	1142123.72
7	454755.18	1142152.02
8	454741.16	1142164.06
9	454815.60	1142258.19
10	454845.44	1142221.70

7563.75 m²

REFERENCIAS		
PUNTO	ESTE	NORTE
P.I	455249.98	1142829.35
XX	454966.09	1142269.17
ZZ	454848.44	1142468.90

NOTAS:
-ESCALA DEL MAPA CATASTRAL 1:5000
-EPOCA 2014.59,SISTEMA CR-SIRGAS, PROYECCION CRTM05,
-METODO DE ENLACE A LA RED DE COORDENADAS CRTM05,
MEDICION ENLACE A ESTACION CIQUE
-EXACTITUD RELATIVA : +/-0.10m,
-EXACTITUD ABSOLUTA : +/-0.10m
-DOY FE QUE LOS LINDEROS SON EXISTENTES
-TODAS LAS MEDIDAS ESTAN DADAS EN METROS
-MODIFICA AL PLANO CATASTRADO N°A-1630235-2013
-FRENTE A SERVIDUMBRE AGRICOLA DE VERTICE 1 AL 4: 17.68m
-PARCELA EXCLUSIVAMENTE PARA USO AGRICOLA
-LOS PUNTOS XX Y ZZ SON VERTICES DE LA SERVIDUMBRE
-COLINDANTE A: 21001050284700.

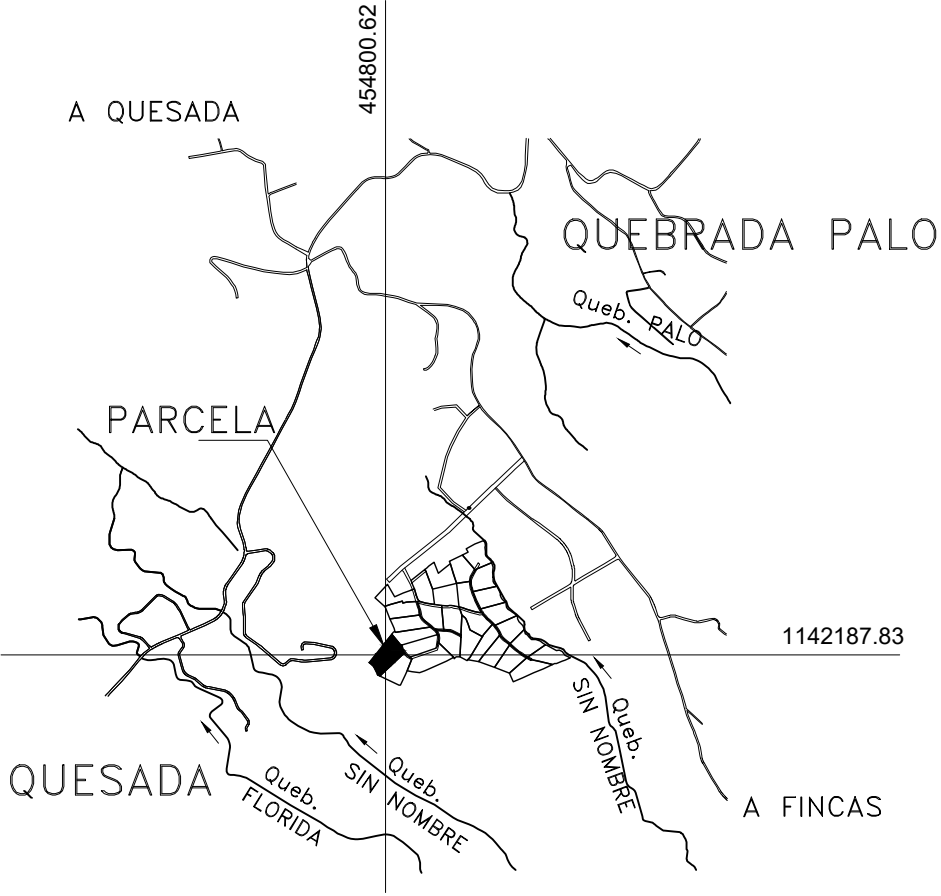

UBICACION GEOGRAFICA
HOJA QUESADA – AGUAS ZARCAS
ESCALA: 1:50,000
AMPLIADA: 1:25,000
EPOCA 2014.59, SISTEMA CR-SIRGAS,
PROYECCION CRTM05

PROTOCOLO: TOMO 24381
FOLIO 026

ESCALA 1:2000
FECHA MAYO 2026

SITUADO EN: LA LLANADA
DISTRITO: 1° QUESADA
CANTON: 10° SAN CARLOS
PROVINCIA: 2° ALAJUELA

PARCELA 33

AREA
7563.75m²

ES PARTE DE
FOLIO REAL
2 502847–000
IDENTIFICADOR PREDIAL
21001050284700
AREA SEGUN REGISTRO
34ha1697.65m²

TOPOGRAFO ASOCIADO: T.A. 8914
JORGE MARIO GUERRERO VARGAS