



ENTERO N°
XXXXXXXXXX

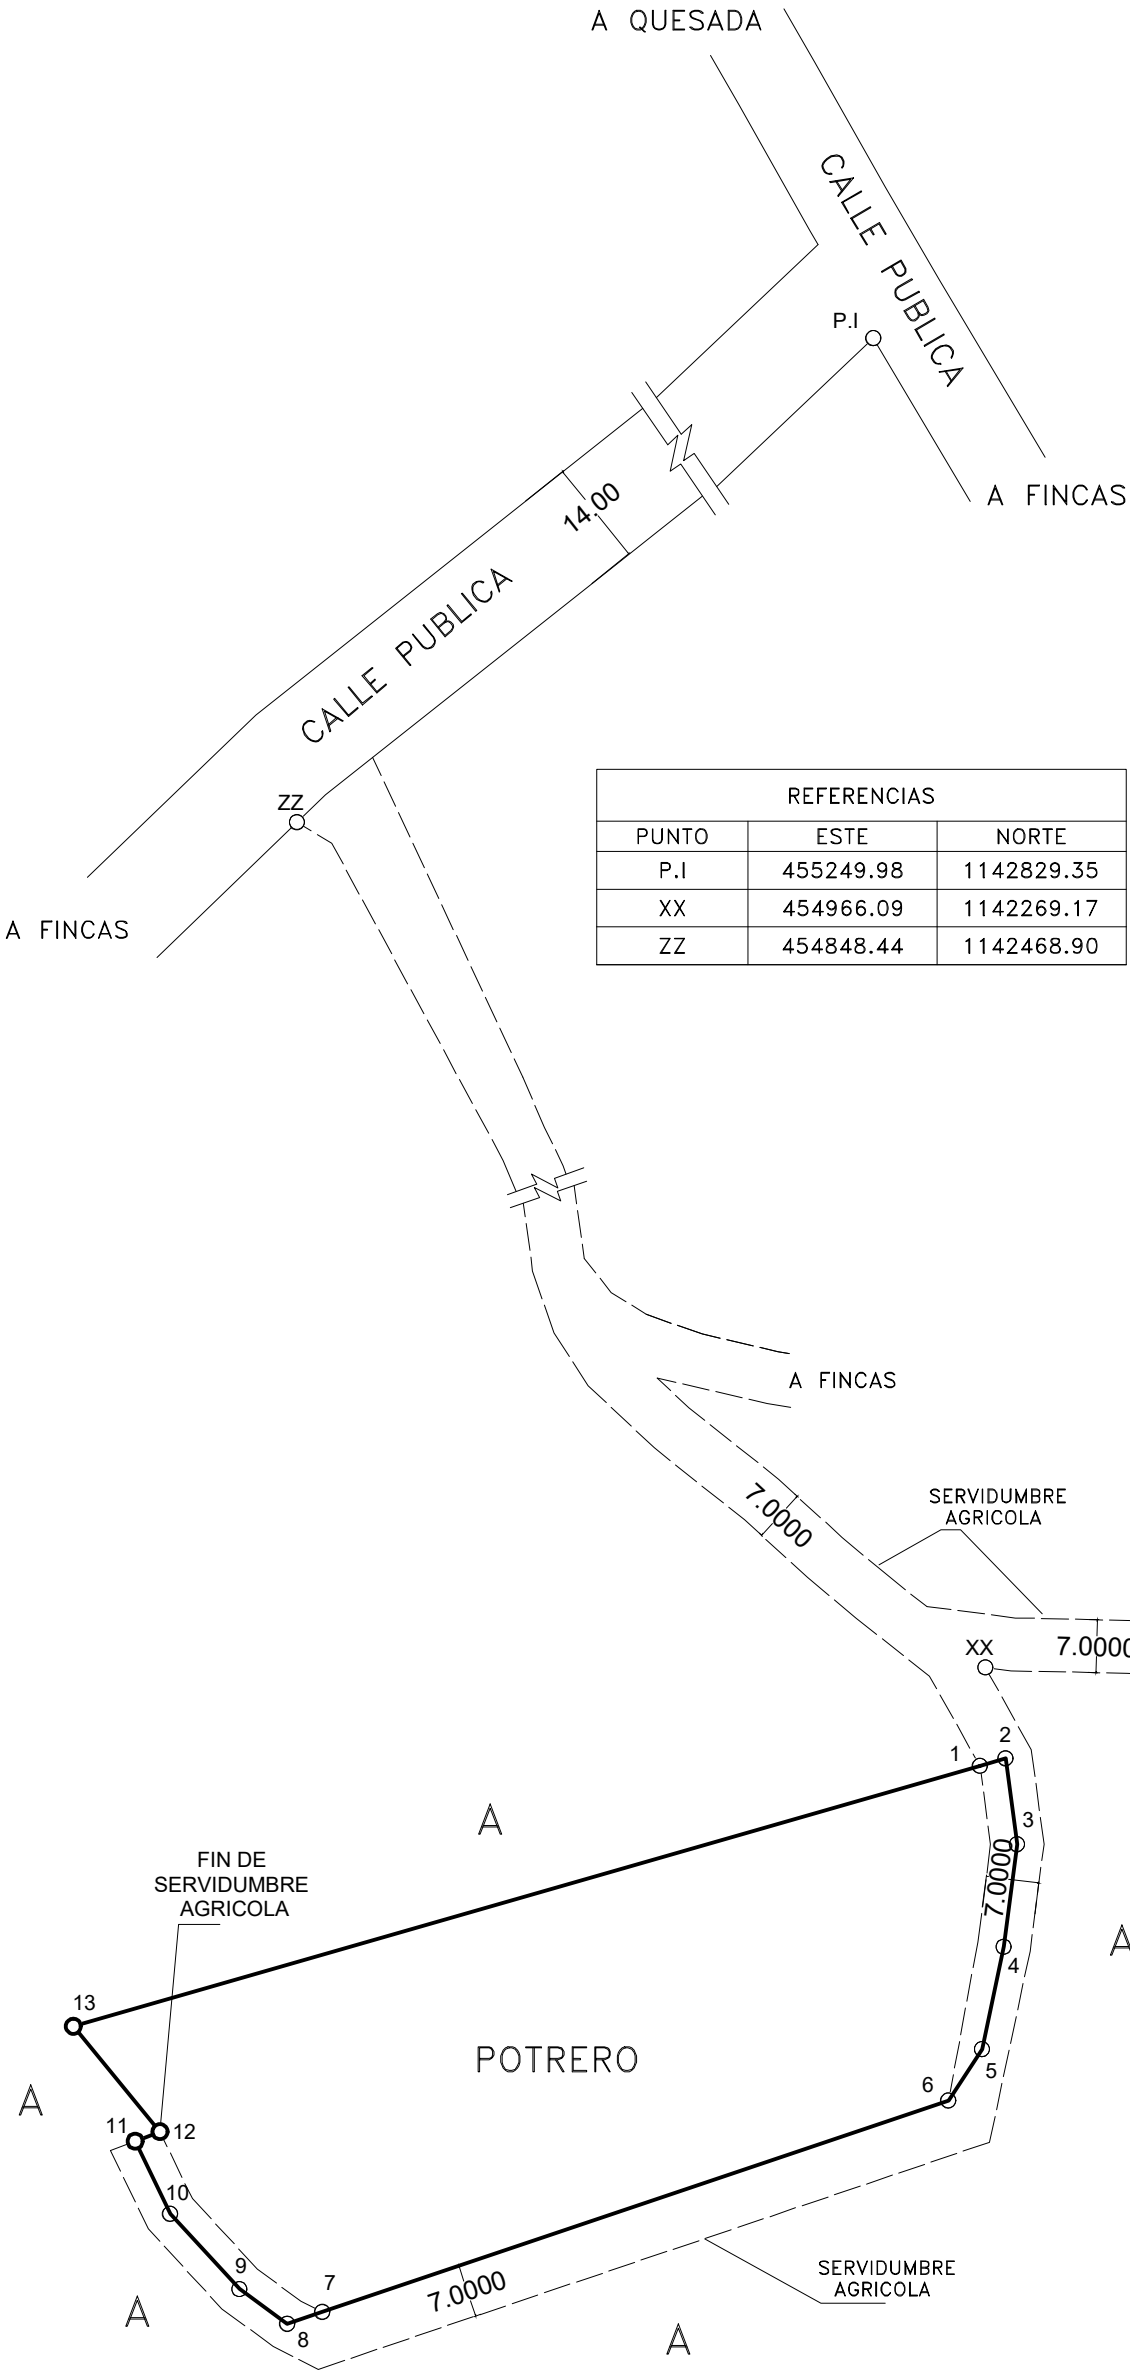

REFERENCIAS		
PUNTO	ESTE	NORTE
P.I	455249.98	1142829.35
XX	454966.09	1142269.17
ZZ	454848.44	1142468.90

LISTADO DE COORDENADAS		
PUNTO	ESTE (m)	NORTE (m)
1	454965.34	1142256.15
2	454968.79	1142257.15
3	454970.32	1142245.79
4	454968.55	1142232.24
5	454965.69	1142218.69
6	454961.21	1142211.90
7	454878.38	1142183.91
8	454873.75	1142182.35
9	454867.45	1142186.96
10	454858.27	1142196.91
11	454853.63	1142206.51
12	454856.90	1142207.77
13	454845.44	1142221.70

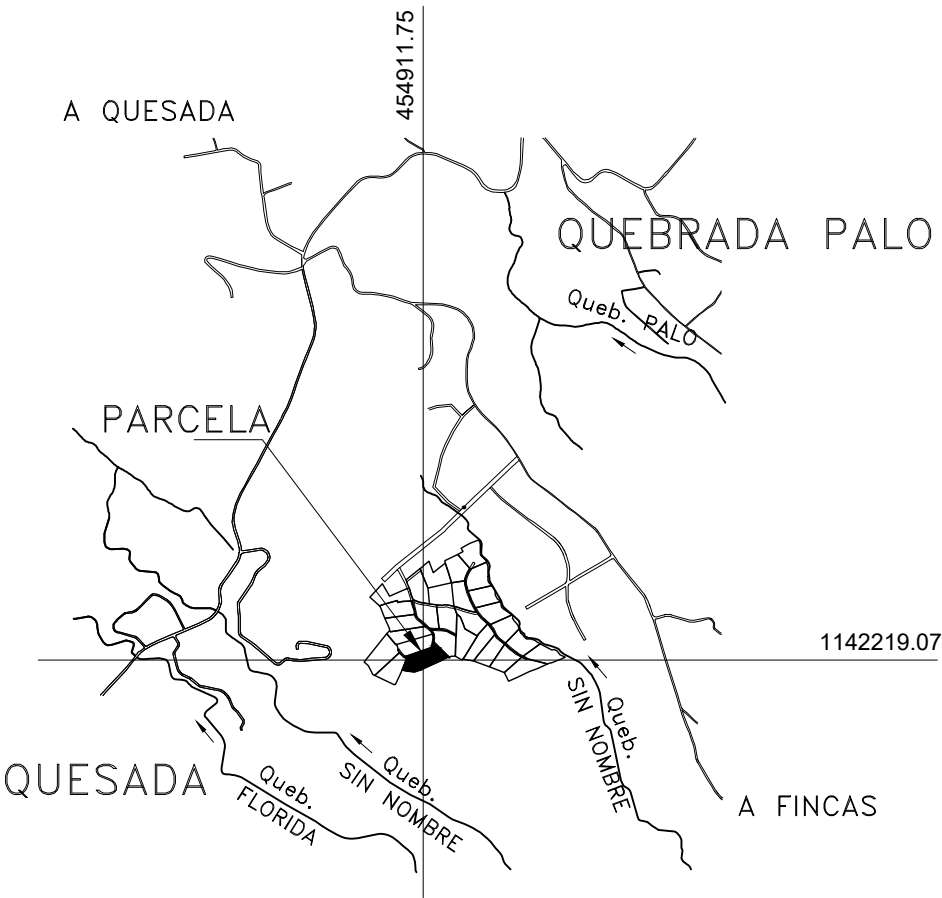

UBICACION GEOGRAFICA
HOJA QUESADA – AGUAS ZARCAS
ESCALA: 1:50,000
AMPLIADA: 1:25,000
EPOCA 2014.59, SISTEMA CR–SIRGAS,
PROYECCION CRTM05

NOTAS:
-ESCALA DEL MAPA CATASTRAL 1:5000
-EPOCA 2014.59,SISTEMA CR-SIRGAS, PROYECCION CRTM05,
-METODO DE ENLACE A LA RED DE COORDENADAS CRTM05,
MEDICION ENLACE A ESTACION CIQUE
-EXACTITUD RELATIVA : +/-0.10m,
-EXACTITUD ABSOLUTA : +/-0.10m
-DOY FE QUE LOS LINDEROS SON EXISTENTES
-TODAS LAS MEDIDAS ESTAN DADAS EN METROS
-MODIFICA AL PLANO CATASTRADO N°A-1630235-2013
-FRENTE A SERVIDUMBRE AGRICOLA DE VERTICE 1 AL 11: 174.95m
-PARCELA EXCLUSIVAMENTE PARA USO AGRICOLA
-LOS PUNTOS XX Y ZZ SON VERTICES DE LA SERVIDUMBRE
-COLINDANTE A: 21001050284700.

PROTOCOLO: TOMO 24381
FOLIO 026

ESCALA 1:1000
FECHA MAYO 2026

SITUADO EN: LA LLANADA

DISTRITO: 1° QUESADA

CANTON: 10° SAN CARLOS

PROVINCIA: 2° ALAJUELA

PARCELA 34

AREA

5000.00m²

ES PARTE DE
FOLIO REAL

2 502847–000

IDENTIFICADOR PREDIAL
21001050284700

AREA SEGUN REGISTRO
34ha1697.65m²

TOPOGRAFO ASOCIADO: T.A. 8914
JORGE MARIO GUERRERO VARGAS