


ENTERO N°
XXXXXXXXXX

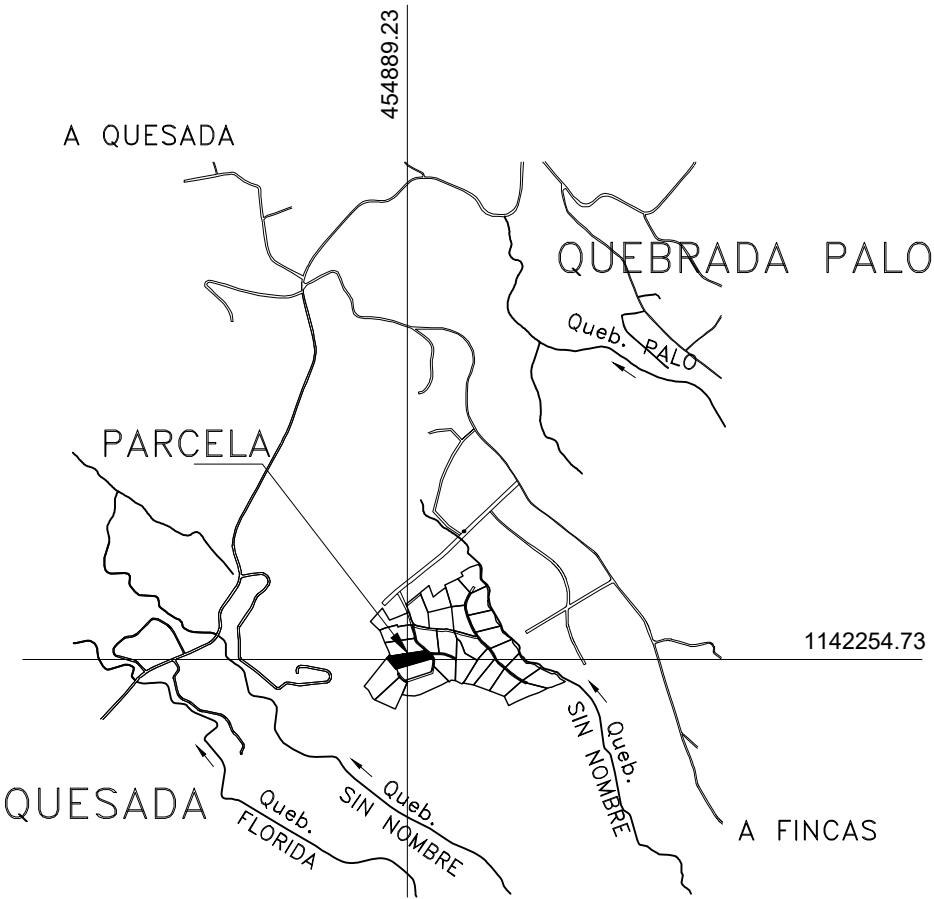


UBICACION GEOGRAFICA

HOJA QUESADA – AGUAS ZARCAS
ESCALA: 1:50,000
AMPLIADA: 1:25,000
EPOCA 2014.59, SISTEMA CR–SIRGAS,
PROYECCION CRTM05

REFERENCIAS		
PUNTO	ESTE	NORTE
P.I	455249.98	1142829.35
XX	454966.09	1142269.17
ZZ	454848.44	1142468.90

LISTADO DE COORDENADAS		
PUNTO	ESTE (m)	NORTE (m)
1	454942.23	1142281.38
2	454947.08	1142282.11
3	454951.06	1142278.53
4	454956.42	1142274.13
5	454961.77	1142269.72
6	454968.79	1142257.15
7	454965.34	1142256.15
8	454845.44	1142221.70
9	454815.60	1142258.19
10	454820.74	1142264.24
11	454824.21	1142268.24
12	454828.14	1142264.04

NOTAS:
-ESCALA DEL MAPA CATASTRAL 1:5000
-EPOCA 2014.59,SISTEMA CR-SIRGAS, PROYECCION CRTM05,
-METODO DE ENLACE A LA RED DE COORDENADAS CRTM05,
MEDICION ENLACE A ESTACION CIQUE
-EXACTITUD RELATIVA : +/-0.10m,
-EXACTITUD ABSOLUTA : +/-0.10m
-DOY FE QUE LOS LINDEROS SON EXISTENTES
-TODAS LAS MEDIDAS ESTAN DADAS EN METROS
-MODIFICA AL PLANO CATASTRADO N°A-1630235-2013
-FRENTE A SERVIDUMBRE AGRICOLA DE VERTICE 1 AL 7: 42.13m
-PARCELA EXCLUSIVAMENTE PARA USO AGRICOLA
-LOS PUNTOS XX Y ZZ SON VERTICES DE LA SERVIDUMBRE
-COLINDANTE A: 21001050284700.

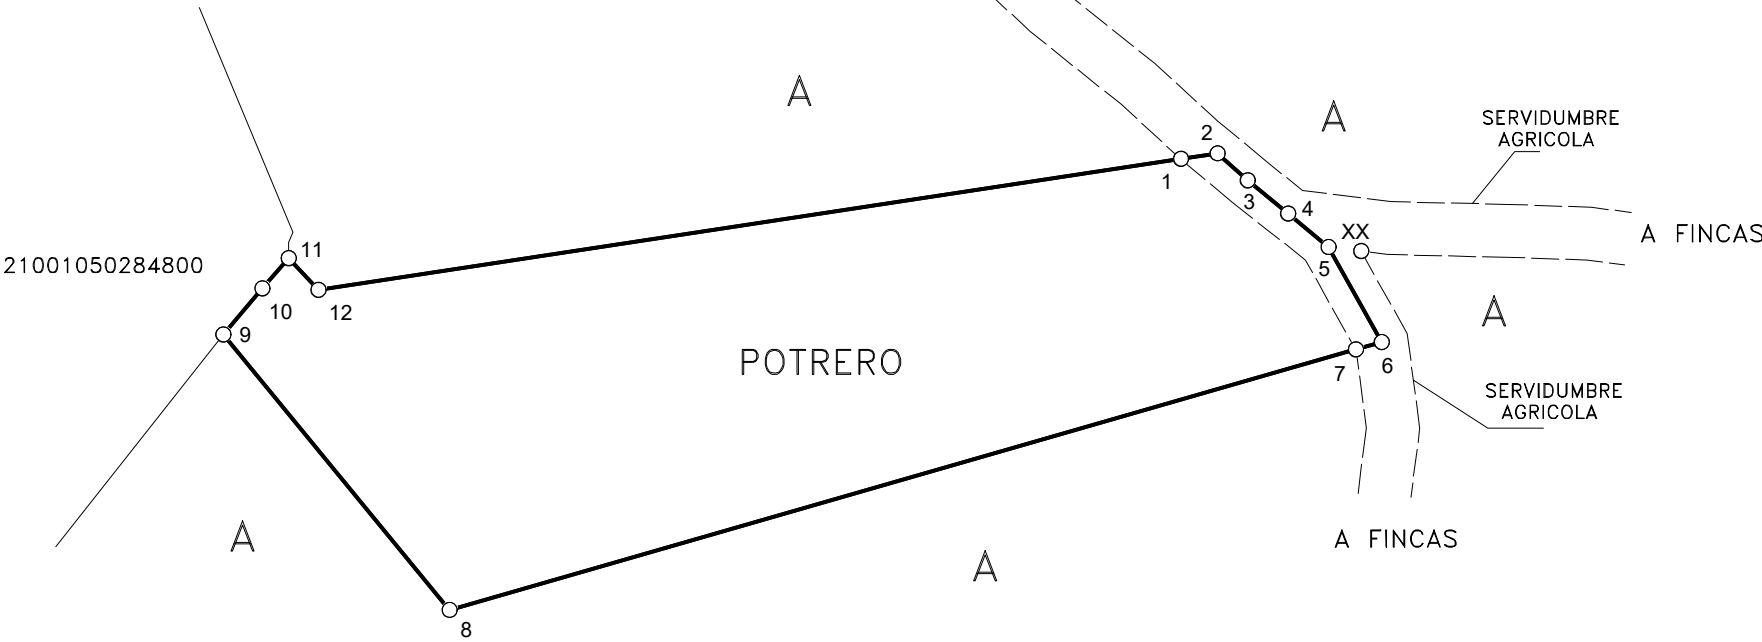

PROTOCOLO: TOMO 24381
FOLIO 026

ESCALA 1:1000
FECHA MAYO 2026

SITUADO EN: LA LLANADA
DISTRITO: 1° QUESADA
CANTON: 10° SAN CARLOS
PROVINCIA: 2° ALAJUELA

PARCELA 35

AREA
5000.00m²

ES PARTE DE
FOLIO REAL
2 502847–000
IDENTIFICADOR PREDIAL
21001050284700
AREA SEGUN REGISTRO
34ha1697.65m²

TOPOGRAFO ASOCIADO: T.A. 8914
JORGE MARIO GUERRERO VARGAS