


ENTERO N°
XXXXXXXXXX

NOTAS:
-ESCALA DEL MAPA CATASTRAL 1:5000
-EPOCA 2014.59,SISTEMA CR-SIRGAS, PROYECCION CRTM05,
-METODO DE ENLACE A LA RED DE COORDENADAS CRTM05,
MEDICION ENLACE A ESTACION CIQUE
-EXACTITUD RELATIVA : +/-0.10m,
-EXACTITUD ABSOLUTA : +/-0.10m
-DOY FE QUE LOS LINDEROS SON EXISTENTES
-TODAS LAS MEDIDAS ESTAN DADAS EN METROS
-MODIFICA AL PLANO CATASTRADO N°A-1630235-2013
-FRENTE A SERVIDUMBRE AGRICOLA DE VERTICE 1 AL 7: 64.51m
-PARCELA EXCLUSIVAMENTE PARA USO AGRICOLA
-LOS PUNTOS XX Y ZZ SON VERTICES DE LA SERVIDUMBRE
-COLINDANTE A: 21001050284700.

LISTADO DE COORDENADAS		
PUNTO	ESTE (m)	NORTE (m)
1	454906.15	1142321.97
2	454909.62	1142322.43
3	454912.20	1142314.99
4	454916.25	1142308.71
5	454924.59	1142300.86
6	454947.08	1142282.11
7	454942.21	1142281.37
8	454828.14	1142264.04
9	454824.21	1142268.24
10	454824.90	1142270.41
11	454824.77	1142271.65
12	454822.65	1142276.85
13	454817.97	1142287.98
14	454809.17	1142309.19

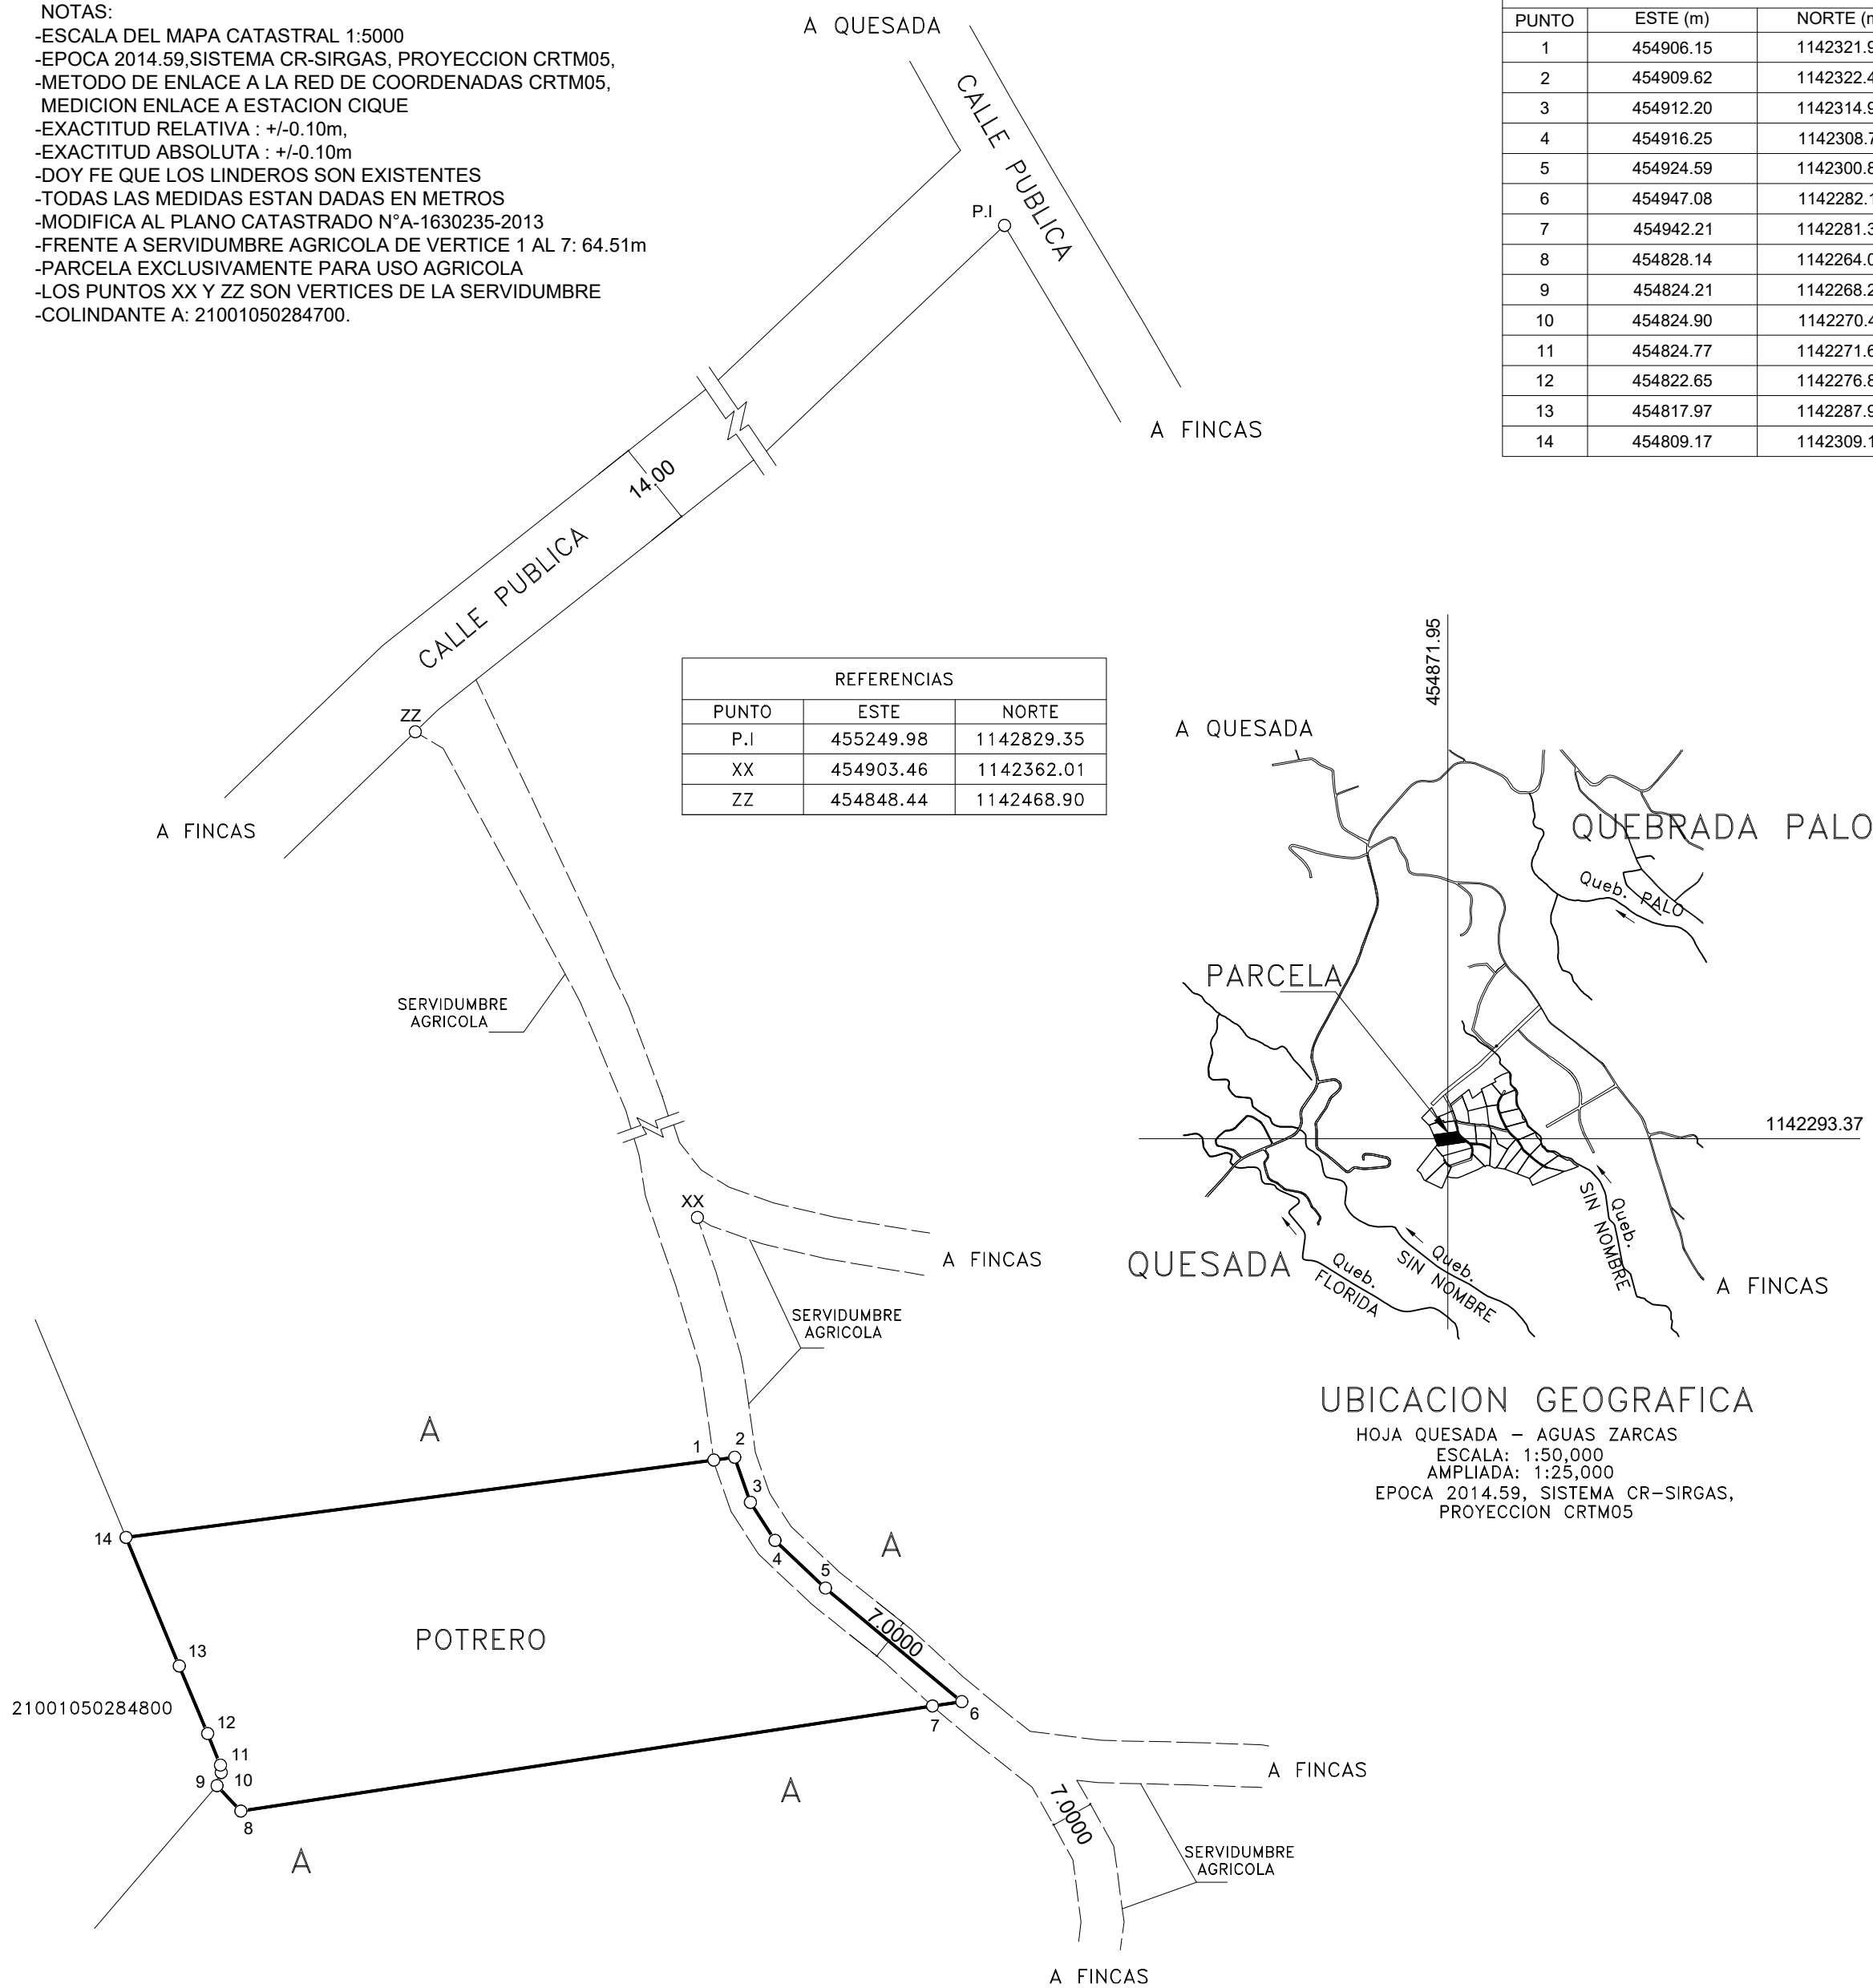

PROTOCOLO: TOMO 24381
FOLIO 026

ESCALA 1:1000
FECHA MAYO 2026

SITUADO EN: LA LLANADA
DISTRITO: 1° QUESADA
CANTON: 10° SAN CARLOS
PROVINCIA: 2° ALAJUELA

PARCELA 36

AREA
5000.00m²

ES PARTE DE
FOLIO REAL
2 502847–000
IDENTIFICADOR PREDIAL
21001050284700
AREA SEGUN REGISTRO
34ha1697.65m²

TOPOGRAFO ASOCIADO: T.A. 8914
JORGE MARIO GUERRERO VARGAS