

ENTERO N°
XXXXXXXXXX

NOTAS:


- ESCALA DEL MAPA CATASTRAL 1:5000
- EPOCA 2014.59, SISTEMA CR-SIRGAS, PROYECCION CRTM05,
- METODO DE ENLACE A LA RED DE COORDENADAS CRTM05, MEDICION ENLACE A ESTACION CIQUE
- EXACTITUD RELATIVA : +/-0.10m,
- EXACTITUD ABSOLUTA : +/-0.10m
- DOY FE QUE LOS LINDEROS SON EXISTENTES
- TODAS LAS MEDIDAS ESTAN DADAS EN METROS
- MODIFICA AL PLANO CATASTRADO N°A-1630235-2013
- FRENTE A SERVIDUMBRE AGRICOLA DE VERTICE 1 AL 6: 53.54m
- PARCELA EXCLUSIVAMENTE PARA USO AGRICOLA
- LOS PUNTOS XX Y ZZ SON VERTICES DE LA SERVIDUMBRE
- COLINDANTE A: 21001050284700.

LISTADO DE COORDENADAS

PUNTO	ESTE (m)	NORTE (m)
1	454894.71	1142366.51
2	454899.34	1142366.58
3	454903.07	1142352.27
4	454907.29	1142338.26
5	454909.62	1142322.43
6	454906.15	1142321.97
7	454809.17	1142309.19
8	454794.21	1142345.17
9	454791.32	1142349.73
10	454811.03	1142357.30
11	454850.16	1142367.45
12	454852.22	1142360.75
13	454865.35	1142364.11
14	454890.56	1142366.46

5028.76 m²

REFERENCIAS		
PUNTO	ESTE	NORTE
P.I	455249.98	1142829.35
XX	454903.46	1142362.01
ZZ	454848.44	1142468.90

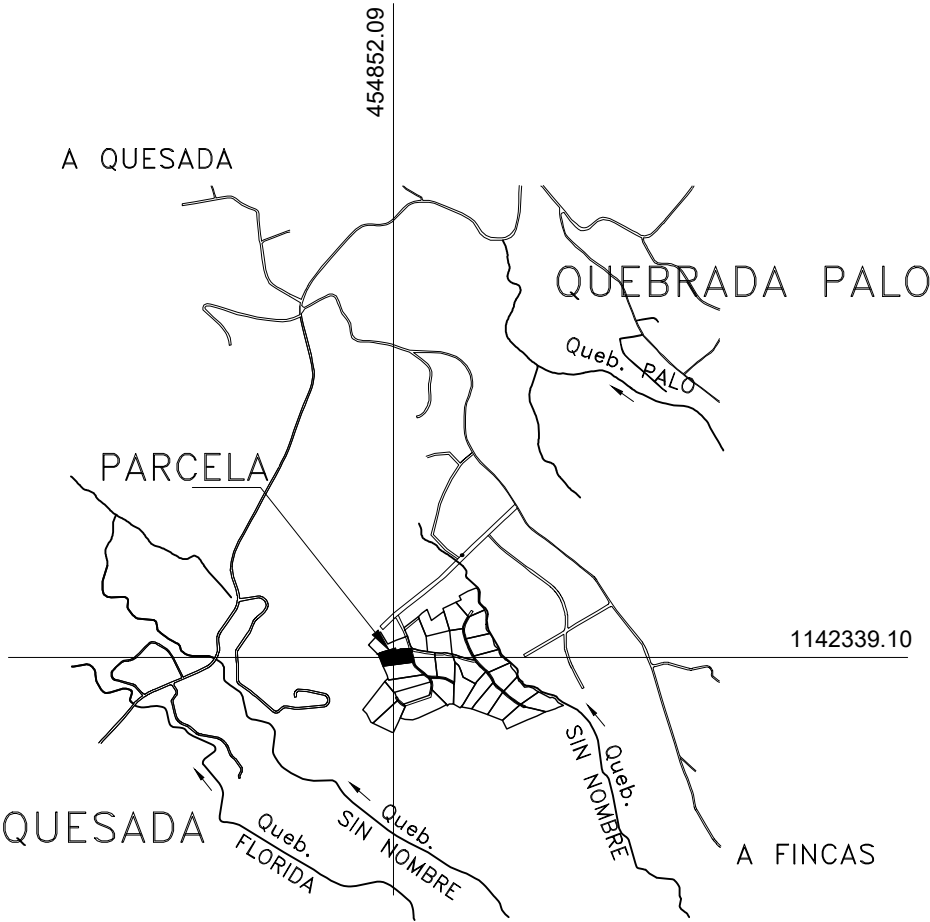

UBICACION GEOGRAFICA
HOJA QUESADA – AGUAS ZARCAS
ESCALA: 1:50,000
AMPLIADA: 1:25,000
EPOCA 2014.59, SISTEMA CR–SIRGAS,
PROYECCION CRTM05

PROTOCOLO: TOMO 24381
FOLIO 026

ESCALA 1:1000
FECHA MAYO 2026

SITUADO EN: LA LLANADA
DISTRITO: 1° QUESADA
CANTON: 10° SAN CARLOS
PROVINCIA: 2° ALAJUELA

PARCELA 37

AREA
5028.76m²

ES PARTE DE
FOLIO REAL
2 502847–000
IDENTIFICADOR PREDIAL
21001050284700
AREA SEGUN REGISTRO
34ha1697.65m²

TOPOGRAFO ASOCIADO: T.A. 8914
JORGE MARIO GUERRERO VARGAS