



ENTERO N°
XXXXXXXXXX

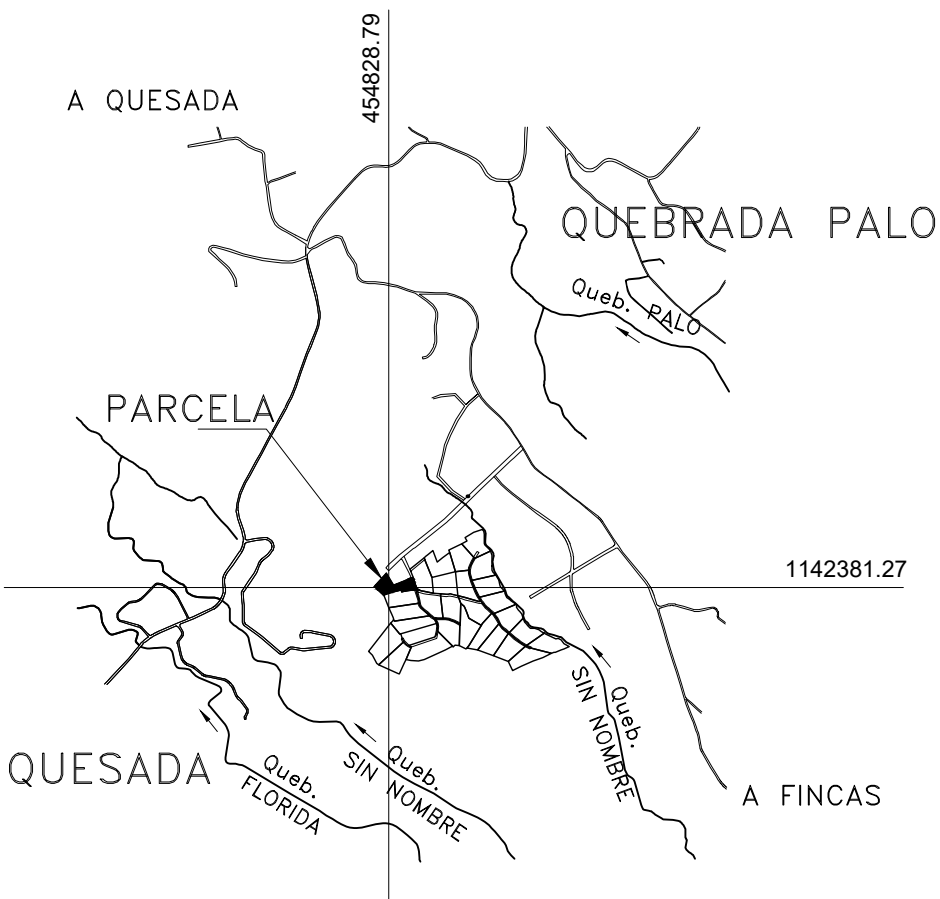

UBICACION GEOGRAFICA

HOJA QUESADA – AGUAS ZARCAS
ESCALA: 1:50,000
AMPLIADA: 1:25,000
EPOCA 2014.59, SISTEMA CR–SIRGAS,
PROYECCION CRTM05

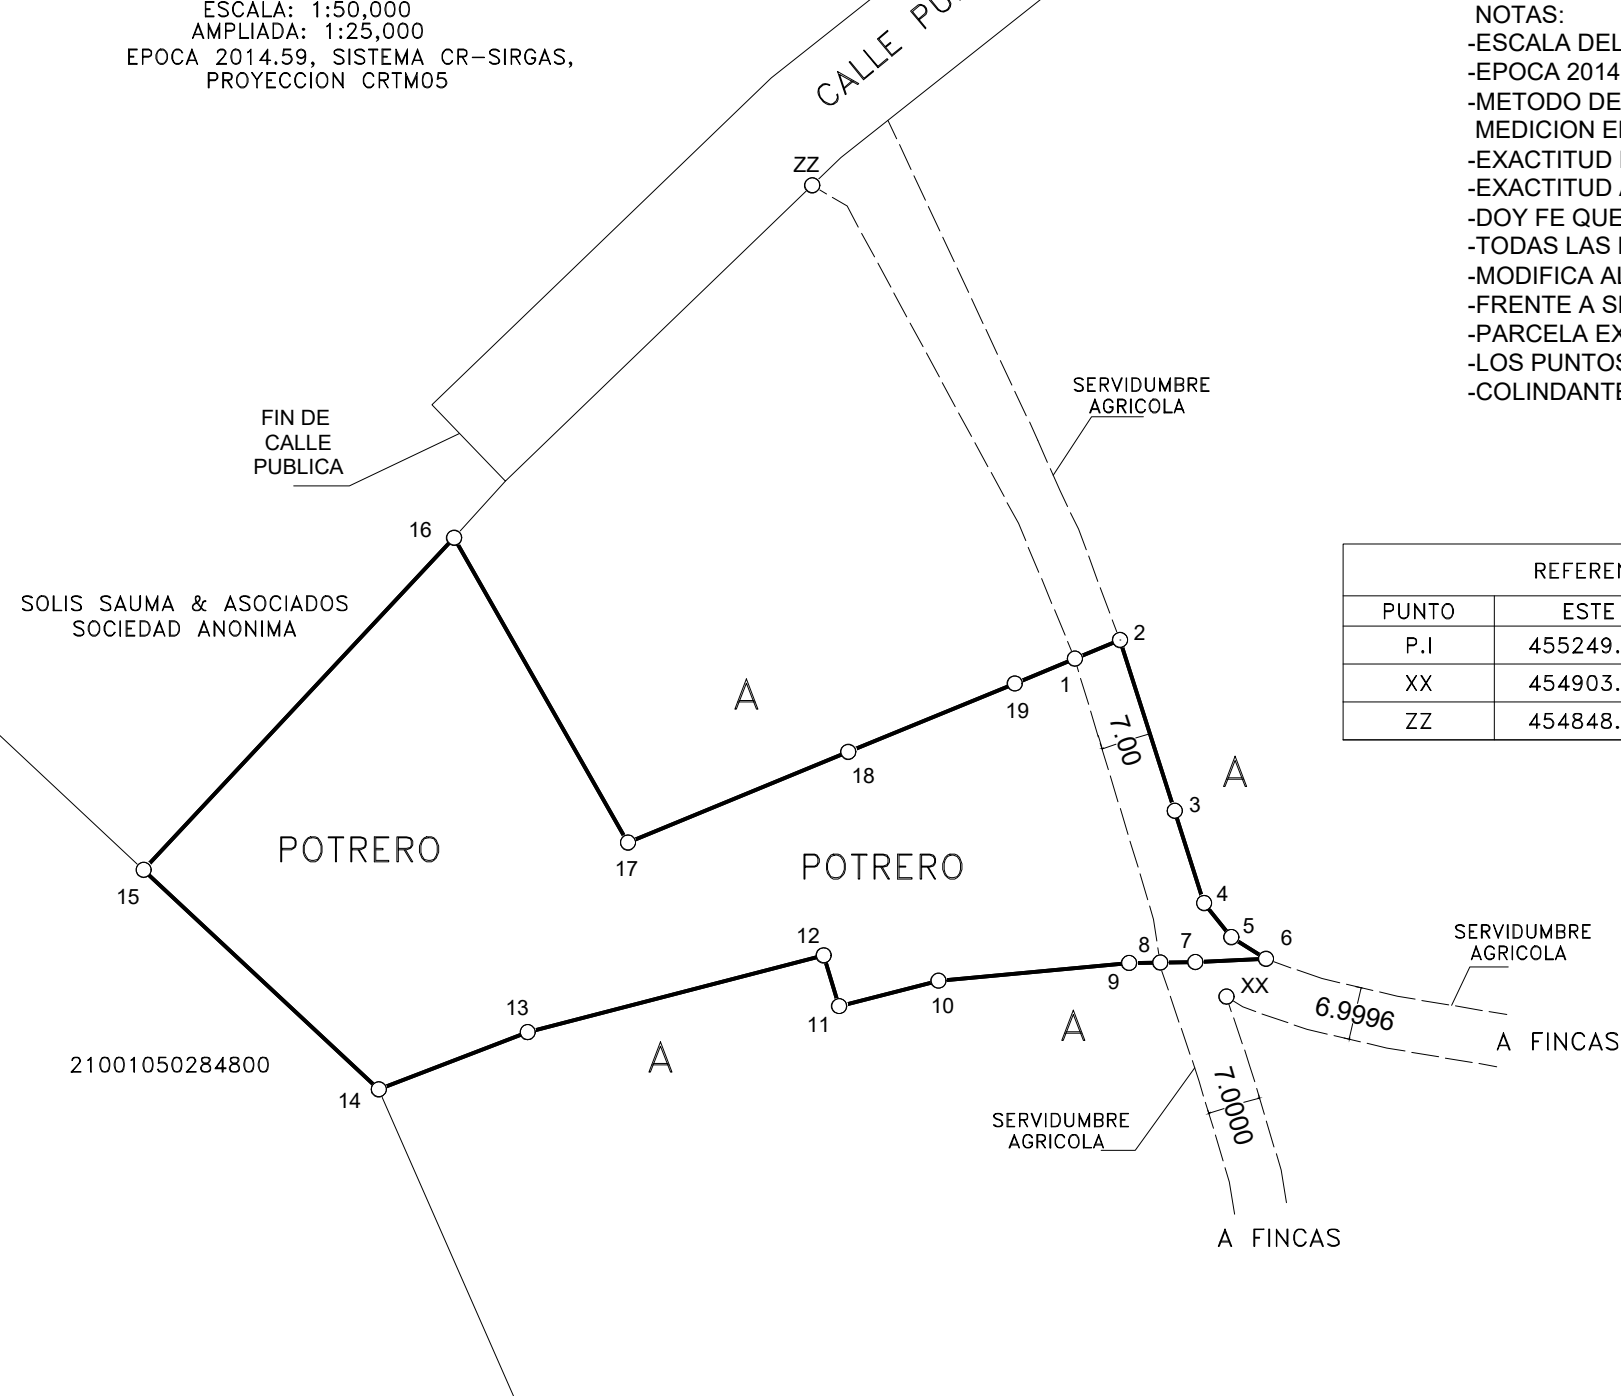

NOTAS:
-ESCALA DEL MAPA CATASTRAL 1:5000
-EPOCA 2014.59,SISTEMA CR-SIRGAS, PROYECCION CRTM05,
-METODO DE ENLACE A LA RED DE COORDENADAS CRTM05,
MEDICION ENLACE A ESTACION CIQUE
-EXACTITUD RELATIVA : +/-0.10m,
-EXACTITUD ABSOLUTA : +/-0.10m
-DOY FE QUE LOS LINDEROS SON EXISTENTES
-TODAS LAS MEDIDAS ESTAN DADAS EN METROS
-MODIFICA AL PLANO CATASTRADO N°A-1630235-2013
-FRENTE A SERVIDUMBRE AGRICOLA DE VERTICE 1 AL 8: 68.17m
-PARCELA EXCLUSIVAMENTE PARA USO AGRICOLA
-LOS PUNTOS XX Y ZZ SON VERTICES DE LA SERVIDUMBRE
-COLINDANTE A: 21001050284700.

REFERENCIAS		
PUNTO	ESTE	NORTE
P.I	455249.98	1142829.35
XX	454903.46	1142362.01
ZZ	454848.44	1142468.90

LISTADO DE COORDENADAS		
PUNTO	ESTE (m)	NORTE (m)
1	454827.11	1141374.37
2	454833.09	1141376.83
3	454840.33	1141354.25
4	454844.22	1141342.04
5	454847.80	1141337.54
6	454852.41	1141334.65
7	454843.05	1141334.24
8	454838.41	1141334.18
9	454834.27	1141334.12
10	454809.06	1141331.78
11	454795.93	1141328.42
12	454793.87	1141335.12
13	454754.74	1141324.97
14	454735.03	1141317.39
15	454703.94	1141346.44
16	454744.99	1141390.34
17	454768.01	1141350.04
18	454797.13	1141362.03
19	454819.16	1141371.10

PROTOCOLO: TOMO 24381
FOLIO 026

ESCALA 1:1000
FECHA MAYO 2026

SITUADO EN: LA LLANADA
DISTRITO: 1° QUESADA
CANTON: 10° SAN CARLOS
PROVINCIA: 2° ALAJUELA

PARCELA 38

AREA
5022.91m²

ES PARTE DE
FOLIO REAL
2 502847–000
IDENTIFICADOR PREDIAL
21001050284700
AREA SEGUN REGISTRO
34ha1697.65m²

TOPOGRAFO ASOCIADO: T.A. 8914
JORGE MARIO GUERRERO VARGAS