


ENTERO N°
XXXXXXXXXX

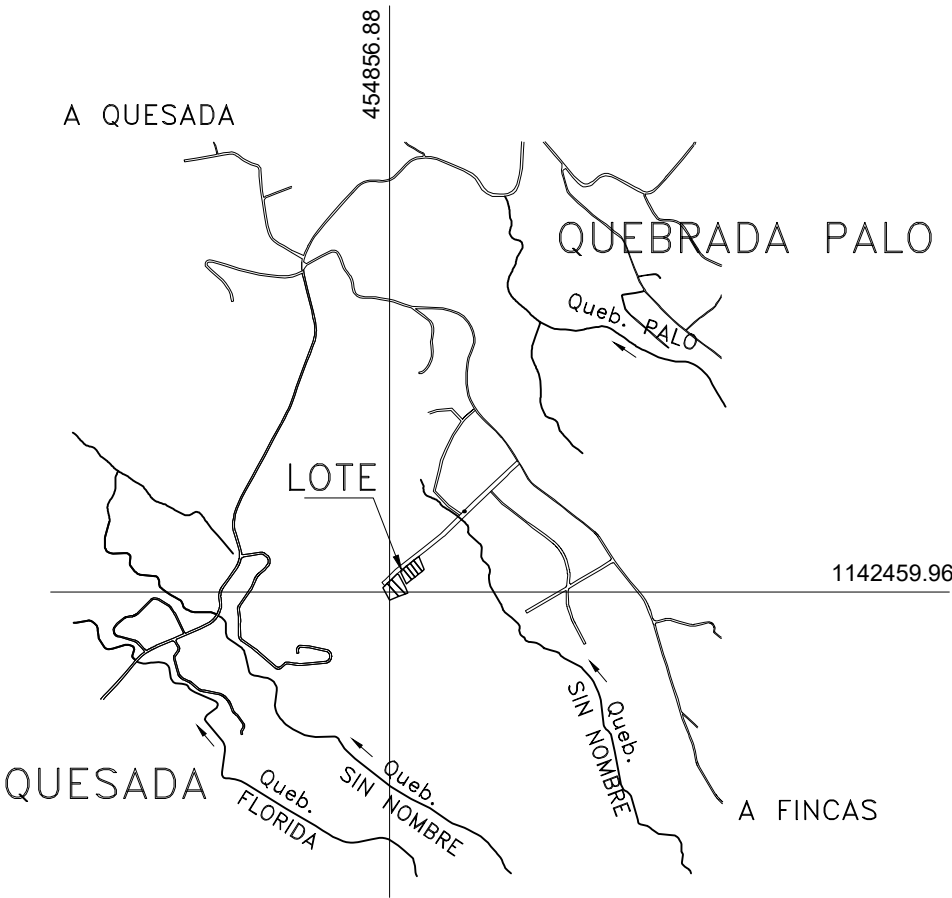


UBICACION GEOGRAFICA

HOJA QUESADA - AGUAS ZARCAS
ESCALA: 1:50,000
AMPLIADA: 1:25,000
EPOCA 2014.59, SISTEMA CR-SIRGAS,
PROYECCION CRTM05

LISTADO DE COORDENADAS		
PUNTO	ESTE (m)	NORTE (m)
1	454859.57	1142478.10
2	454868.22	1142485.05
3	454896.11	1142449.73
4	454878.53	1142435.62
5	454861.03	1142472.93
6	454861.47	1142473.26
7	454859.41	1142475.94
8	454860.39	1142476.39

REFERENCIAS		
PUNTO	ESTE	NORTE
P.I	455249.98	1142829.35

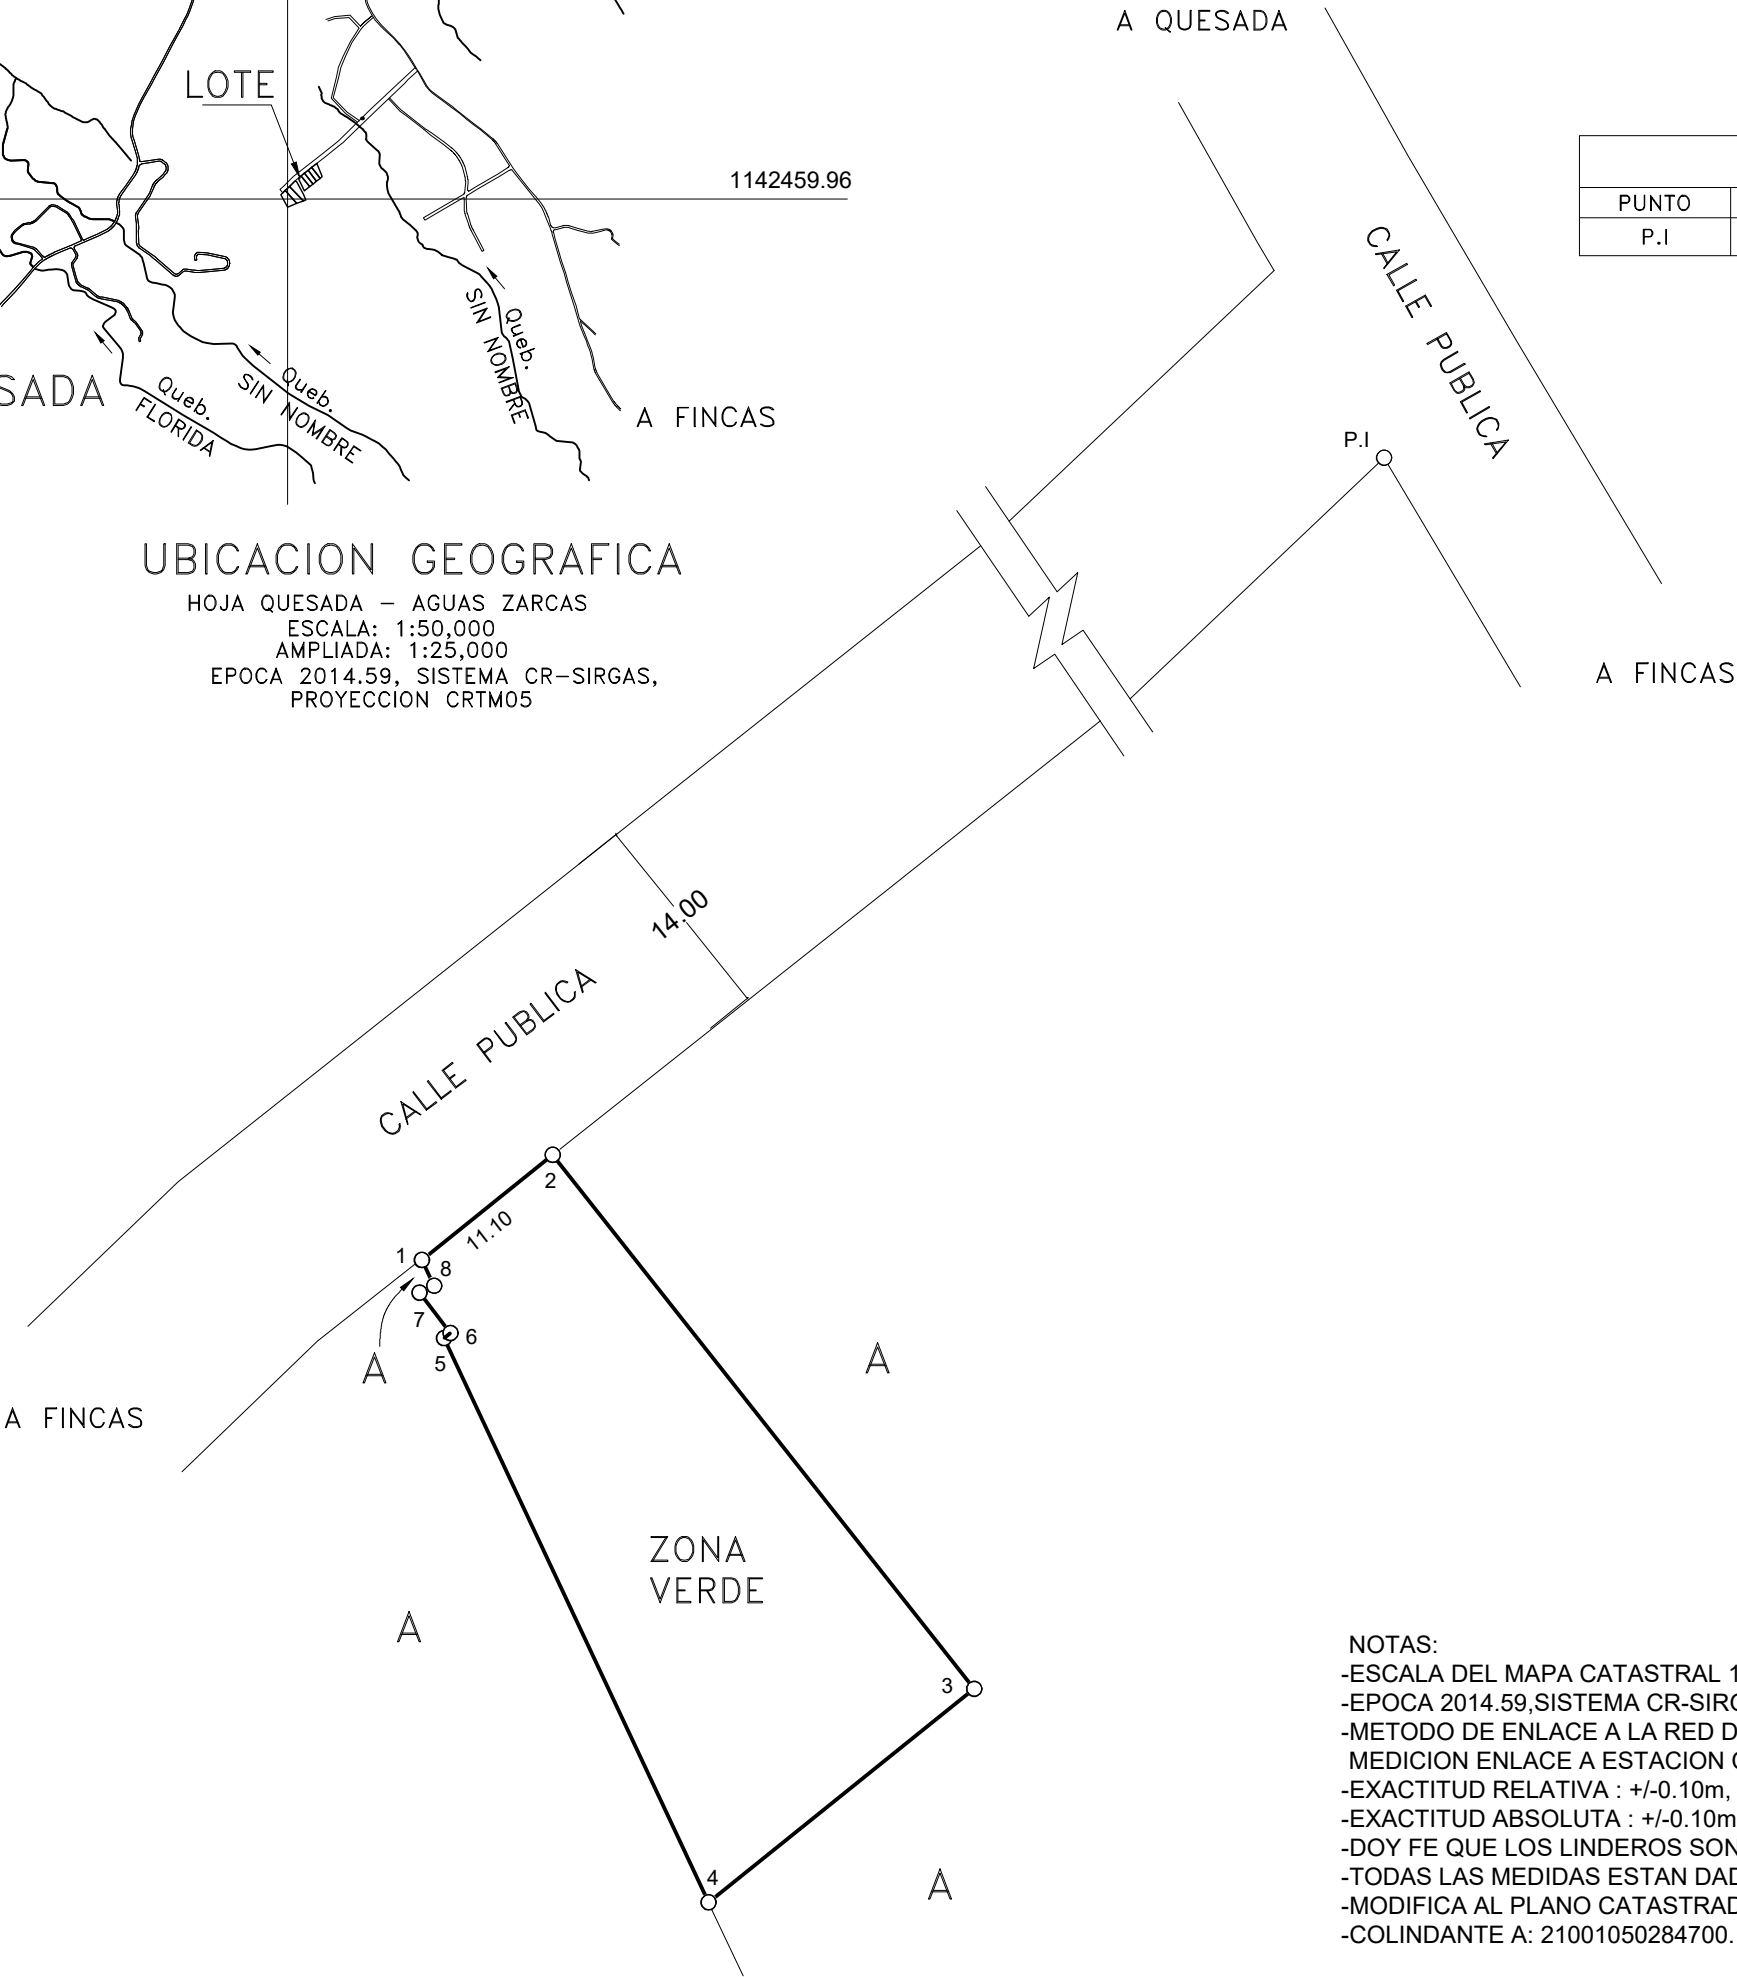

NOTAS:
-ESCALA DEL MAPA CATASTRAL 1:5000
-EPOCA 2014.59,SISTEMA CR-SIRGAS, PROYECCION CRTM05,
-METODO DE ENLACE A LA RED DE COORDENADAS CRTM05,
MEDICION ENLACE A ESTACION CIQUE
-EXACTITUD RELATIVA : +/-0.10m,
-EXACTITUD ABSOLUTA : +/-0.10m
-DOY FE QUE LOS LINDEROS SON EXISTENTES
-TODAS LAS MEDIDAS ESTAN DADAS EN METROS
-MODIFICA AL PLANO CATASTRADO N°A-1721978-2014
-COLINDANTE A: 21001050284700.

PROTOCOLO: TOMO 24381
FOLIO 026

ESCALA 1:500
FECHA MAYO 2026

SITUADO EN: LA LLANADA
DISTRITO: 1° QUESADA
CANTON: 10° SAN CARLOS
PROVINCIA: 2° ALAJUELA

AREA
775.02m²

ES PARTE DE
FOLIO REAL
2 516134-000
IDENTIFICADOR PREDIAL
21001051613400
AREA SEGUN REGISTRO
1ha4183.00m²

TOPOGRAFO ASOCIADO: T.A. 8914
JORGE MARIO GUERRERO VARGAS