


ENTERO N°
XXXXXXXXXX

NOTAS:
-ESCALA DEL MAPA CATASTRAL 1:5000
-EPOCA 2014.59,SISTEMA CR-SIRGAS, PROYECCION CRTM05,
-METODO DE ENLACE A LA RED DE COORDENADAS CRTM05,
MEDICION ENLACE A ESTACION CIQUE
-EXACTITUD RELATIVA : +/-0.10m,
-EXACTITUD ABSOLUTA : +/-0.10m
-DOY FE QUE LOS LINDEROS SON EXISTENTES
-TODAS LAS MEDIDAS ESTAN DADAS EN METROS
-MODIFICA AL PLANO CATASTRADO N°A-1721978-2014
-FRENTE A SERVIDUMBRE AGRICOLA DE VERTICE 1 AL 2: 7.34m
-PARCELA EXCLUSIVAMENTE PARA USO AGRICOLA
-LOS PUNTOS XX Y ZZ SON VERTICES DE LA SERVIDUMBRE
-COLINDANTE A: 21001050284700.


LISTADO DE COORDENADAS		
PUNTO	ESTE (m)	NORTE (m)
1	454928.23	1142466.55
2	454925.57	1142473.39
3	454931.20	1142477.91
4	454937.45	1142483.24
5	454954.92	1142497.13
6	454969.41	1142459.85
7	454986.99	1142473.52
8	455009.50	1142491.03
9	455028.96	1142427.00
10	454951.03	1142408.18

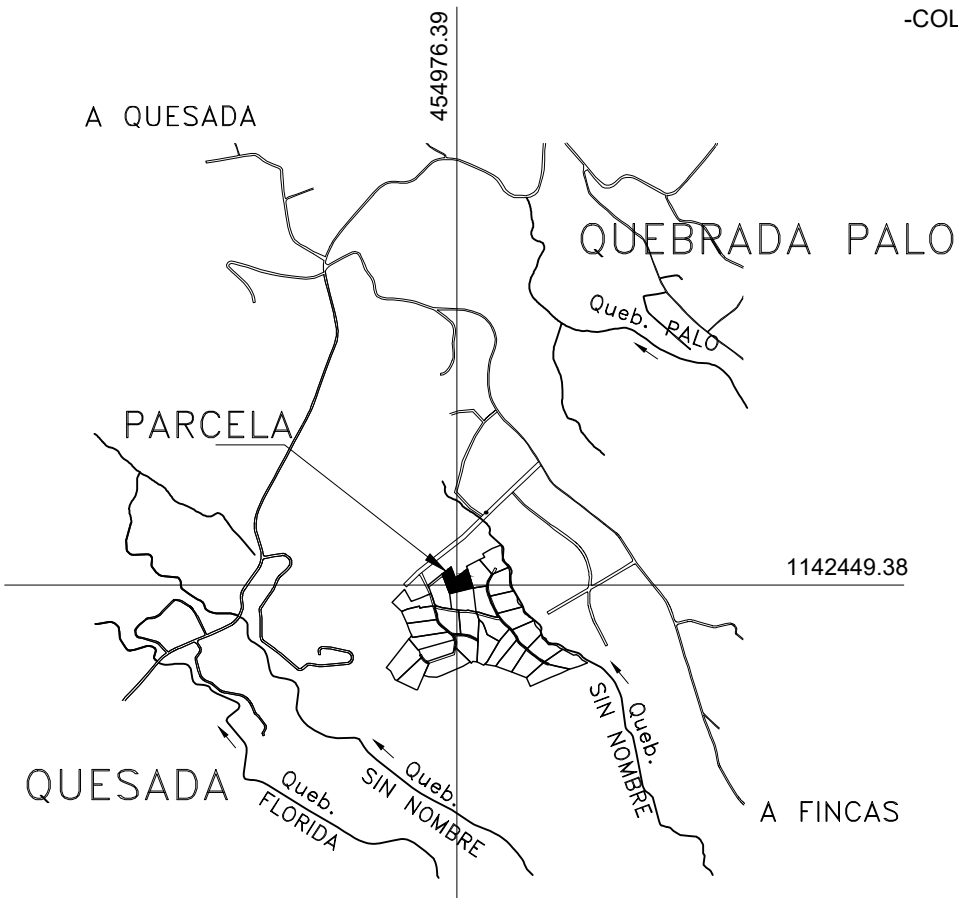

UBICACION GEOGRAFICA

HOJA QUESADA – AGUAS ZARCAS
ESCALA: 1:50,000
AMPLIADA: 1:25,000
EPOCA 2014.59, SISTEMA CR–SIRGAS,
PROYECCION CRTM05

REFERENCIAS		
PUNTO	ESTE	NORTE
P.I	455249.98	1142829.35
XX	454878.53	1142435.61
ZZ	454850.63	1142471.01

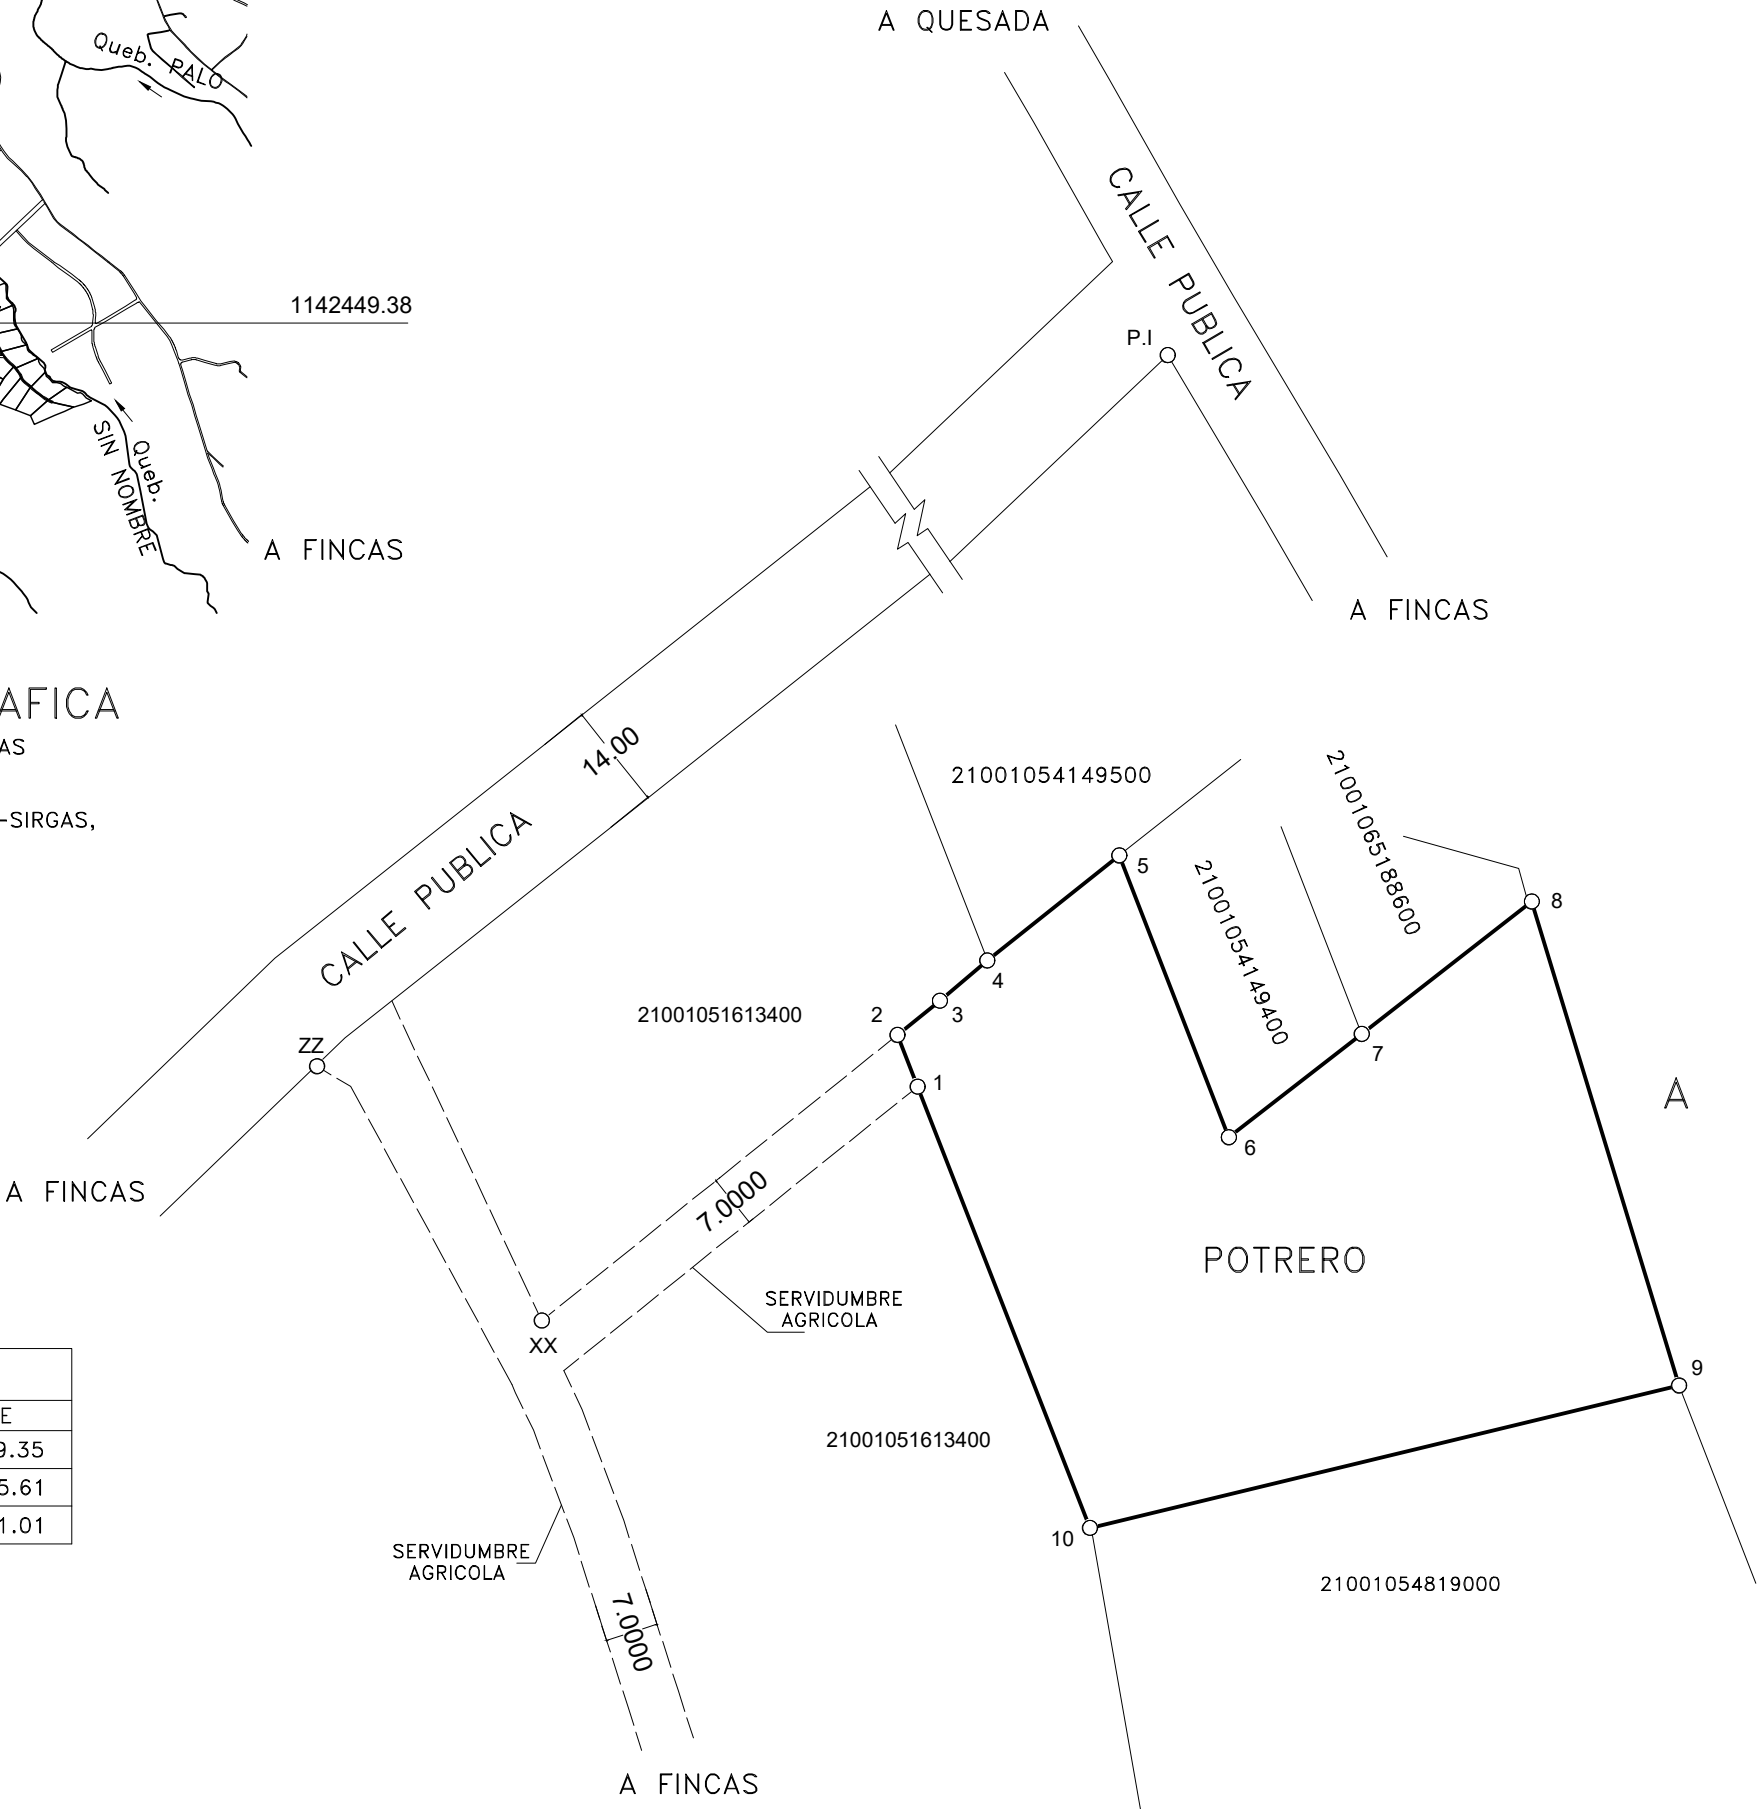

TOPOGRAFO ASOCIADO: T.A. 8914
JORGE MARIO GUERRERO VARGAS

PROTOCOLO: TOMO 24381
FOLIO 026

ESCALA 1:1000
FECHA MAYO 2026

SITUADO EN: LA LLANADA
DISTRITO: 1° QUESADA
CANTON: 10° SAN CARLOS
PROVINCIA: 2° ALAJUELA

PARCELA 40

AREA
5405.63m²

ES PARTE DE
FOLIO REAL
2 516134–000
IDENTIFICADOR PREDIAL
21001051613400
AREA SEGUN REGISTRO
1ha4183.00m²