



ENTERO N°
XXXXXXXXXX

NOTAS:
-ESCALA DEL MAPA CATASTRAL 1:5000
-EPOCA 2014.59,SISTEMA CR-SIRGAS, PROYECCION CRTM05,
-METODO DE ENLACE A LA RED DE COORDENADAS CRTM05,
MEDICION ENLACE A ESTACION CIQUE
-EXACTITUD RELATIVA : +/-0.10m,
-EXACTITUD ABSOLUTA : +/-0.10m
-DOY FE QUE LOS LINDEROS SON EXISTENTES
-TODAS LAS MEDIDAS ESTAN DADAS EN METROS
-MODIFICA AL PLANO CATASTRADO N°A-1721978-2014
-COLINDANTE A: 21001050284700.

LISTADO DE COORDENADAS		
PUNTO	ESTE (m)	NORTE (m)
1	454879.92	1142494.44
2	454891.62	1142503.84
3	454919.50	1142468.52
4	454907.80	1142459.12

675.00 m²

REFERENCIAS		
PUNTO	ESTE	NORTE
P.I	455249.98	1142829.35

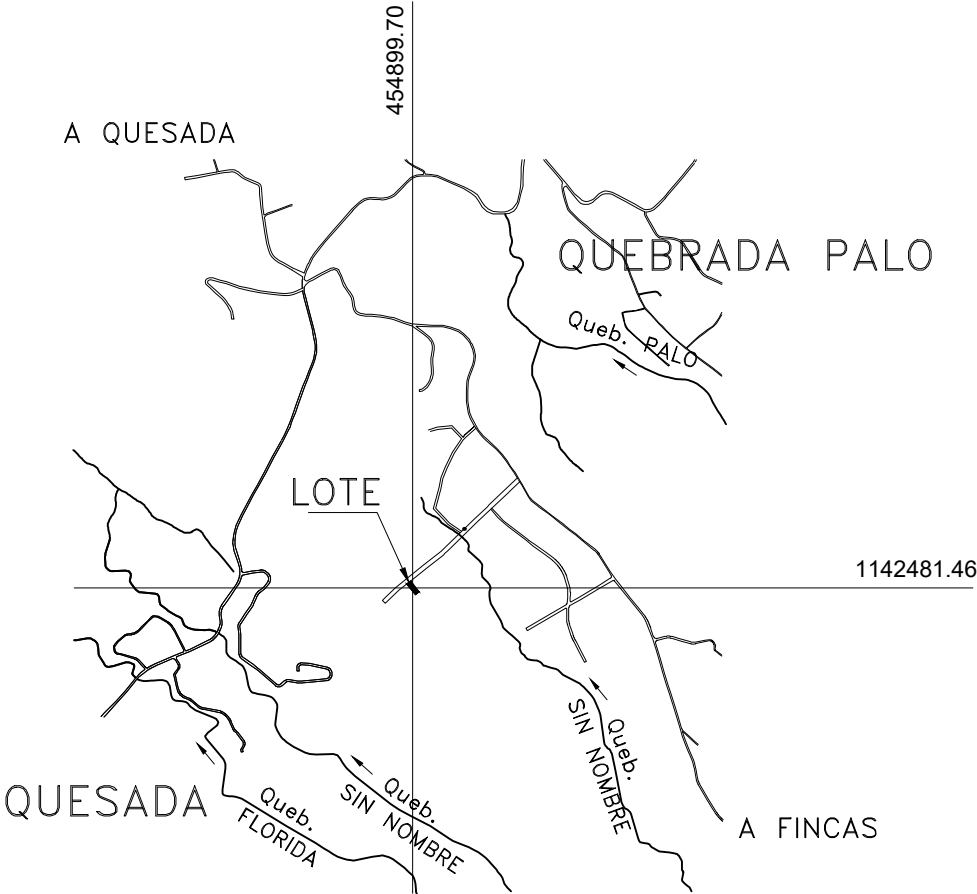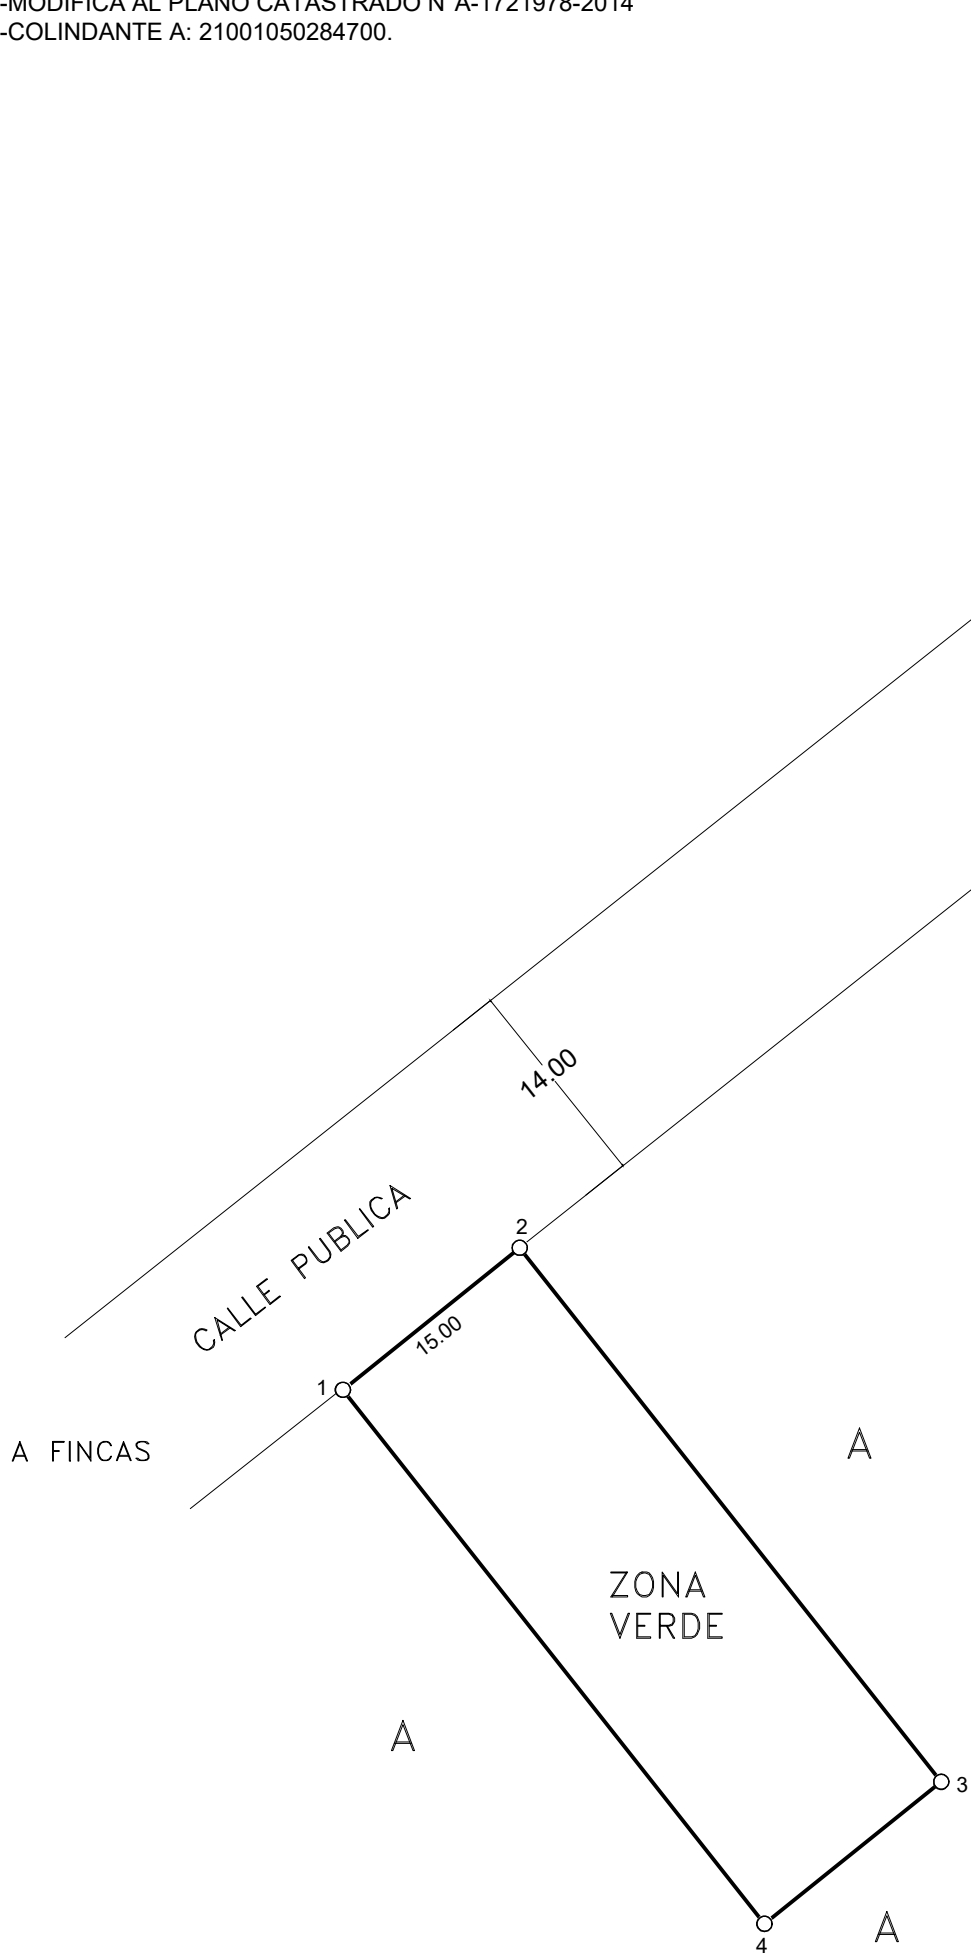

UBICACION GEOGRAFICA
HOJA QUESADA – AGUAS ZARCAS
ESCALA: 1:50,000
AMPLIADA: 1:25,000
EPOCA 2014.59, SISTEMA CR–SIRGAS,
PROYECCION CRTM05

PROTOCOLO: TOMO 24381
FOLIO 026

ESCALA 1:500
FECHA MAYO 2026

SITUADO EN: LA LLANADA
DISTRITO: 1° QUESADA
CANTON: 10° SAN CARLOS
PROVINCIA: 2° ALAJUELA

AREA
675.00m²

ES PARTE DE
FOLIO REAL
2 516134–000
IDENTIFICADOR PREDIAL
21001051613400
AREA SEGUN REGISTRO
1ha4183.00m²

TOPOGRAFO ASOCIADO: T.A. 8914
JORGE MARIO GUERRERO VARGAS