COMPROBANTE DE INSCRIPCION CATASTRAL

REGISTRO NACIONAL
REPÚBLICA DE COSTA RICA

REGISTRO INMOBILIARIO
SUBDIRECCIÓN CATASTRAL

INSCRIPCIÓN No:
2-3541-2026


Fecha : 23/01/2026 11:56:58
Registrador: DAVID AGUERO AZOFEIFA
22CBC7EC5F25547915F1522BD42A8293

La provisionalidad de este documento está sujeta a lo establecido en el artículo 151 del Reglamento General del Registro Inmobiliario.

Catastro Nacional
2025-85824-C
22/01/2026 09:48:55
REINGRESO NORMAL

cfia
Contrato 1226138
Fecha 21/01/2026
Sellado CFIA

No de entero: 623054841 y 634973827

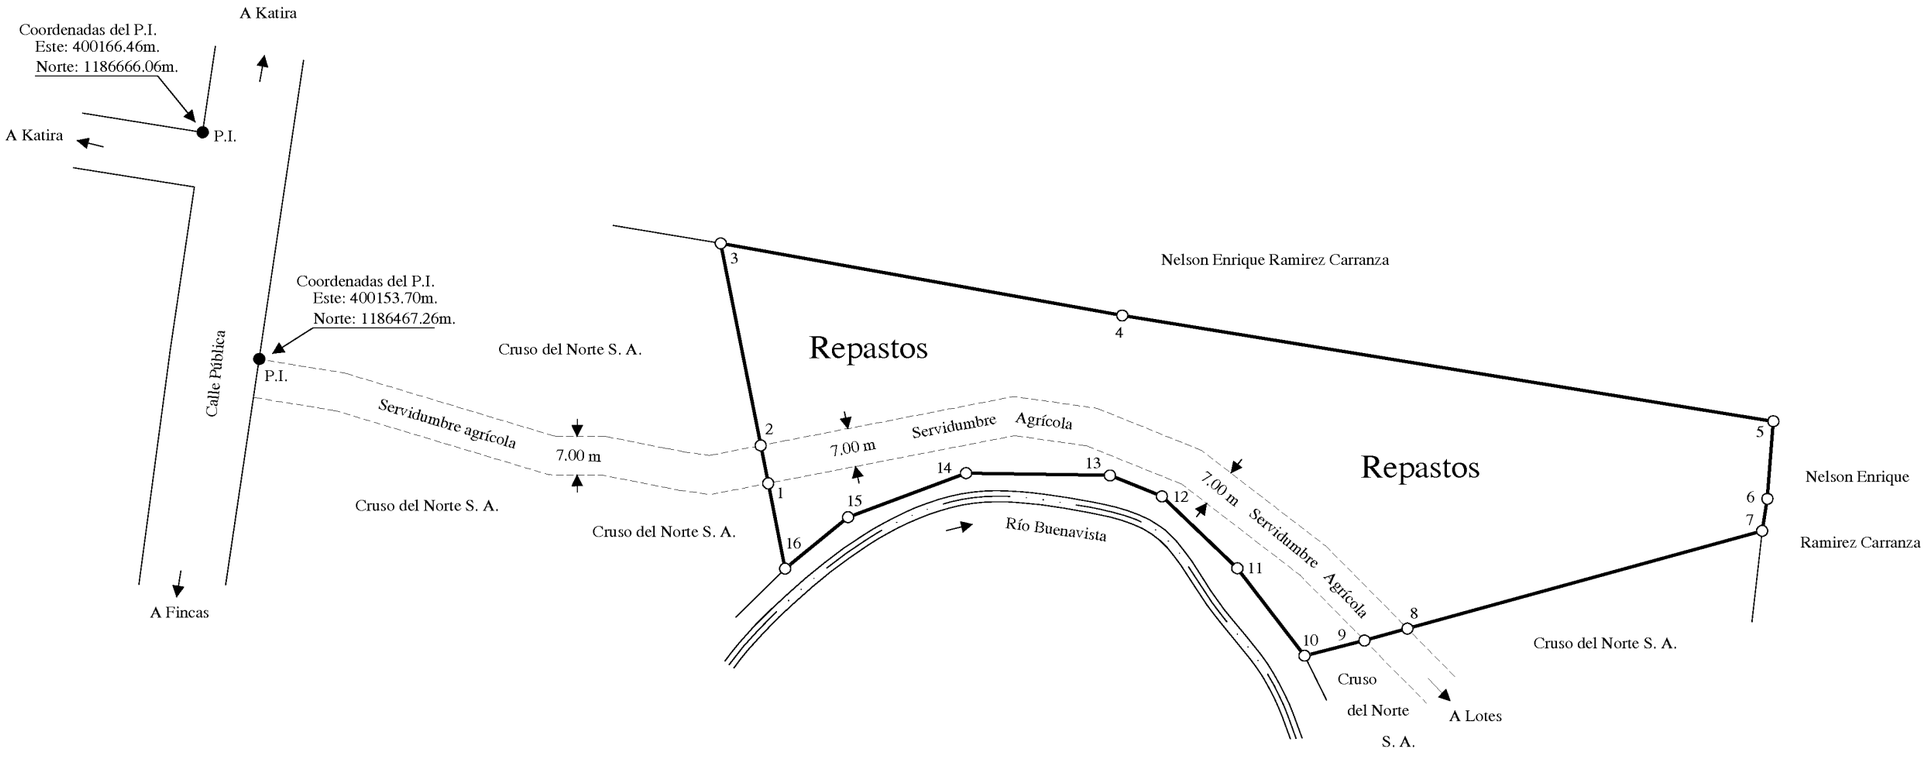


LISTADO DE COORDENADAS		
VERTICE	ESTE (m)	NORTE (m)
1	400732.16	1186388.90
2	400730.82	1186395.77
3	400723.68	1186432.45
4	400795.38	1186419.37
5	400911.65	1186400.17
6	400910.58	1186386.09
7	400909.65	1186380.27
8	400846.31	1186362.53
9	400838.63	1186360.38
10	400827.94	1186357.61
11	400815.94	1186373.48
12	400802.46	1186386.54
13	400793.19	1186390.33
14	400767.49	1186390.75
15	400746.42	1186382.75
16	400735.17	1186373.42

UBICACION GEOGRAFICA

HOJA GUATUSO - ESCALA 1:50000
Época 2014.59, Sistema CR-SIRGAS, Proyección CRTM05

400000 401000

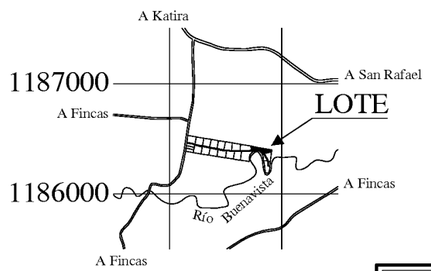

NOTAS:

Época 2014.59, Sistema CR-SIRGAS, Proyección CRTM05.
Método de enlace a la red de coordenadas CRTM 05, medición NTRIP con equipo GNSS
Enlazado a la estación TOPOMUR, datos medidos en época 2019.24 y trasladados a la época 2014.59.
Exactitud relativa: +- 0.10m.
Exactitud absoluta: +- 0.10m.
Escala de la ortofoto 1:5000
Doy fe que los linderos son existentes.
Distancia frente a servidumbre agrícola del 1 al 2 con 7.00 metros y de 8 a 9 con 7.97 metros.
Afectado por la Ley Forestal No. 7575, Artículo 33.
Modifica al Plano Catastrado No. A-0608756-1985.

En concordancia con lo dispuesto en los artículos 33 y 34 de la Ley de Planificación Urbana N° 4820, se otorga el Visado Municipal a 2025 - 85824 - C, Trámite APT-388-2025, Resolución 321-122025.

MARYELY MARIELA CORONADO RAMOS (FIRMA)
Firmado digitalmente por MARYELY MARIELA CORONADO RAMOS (FIRMA)
Fecha: 2026.01.20 13:45:08 -06'00'

Ing. Maryely Coronado Ramos
Coordinadora Catastro-Bienes Inmuebles
Municipalidad de Guatuso

PARA SEGREGACION DE FINCA
UNICAMENTE PARA USO AGRICOLA

SITUADO EN:	KATIRA
DISTRITO:	04 KATIRA
CANTON:	15 GUATUSO
PROVINCIA:	02 ALAJUELA

JORGE MARIO GUERRERO VARGAS (FIRMA)
Firmado digitalmente por JORGE MARIO GUERRERO VARGAS (FIRMA)
Fecha: 2026.01.14 13:23:42 -06'00'

JORGE MARIO GUERRERO VARGAS
TOPOGRAFO ASOCIADO T.A. 8914

ES PARTE DE LA FINCA INSCRITA AL FOLIO REAL
NUMERO:
2220270-000
ÁREA SEGUN REGISTRO:
129218.52m^2

AREA:
7087.42 m ^{2}

PROTOCOLO TOMO	23920
FOLIO	138
ESCALA:	1:1000
FECHA:	OCTUBRE 2025