COMPROBANTE DE INSCRIPCION CATASTRAL

REGISTRO NACIONAL
REPÚBLICA DE COSTA RICA

REGISTRO INMOBILIARIO
SUBDIRECCIÓN CATASTRAL

INSCRIPCIÓN No:
2-3547-2026

Fecha : 23/01/2026 11:58:19
Registrador: DAVID AGUERO AZOFEIFA
5A45DC060C5A538D0CDD25DAD9EE0D4F


La provisionalidad de este documento está sujeta a lo establecido en el artículo 151 del Reglamento General del Registro Inmobiliario.

Catastro Nacional
2025-85831-C
22/01/2026 09:56:03
REINGRESO NORMAL


cfia
Contrato 1226138
Fecha 21/01/2026
Sellado CFIA

No de entero: 623057719 y 634988760

LISTADO DE COORDENADAS		
VERTICE	ESTE (m)	NORTE (m)
1	400360.76	1186418.74
2	400421.39	1186406.65
3	400433.34	1186404.27
4	400422.55	1186338.77
5	400380.64	1186345.60
6	400349.76	1186350.56

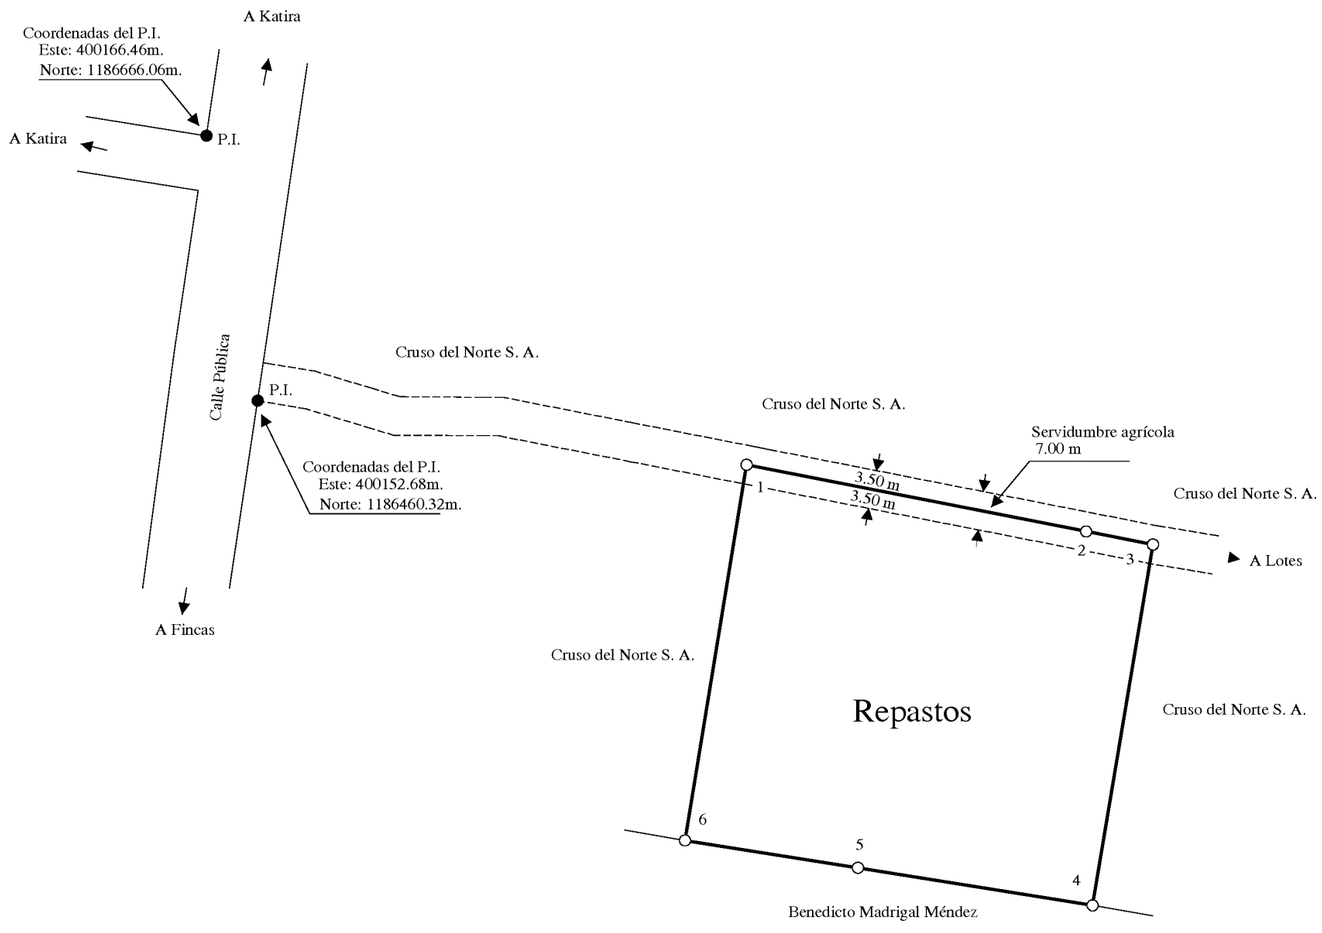

UBICACION GEOGRAFICA
HOJA GUATUSO - ESCALA 1:50000
Época 2014.59, Sistema CR-SIRGAS, Proyección CRTM05

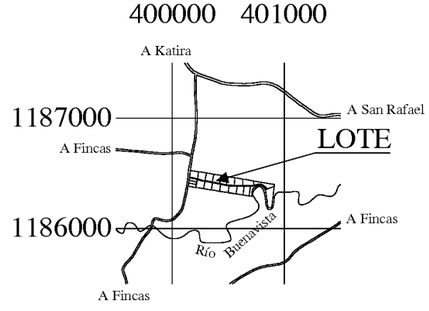

NOTAS:

Época 2014.59, Sistema CR-SIRGAS, Proyección CRTM05.
Método de enlace a la red de coordenadas CRTM 05, medición NTRIP con equipo GNSS
Enlazado a la estación TOPOMUR, datos medidos en época 2019.24 y trasladados a la época 2014.59.
Exactitud relativa: +- 0.10m.
Exactitud absoluta: +- 0.10m.
Escala de la ortofoto 1:5000
Doy fe que los linderos son existentes.
Distancia frente a servidumbre agrícola del 1 al 3 con 74.00 metros.
Modifica al Plano Catastrado No. A-0608756-1985.

En concordancia con lo dispuesto en los artículos 33 y 34 de la Ley de Planificación Urbana N° 4820, se otorga el Visado Municipal a 2025 - 85831 - C, Trámite APT-388-2025, Resolución 321-122025.

MARYELY MARIELA CORONADO RAMOS (FIRMA)
Firmado digitalmente por MARYELY MARIELA CORONADO RAMOS (FIRMA)
Fecha: 2026.01.20 13:49:50 -06'00'

Ing. Maryely Coronado Ramos
Coordinadora Catastro-Bienes Inmuebles
Municipalidad de Guatuso

PARA SEGREGACION DE FINCA
UNICAMENTE PARA USO AGRICOLA

SITUADO EN:	KATIRA
DISTRITO:	04 KATIRA
CANTON:	15 GUATUSO
PROVINCIA:	02 ALAJUELA

ES PARTE DE LA FINCA INSCRITA AL FOLIO REAL NUMERO:
2220270-000
ÁREA SEGUN REGISTRO:
129218.52m^2

AREA:
5000.00 m^2

PROTOCOLO TOMO	23920
FOLIO	138
ESCALA:	1:1000
FECHA:	OCTUBRE 2025

JORGE MARIO GUERRERO VARGAS (FIRMA)
Firmado digitalmente por JORGE MARIO GUERRERO VARGAS (FIRMA)
Fecha: 2026.01.14 13:25:55 -06'00'

JORGE MARIO GUERRERO VARGAS
TOPOGRAFO ASOCIADO T.A. 8914