COMPROBANTE DE INSCRIPCION CATASTRAL

REGISTRO NACIONAL
REPÚBLICA DE COSTA RICA

REGISTRO INMOBILIARIO
SUBDIRECCIÓN CATASTRAL

INSCRIPCIÓN No:
2-3550-2026

Fecha : 23/01/2026 11:59:19
Registrador: DAVID AGUERO AZOFEIFA
30286A96AD25EC1B302A7875183C540E

La provisionalidad de este documento está sujeta a lo establecido en el artículo 151 del Reglamento General del Registro Inmobiliario.


Catastro Nacional
2025-85836-C
22/01/2026 09:58:12
REINGRESO NORMAL


cfia
Contrato 1226138
Fecha 21/01/2026
Sellado CFIA

No de entero: 634989863

LISTADO DE COORDENADAS		
VERTICE	ESTE (m)	NORTE (m)
1	400882.48	1186290.77
2	400875.49	1186290.48
3	400874.81	1186295.15
4	400873.76	1186298.60
5	400872.57	1186301.87
6	400839.99	1186300.51
7	400843.27	1186277.58
8	400847.24	1186248.82
9	400852.40	1186213.47
10	400853.93	1186199.14
11	400857.83	1186189.99
12	400880.19	1186187.44
13	400890.44	1186200.75
14	400898.95	1186279.54
15	400899.94	1186291.48

UBICACION GEOGRAFICA
HOJA GUATUSO - ESCALA 1:50000
Época 2014.59, Sistema CR-SIRGAS, Proyección CRTM05

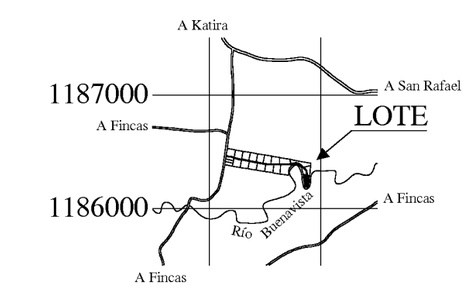

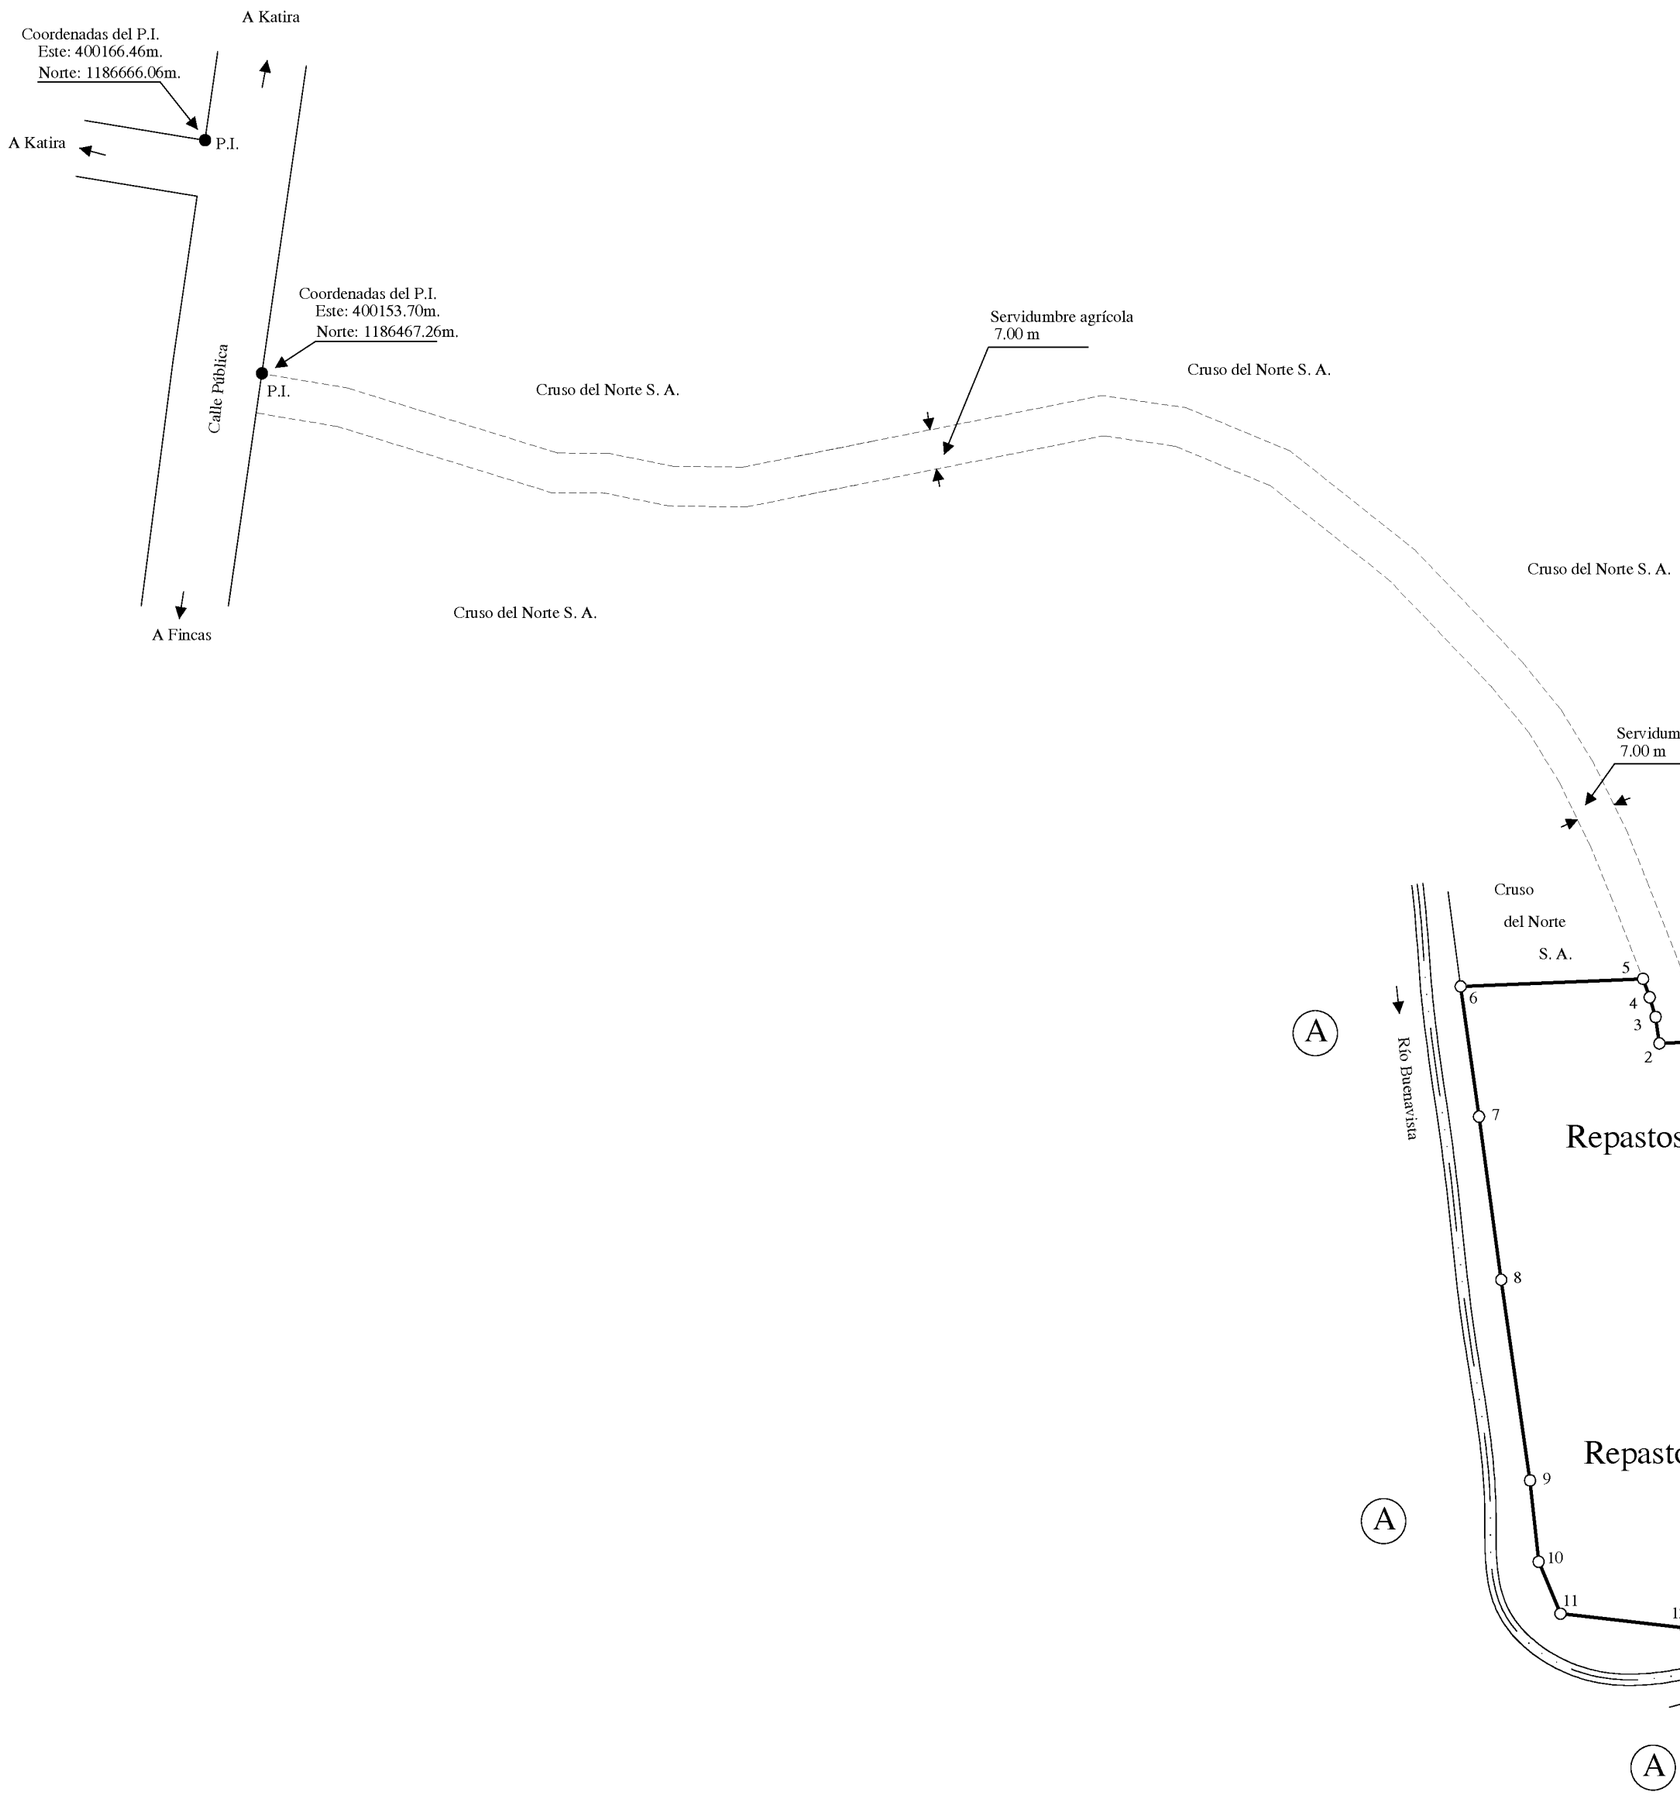

NOTAS:

Época 2014.59, Sistema CR-SIRGAS, Proyección CRTM05.
Método de enlace a la red de coordenadas CRTM 05, medición NTRIP con equipo GNSS
Enlazado a la estación TOPOMUR, datos medidos en época 2019.24 y trasladados a la época 2014.59.
Exactitud relativa: +- 0.10m.
Exactitud absoluta: +- 0.10m.
Escala de la ortofoto 1:5000
Doy fe que los linderos son existentes.
Distancia frente a servidumbre agrícola del 1 a 5 con 18.81 metros.
Modifica al Plano Catastrado No. A-0608756-1985.
Afectado por la Ley Forestal No. 7575, Artículo 33.
Colindante A: Juan Carlos Zúñiga Acuña, Florindo Espinoza Coronado, Edgar Fabio Rojas Rodríguez y Corporación Productiva Rojas Salazar S.A.

En concordancia con lo dispuesto en los artículos 33 y 34 de la Ley de Planificación Urbana N° 4820, se otorga el Visado Municipal a 2025 - 85836 - C, Trámite APT-388-2025, Resolución 321-122025.

MARYELY MARIELA CORONADO RAMOS (FIRMA)
Firmado digitalmente por MARYELY MARIELA CORONADO RAMOS (FIRMA)
Fecha: 2026.01.20 13:52:14 -06'00'

Ing. Maryely Coronado Ramos
Coordinadora Catastro-Bienes Inmuebles
Municipalidad de Guatuso

PARA SEGREGACION DE FINCA
UNICAMENTE PARA USO AGRICOLA

SITUADO EN:	KATIRA
DISTRITO:	04 KATIRA
CANTON:	15 GUATUSO
PROVINCIA:	02 ALAJUELA

ES PARTE DE LA FINCA INSCRITA AL FOLIO REAL NUMERO:
2220270-000
ÁREA SEGUN REGISTRO:
129218.52m^2

AREA:
5000.00 m^2

PROTOCOLO TOMO	23920
FOLIO	138
ESCALA:	1:1000
FECHA:	OCTUBRE 2025

JORGE MARIO GUERRERO VARGAS (FIRMA)
Firmado digitalmente por JORGE MARIO GUERRERO VARGAS (FIRMA)
Fecha: 2026.01.14 13:27:25 -06'00'

JORGE MARIO GUERRERO VARGAS
TOPOGRAFO ASOCIADO T.A. 8914