COMPROBANTE DE INSCRIPCION CATASTRAL

REGISTRO NACIONAL
REPÚBLICA DE COSTA RICA

REGISTRO INMOBILIARIO
SUBDIRECCIÓN CATASTRAL

INSCRIPCIÓN No:
2-3533-2026

Fecha : 23/01/2026 11:34:03
Registrador: DAVID AGUERO AZOFEIFA
B093037B4FF088646566CA6C58ADE4C3


La provisionalidad de este documento está sujeta a lo establecido en el artículo 151 del Reglamento General del Registro Inmobiliario.

Catastro Nacional
2025-85811-C
22/01/2026 09:53:00
REINGRESO NORMAL


cfia
Contrato 1226138
Fecha 21/01/2026
Sellado CFIA

No de entero: 623036916 y 634971450

LISTADO DE COORDENADAS		
VERTICE	ESTE (m)	NORTE (m)
1	400291.25	1186431.99
2	400275.79	1186432.09
3	400224.96	1186447.61
4	400237.02	1186516.50
5	400247.77	1186514.63
6	400303.73	1186504.93

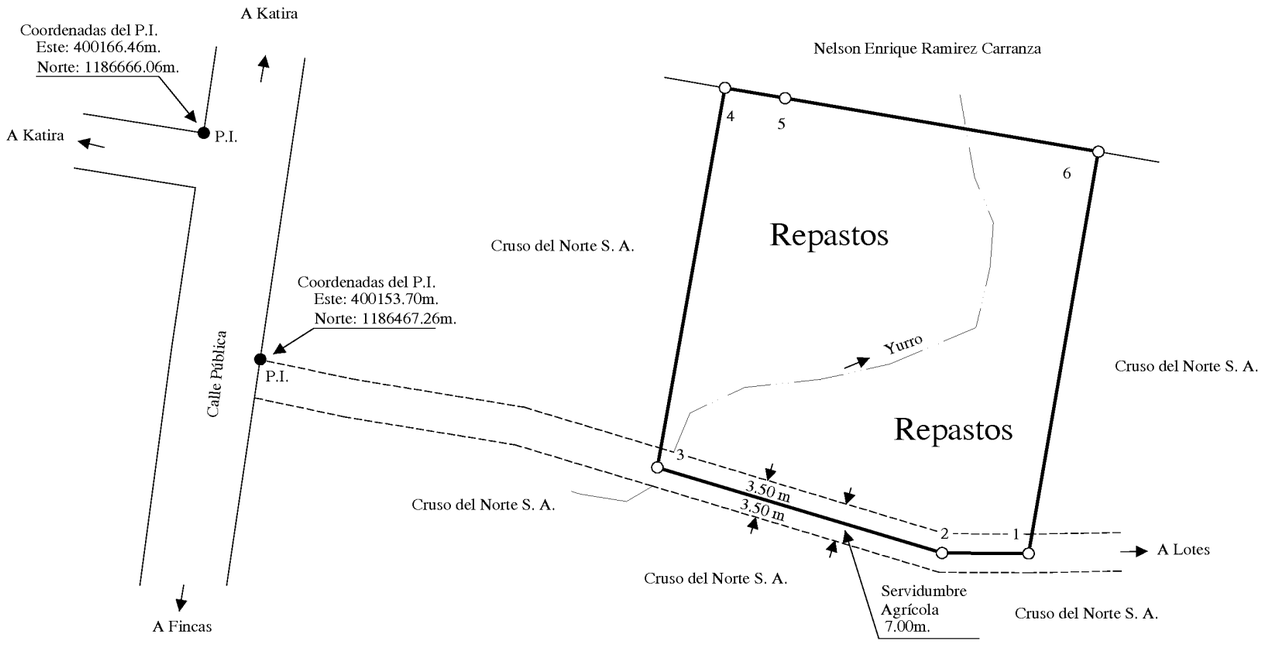

UBICACION GEOGRAFICA
HOJA GUATUSO - ESCALA 1:50000
Época 2014.59, Sistema CR-SIRGAS, Proyección CRTM05

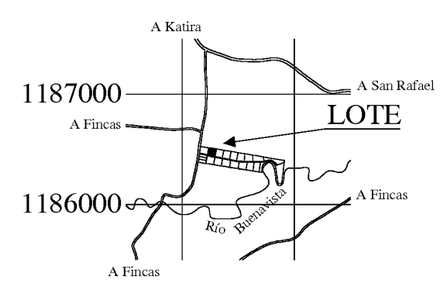

NOTAS:

Época 2014.59, Sistema CR-SIRGAS, Proyección CRTM05.
Método de enlace a la red de coordenadas CRTM 05, medición NTRIP con equipo GNSS
Enlazado a la estación TOPOMUR, datos medidos en época 2019.24 y trasladados a la época 2014.59.
Exactitud relativa: +- 0.10m.
Exactitud absoluta: +- 0.10m.
Escala de la ortofoto 1:5000
Doy fe que los linderos son existentes.
Distancia frente a servidumbre agrícola del 1 al 3 con 68.61 metros.
Afectado por la Ley Forestal No. 7575, Artículo 33 y por la Ley de Aguas No. 276 y sus reformas.
Modifica al Plano Catastrado No. A-0608756-1985.

En concordancia con lo dispuesto en los artículos 33 y 34 de la Ley de Planificación Urbana N° 4820, se otorga el Visado Municipal a 2025 - 85811 - C, Trámite APT-388-2025, Resolución 321-122025.

MARYELY MARIELA CORONADO RAMOS (FIRMA)
Firmado digitalmente por MARYELY MARIELA CORONADO RAMOS (FIRMA)
Fecha: 2026.01.20 13:39:43 -06'00'

Ing. Maryely Coronado Ramos
Coordinadora Catastro-Bienes Inmuebles
Municipalidad de Guatuso

PARA SEGREGACION DE FINCA
UNICAMENTE PARA USO AGRICOLA

SITUADO EN:	KATIRA
DISTRITO:	04 KATIRA
CANTON:	15 GUATUSO
PROVINCIA:	02 ALAJUELA

ES PARTE DE LA FINCA
INSCRITA AL FOLIO REAL
NUMERO:
2220270-000
ÁREA SEGUN REGISTRO:
129218.52m^2

AREA:
5000.00 m ^{2}

PROTOCOLO TOMO	23920
FOLIO	138
ESCALA:	1:1000
FECHA:	OCTUBRE 2025

JORGE MARIO GUERRERO VARGAS (FIRMA)
Firmado digitalmente por JORGE MARIO GUERRERO VARGAS (FIRMA)
Fecha: 2026.01.14 13:19:14 -06'00'

JORGE MARIO GUERRERO VARGAS
TOPOGRAFO ASOCIADO T.A. 8914